


ALLOCATION TO ASSEMBLIES	
Assembly Mark	TOTAL
B/1263	4
Total	4

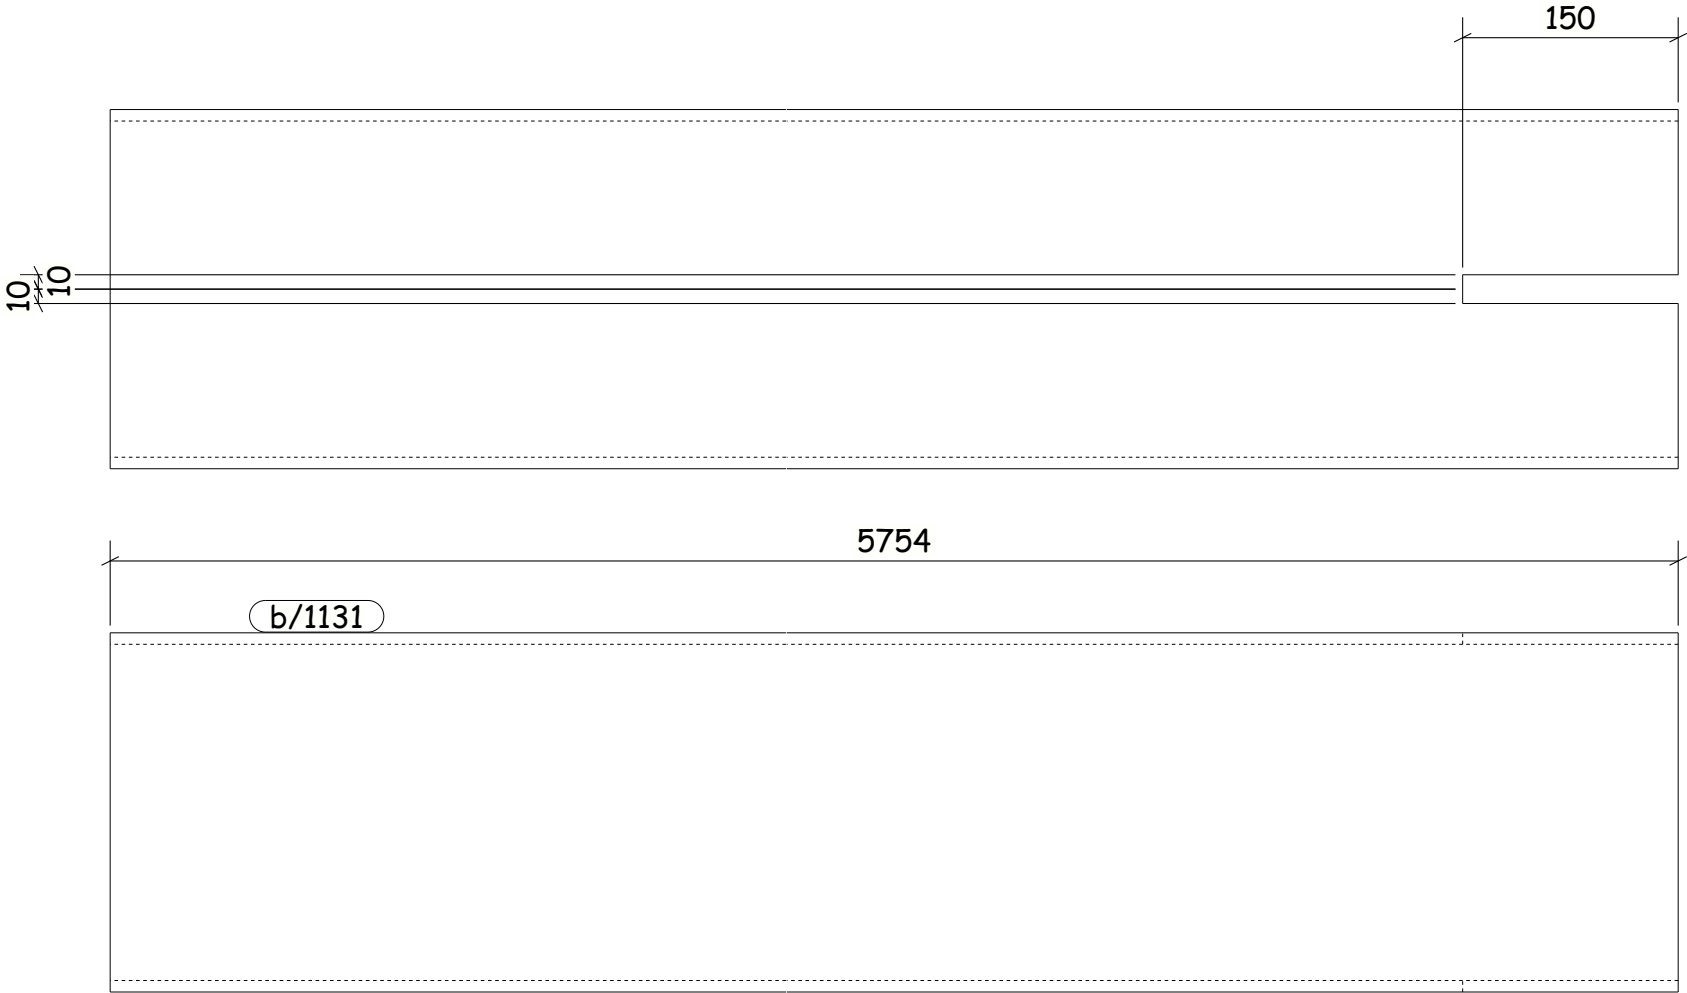

4 No DIAG

REQUIRED AS DRAWN MARKED b/***

LOT	0	QTY	4
PHASE	1	QTY	4

Rev	By	Date	Details				
b/1131	250*8		S235JR	4	5754.2	5.76	349.4
Mark	Profile		Grade	QTY	Length	Area	Weight

Fabricación: HcB Ingeniería

Project: CTIB 2026

General Notes:

ALL HOLES 22 Dia UNO

FINISH: 0

Steel Grade: S235JR

Drawn:

Checked:

Scale: N.T.S.

HcB CTIB

Job No. / Dwg No. / Rev

1 / b/1131 /

A4