


SHAFT DRAWING

| ALLOCATION TO ASSEMBLIES |       |
|--------------------------|-------|
| Assembly Mark            | TOTAL |
| A/8                      | 1     |
| B/30                     | 1     |
| C/2                      | 1     |
| C/74                     | 3     |
| Total                    | 6     |

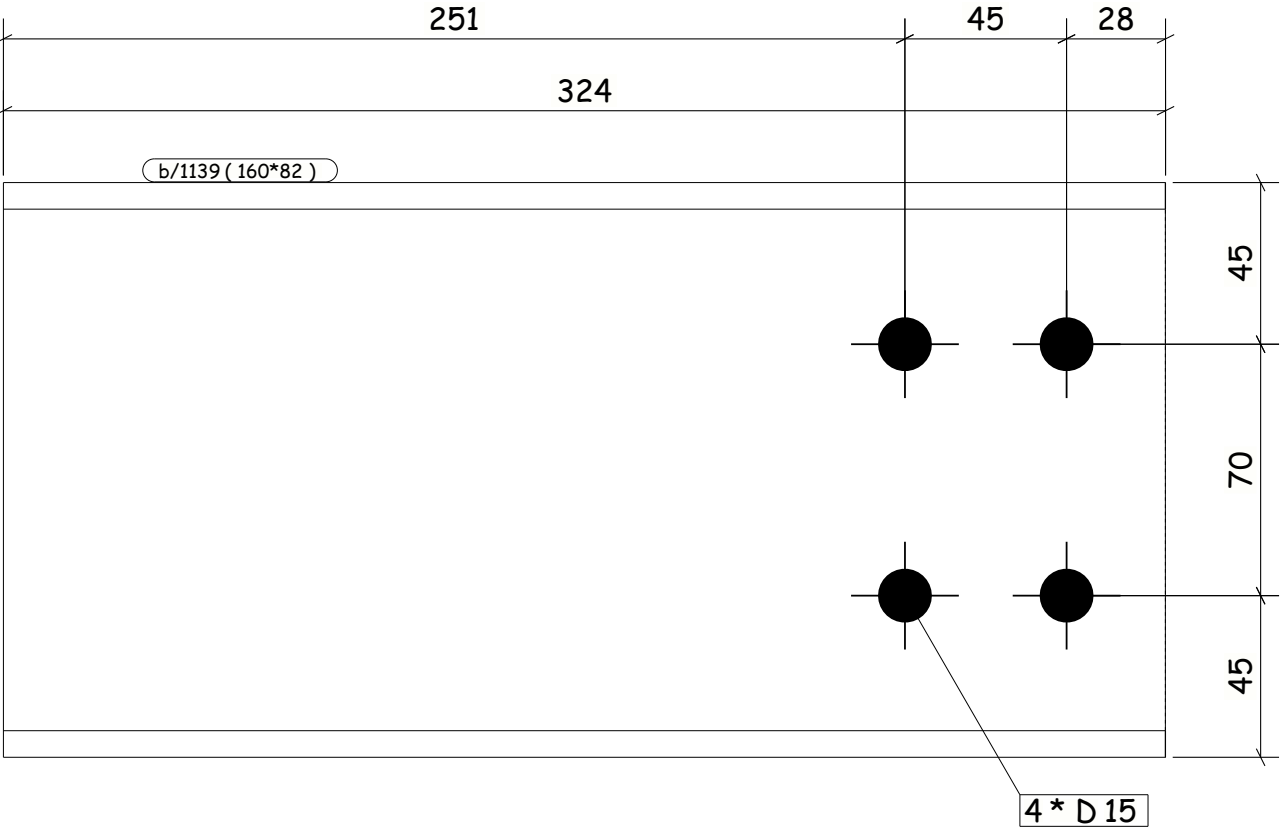

6 No BEAM                      REQUIRED AS DRAWN MARKED   b/\*\*\*

|       |   |     |   |
|-------|---|-----|---|
| LOT   | 0 | QTY | 6 |
| PHASE | 1 | QTY | 6 |

| Rev    | By | Date    | Details |     |        |      |        |
|--------|----|---------|---------|-----|--------|------|--------|
| b/1139 |    | IPE160  | S235JR  | 6   | 323.5  | 0.20 | 4.9    |
| Mark   |    | Profile | Grade   | QTY | Length | Area | Weight |

|                             |               |
|-----------------------------|---------------|
| Fabricación: HcB Ingeniería |               |
| Project: CTIB 2026          |               |
| General Notes:              | Drawn:        |
| ALL HOLES 22 Dia UNO        | Checked:      |
| FINISH: 0                   | Scale: N.T.S. |
| Steel Grade: S235JR         |               |



|           |           |     |    |
|-----------|-----------|-----|----|
| Job No. / | Dwg No. / | Rev | A4 |
| 1 /       | b/1139 /  |     |    |