


SHAFT DRAWING

ALLOCATION TO ASSEMBLIES	
Assembly Mark	TOTAL
B/1275	2
B/1287	2
Total	4

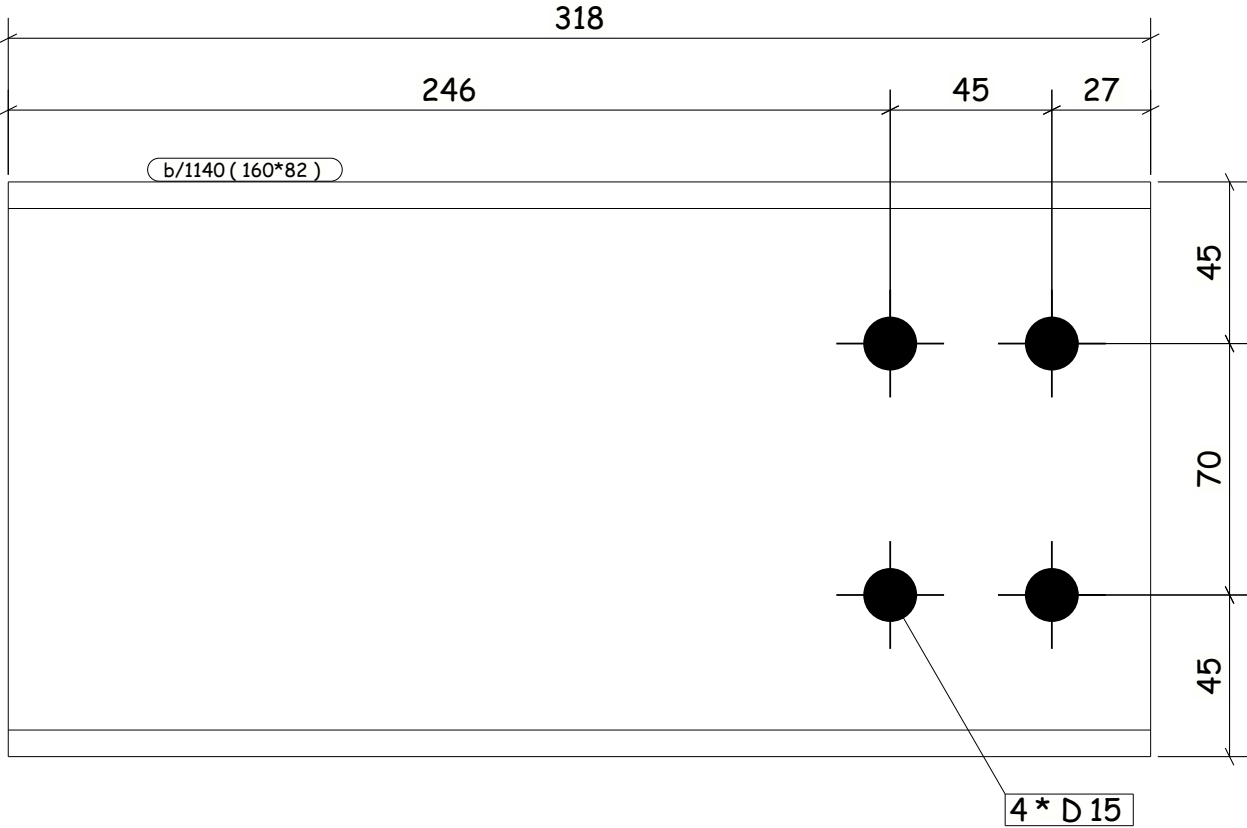

4 No BEAM REQUIRED AS DRAWN MARKED b/***

LOT	0	QTY	4
PHASE	1	QTY	4

Rev	By	Date	Details				
b/1140		IPE160	S235JR	4	318.0	0.20	4.8
Mark		Profile	Grade	QTY	Length	Area	Weight

Fabricación: HcB Ingeniería	
Project: CTIB 2026	
General Notes:	Drawn:
ALL HOLES 22 Dia UNO	Checked:
FINISH: 0	Scale: N.T.S.
Steel Grade: S235JR	



Job No. /	Dwg No. /	Rev	A4
1 /	b/1140 /		