


SHAFT DRAWING

ALLOCATION TO ASSEMBLIES	
Assembly Mark	TOTAL
B/236	8
Total	8

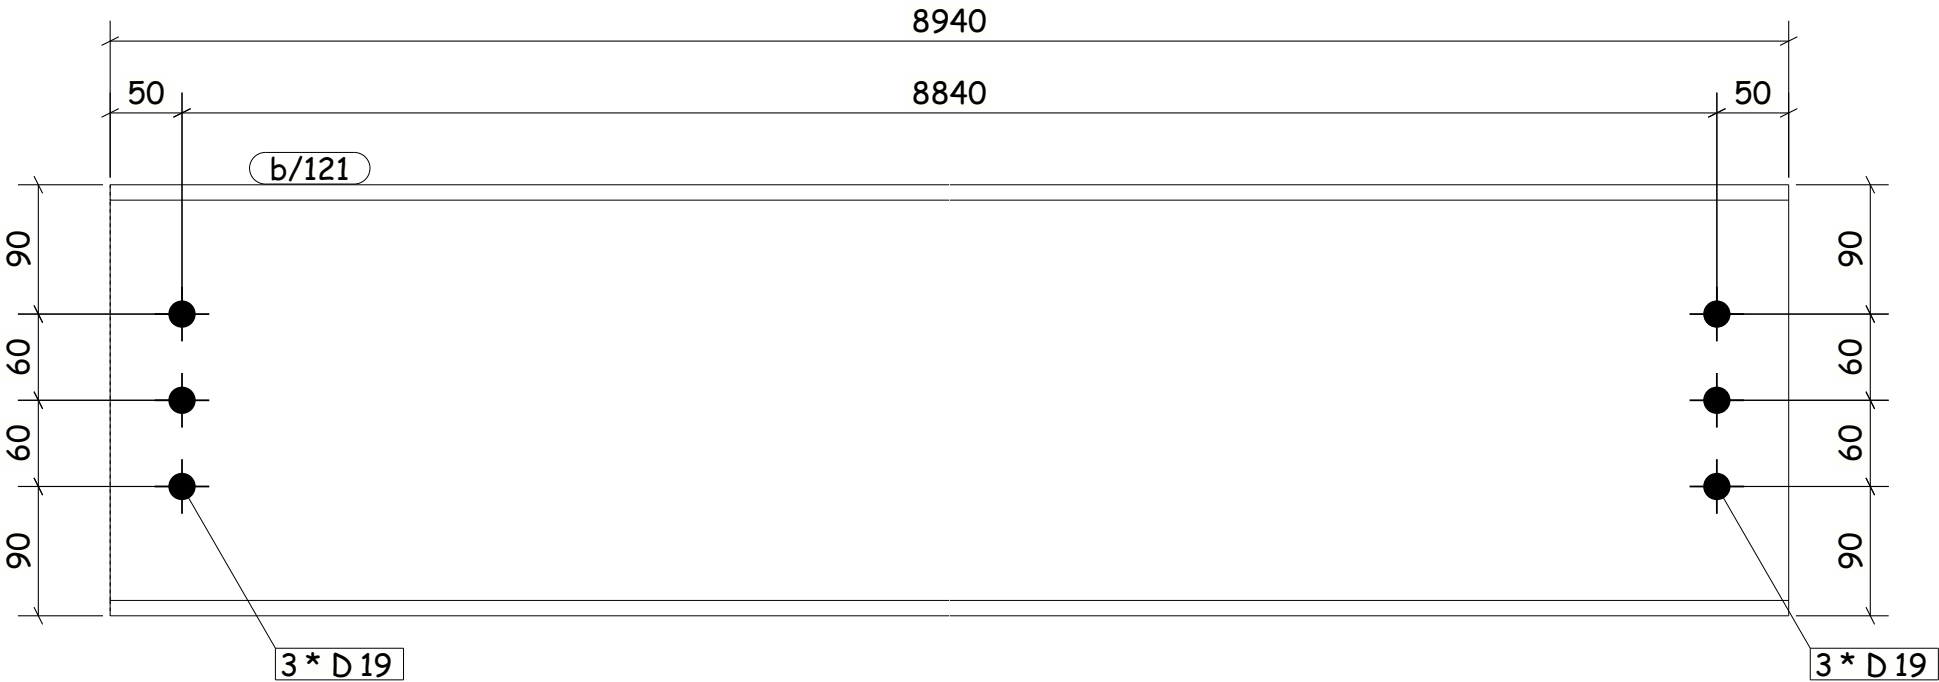

8 No BEAM

REQUIRED AS DRAWN MARKED b/121

LOT	0	QTY	8
PHASE	1	QTY	8

Rev	By	Date	Details				
b/121	IPE300		S235JR	8	8940.0	10.36	364.1
Mark	Profile		Grade	QTY	Length	Area	Weight

Fabricación: HcB Ingeniería

Project: CTIB 2026

General Notes:

ALL HOLES 22 Dia UNO

FINISH: 0

Steel Grade: S235JR

Drawn:

Checked:

Scale: N.T.S.

HcB CTIB

Job No. / Dwg No. / Rev

1 / b/121 /

A4