


SHAFT DRAWING

ALLOCATION TO ASSEMBLIES	
Assembly Mark	TOTAL
B/238	1
B/1276	1
Total	2

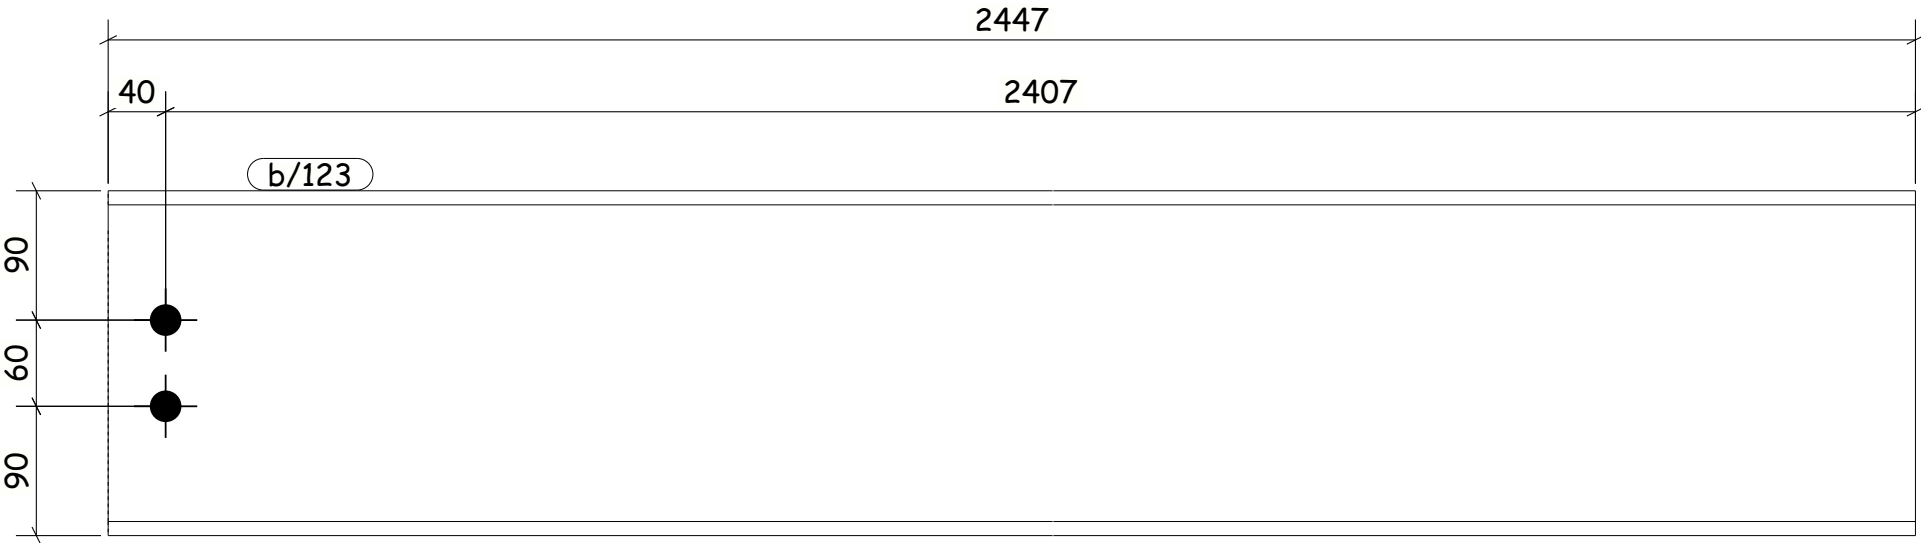

2 No BEAM

REQUIRED AS DRAWN MARKED b/123

LOT	0	QTY	2
PHASE	1	QTY	2

Rev	By	Date	Details				
b/123		IPE240	S235JR	2	2446.7	2.26	71.4
Mark		Profile	Grade	QTY	Length	Area	Weight

Fabricación: HcB Ingeniería					
Project: CTIB 2026					
General Notes:	Drawn:				
ALL HOLES 22 Dia UNO	Checked:	Job No. /	Dwg No. /	Rev	A4
FINISH: 0					
Steel Grade: S235JR	Scale: N.T.S.	1 /	b/123 /		