


SHAFT DRAWING

| ALLOCATION TO ASSEMBLIES |       |
|--------------------------|-------|
| Assem 75 Mark            | TOTAL |
| B/950                    | 1     |
| Total 720                | 1     |

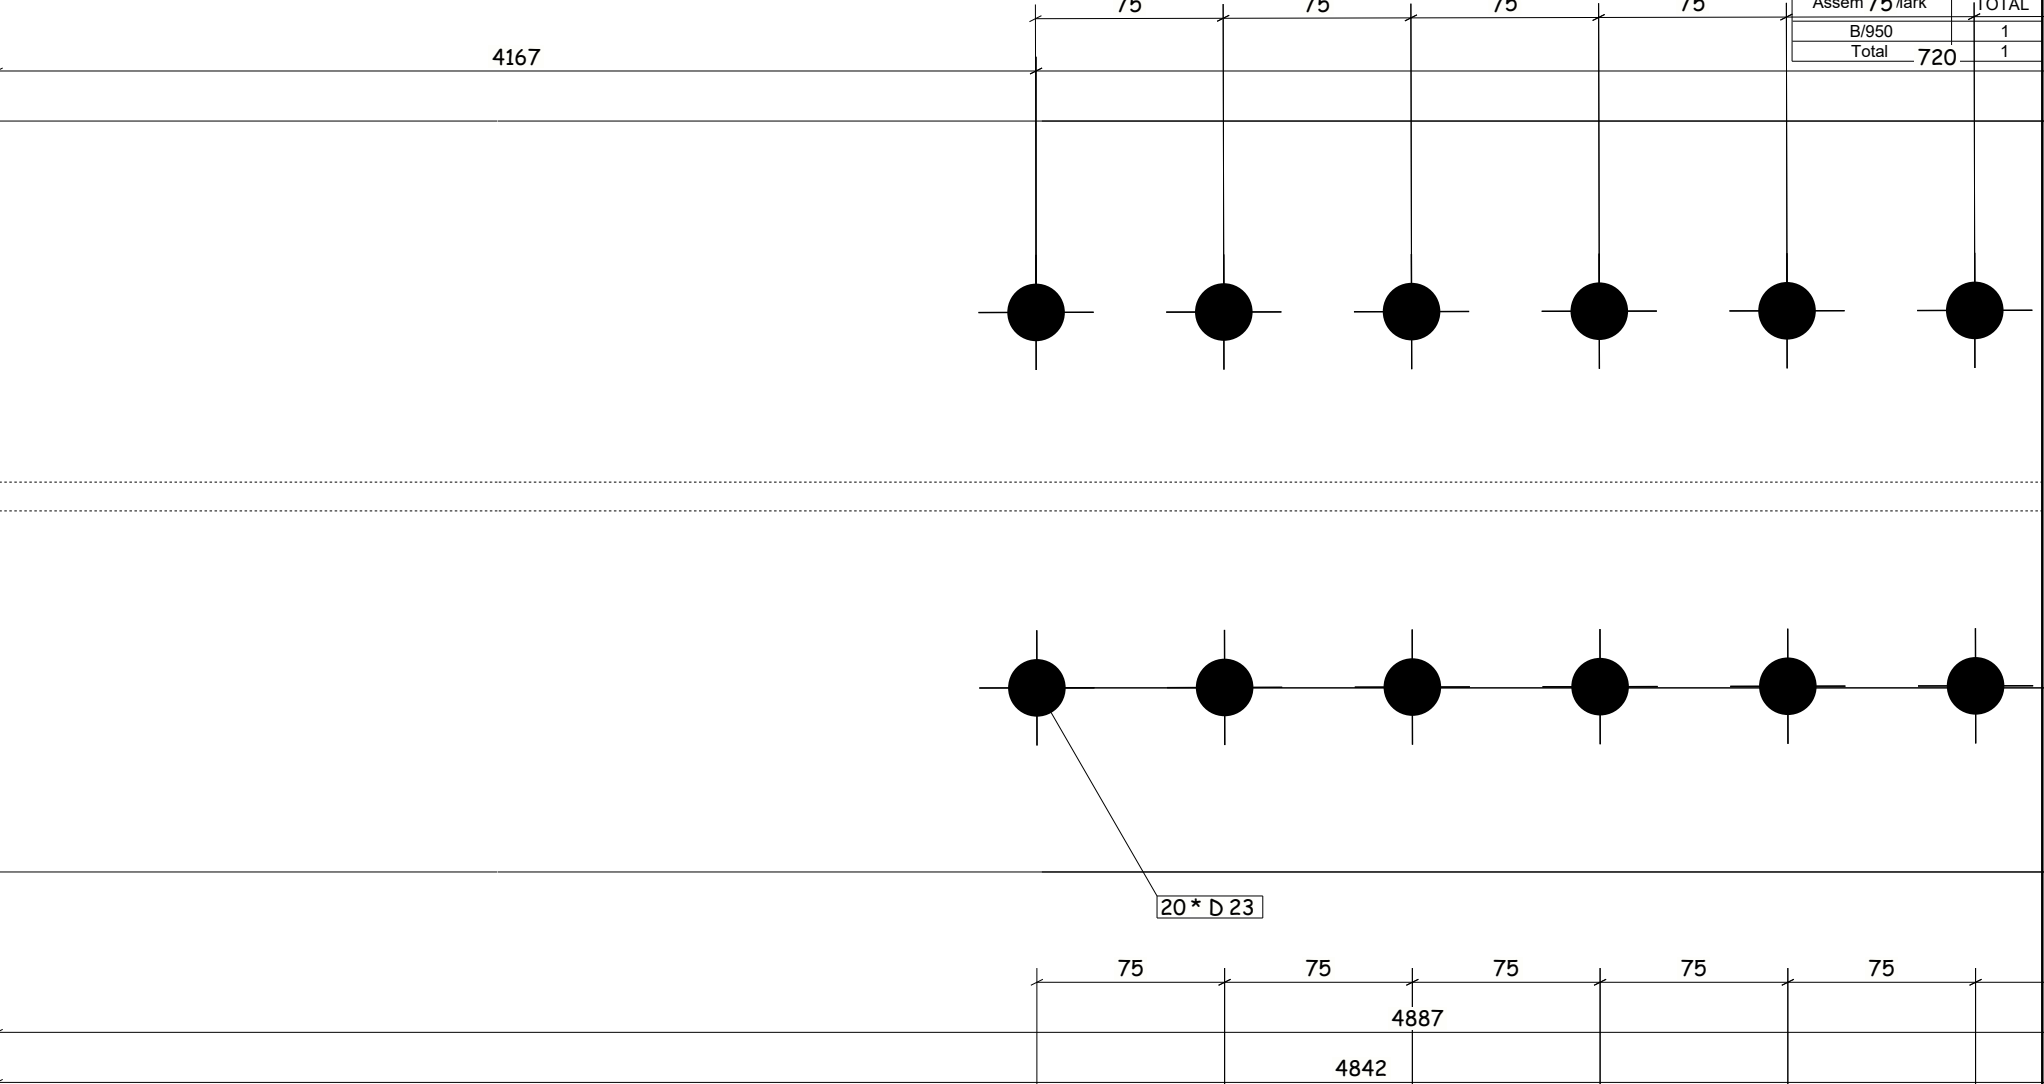

1 No BEAM

REQUIRED AS DRAWN MARKED b/127

|       |   |     |   |
|-------|---|-----|---|
| LOT   | 0 | QTY | 1 |
| PHASE | 1 | QTY | 1 |

|       |         |      |         |     |        |      |        |
|-------|---------|------|---------|-----|--------|------|--------|
|       |         |      |         |     |        |      |        |
|       |         |      |         |     |        |      |        |
|       |         |      |         |     |        |      |        |
| Rev   | By      | Date | Details |     |        |      |        |
| b/127 | HEA450  |      | S235JR  | 1   | 4887.1 | 9.83 | 659.0  |
| Mark  | Profile |      | Grade   | QTY | Length | Area | Weight |

Fabrication HcB Ingenieria

Project: CTIB 2026

General Notes:

ALL HOLES 22 Dia UNO

FINISH: 0

Steel Grade: S235JR

Drawn:

Checked:

Scale:

N.T.S.

HcB CTIB

Job No. / Dwg No. / Rev

1 / b/127 /