


SHAFT DRAWING

ALLOCATION TO ASSEMBLIES	
Assembly Mark	TOTAL
B/244	1
Total	1

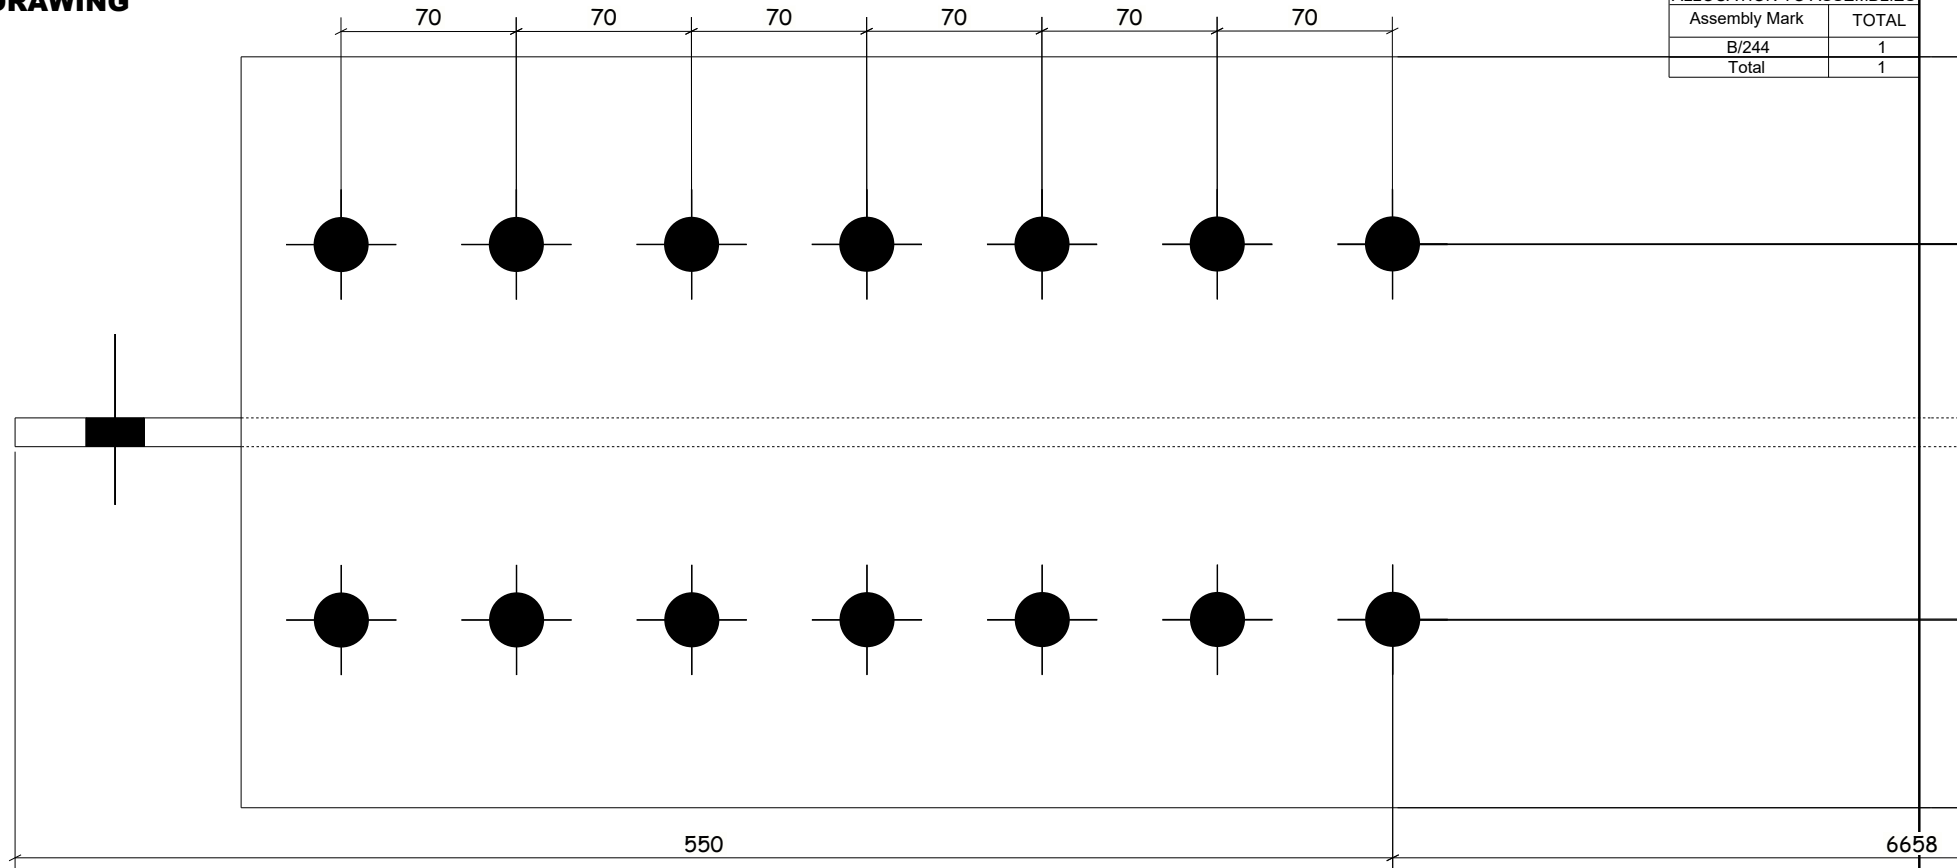

LOT	0	QTY	1
PHASE	1	QTY	1

Fabricación: HcB Ingeniería

Project:	CTIB 2026
-----------------	-----------

General Notes:		
ALL HOLES	22	Dia UNO

FINISH: 0
Steel Grade: S235JR

Drawn:

Checked:

Scale: N.T.S.

HcB CTIB

Job No. /	Dwg No. /	Rev
1 /	b/130 /	

Rev	By	Date	Details					
	b/130	HEA450	S235JR	1	7207.9	14.50	962.5	
	Mark	Profile	Grade	QTY	Length	Area	Weight	