
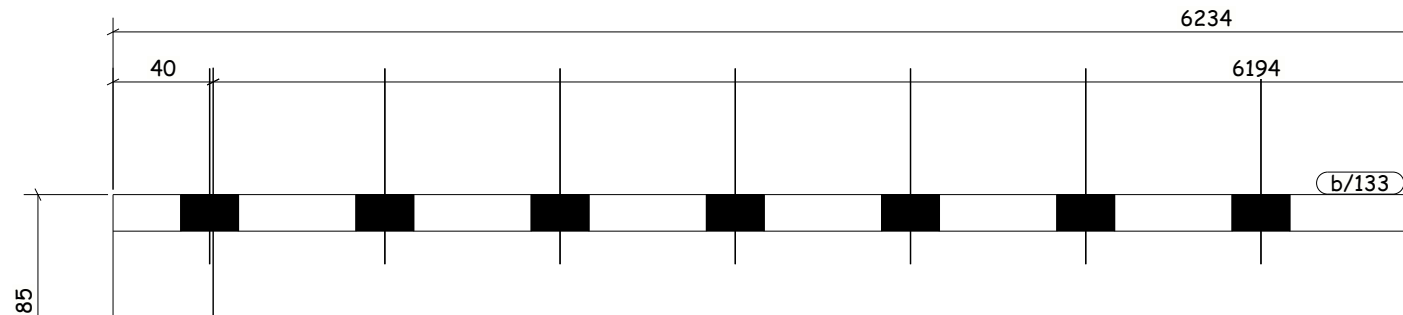


SHAFT DRAWING

ALLOCATION TO ASSEMBLIES	
Assembly Mark	TOTAL
B/247	1
Total	1

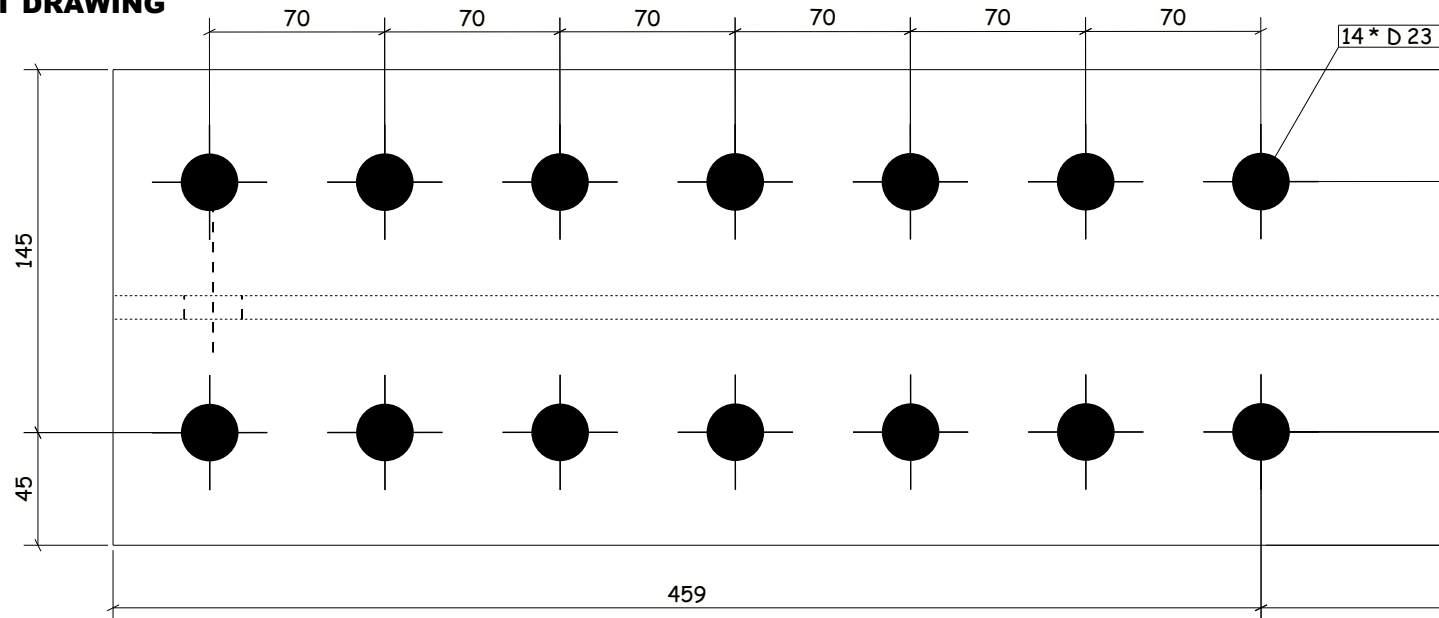

No	BEAM
----	------

REQUIRED AS DRAWN MARKED b/133

LOT	0	QTY	1
PHASE	1	QTY	1

Fabricación: HcB Ingeniería

Project:	CTIB 2026
-----------------	-----------

General Notes:

ALL HOLES 22 Dia UNO

FINISH: 0
Steel Grade: S235JR

Drawn:

Checked:

Scale: N.T.S.

HCB CTIB

Job No. / Dwg No. / Rev

1 / b/133 /

70								
	Rev	By	Date	Details				
	b/133		IPE450	S235JR	1	6233.9	10.01	465.1
	Mark		Profile	Grade	QTY	Length	Area	Weight