


SHAFT DRAWING

ALLOCATION TO ASSEMBLIES	
Assembly Mark	TOTAL
B/274	1
B/372	1
B/384	1
B/428	1
B/485	1
B/991	1
B/1023	1
B/1032	1
B/1065	1
B/1069	5
B/1088	1
B/1121	1
Total	16

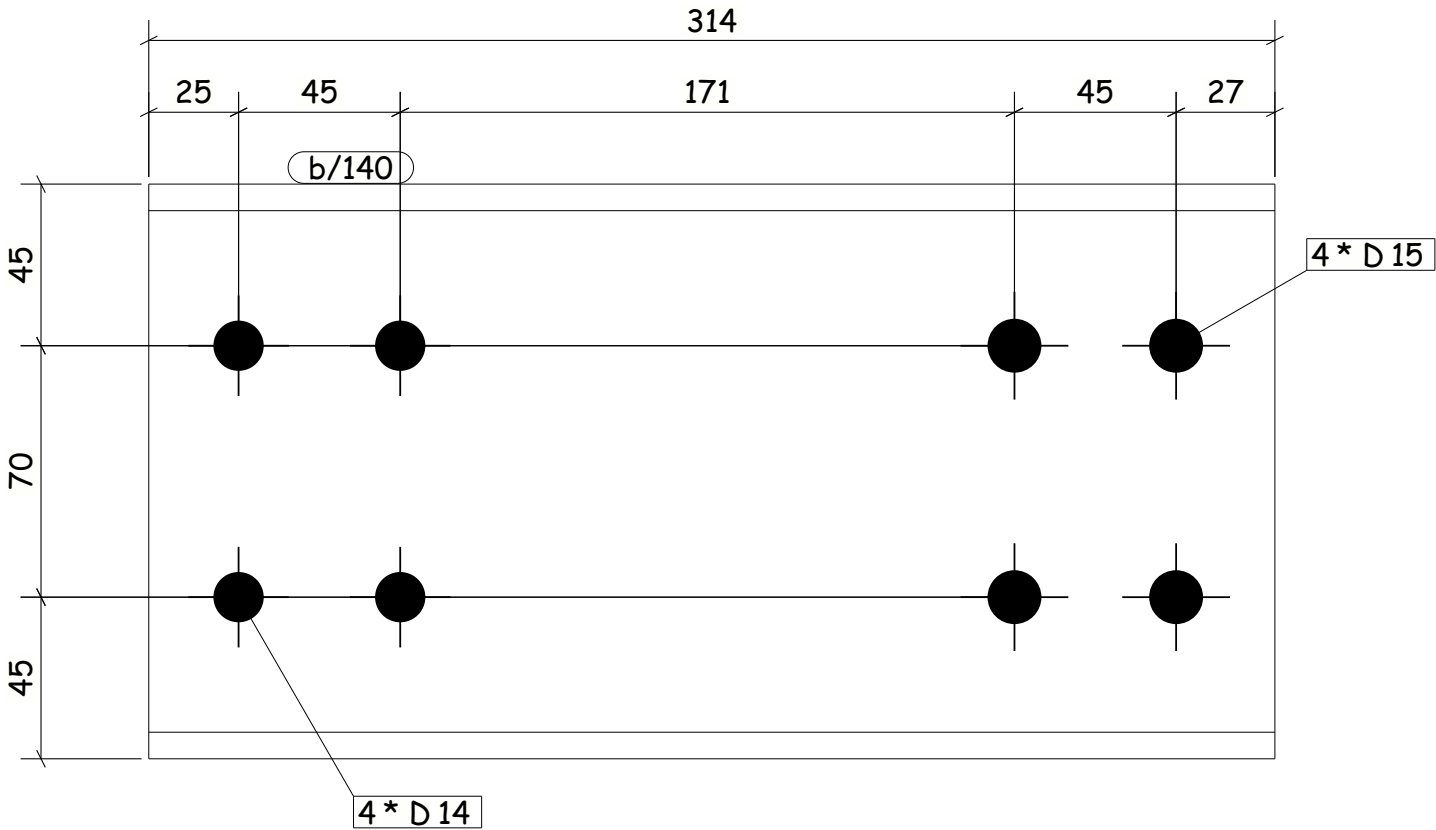

16 No BEAM REQUIRED AS DRAWN MARKED b/140

LOT	0	QTY	16
PHASE	1	QTY	16

Rev	By	Date	Details				
b/140		IPE160	S235JR	16	313.5	0.20	4.8
Mark		Profile	Grade	QTY	Length	Area	Weight

Fabricación: HcB Ingeniería		HcB CTIB				
Project: CTIB 2026						
General Notes:						Drawn:
ALL HOLES 22 Dia UNO		Checked:		Job No. / Dwg No. / Rev		A4
FINISH: 0						
Steel Grade: S235JR		Scale: N.T.S.		1 / b/140 /		