


SHAFT DRAWING

ALLOCATION TO ASSEMBLIES	
Assembly Mark	TOTAL
B/14	4
B/32	1
B/987	6
B/989	6
B/1061	6
B/1062	5
B/1063	2
C/2	3
Total	33

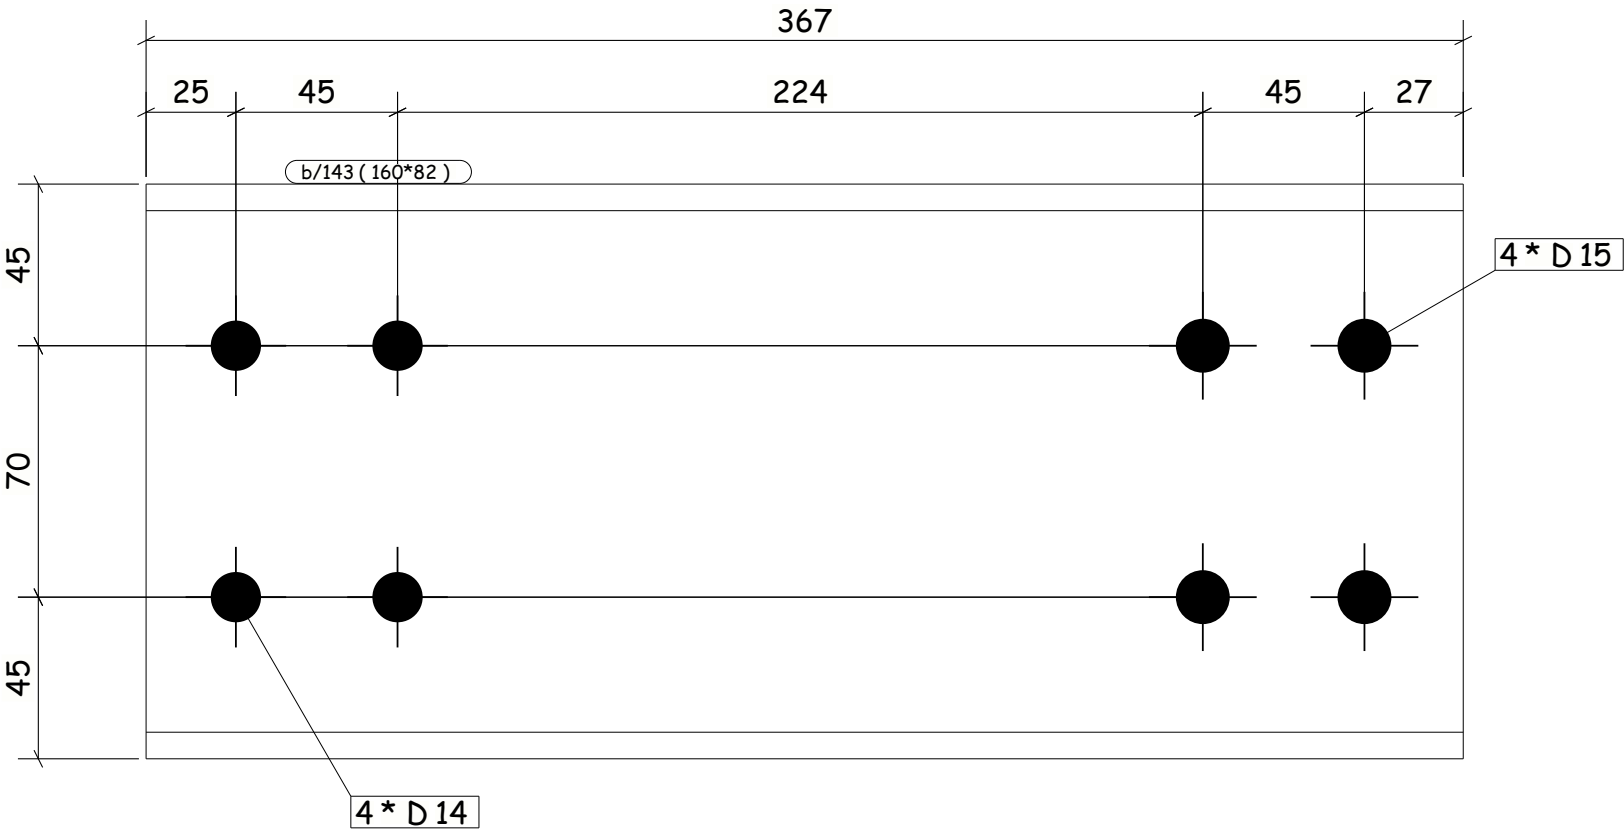

33 No BEAM REQUIRED AS DRAWN MARKED b/143

LOT	0	QTY	33
PHASE	1	QTY	33

Rev	By	Date	Details				
b/143	IPE160		S235JR	33	366.7	0.23	5.6
Mark	Profile		Grade	QTY	Length	Area	Weight

Fabricación: HcB Ingeniería	
Project: CTIB 2026	
General Notes:	Drawn:
ALL HOLES 22 Dia UNO	Checked:
FINISH: 0	Scale: N.T.S.
Steel Grade: S235JR	



Job No. /	Dwg No. /	Rev	A4
1 /	b/143 /		