


SHAFT DRAWING

ALLOCATION TO ASSEMBLIES	
Assembly Mark	TOTAL
B/30	3
B/35	3
B/37	3
B/52	3
B/274	3
B/370	3
B/372	2
B/384	3
B/385	3
B/428	4
B/485	4
B/989	1
B/991	6
B/994	3
B/1023	6
B/1024	3
B/1032	6
B/1033	3
B/1062	1
B/1065	3
B/1088	2
B/1115	1
B/1118	1
B/1121	3
B/1123	3
B/1159	3
B/1168	2
B/1170	3
B/1184	3
B/1269	2
B/1270	2
C/2	4
Total	95

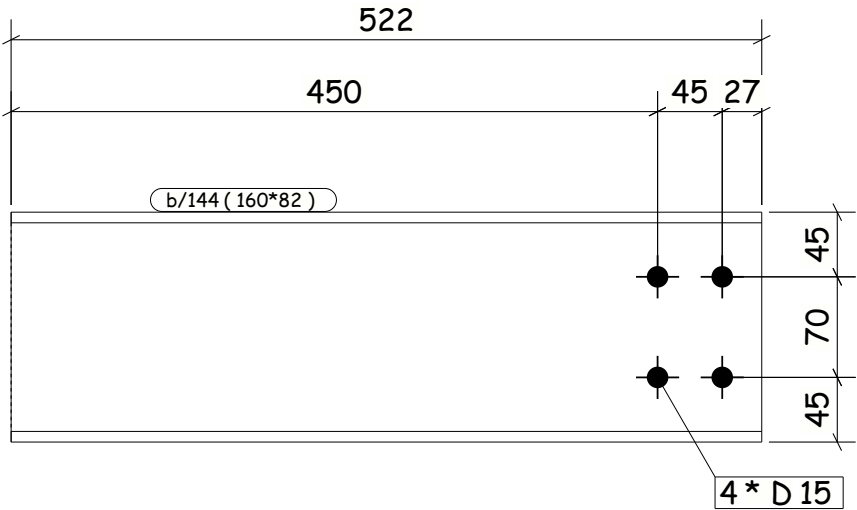

95 No BEAM REQUIRED AS DRAWN MARKED b/144

LOT	0	QTY	95
PHASE	1	QTY	95

Rev	By	Date	Details				
b/144		IPE160	S235JR	95	522.4	0.33	8.0
Mark		Profile	Grade	QTY	Length	Area	Weight

Fabricación: HcB Ingeniería	
Project: CTIB 2026	
General Notes:	Drawn:
ALL HOLES 22 Dia UNO	Checked:
FINISH: 0	Scale: N.T.S.
Steel Grade: S235JR	

HcB

CTIB

Job No. /

Dwg No. /

Rev

A4

1

/

b/144

/