


SHAFT DRAWING

ALLOCATION TO ASSEMBLIES	
Assembly Mark	TOTAL
B/14	1
B/1062	1
B/1063	1
B/1118	1
B/1120	1
B/1273	1
B/1274	2
Total	8

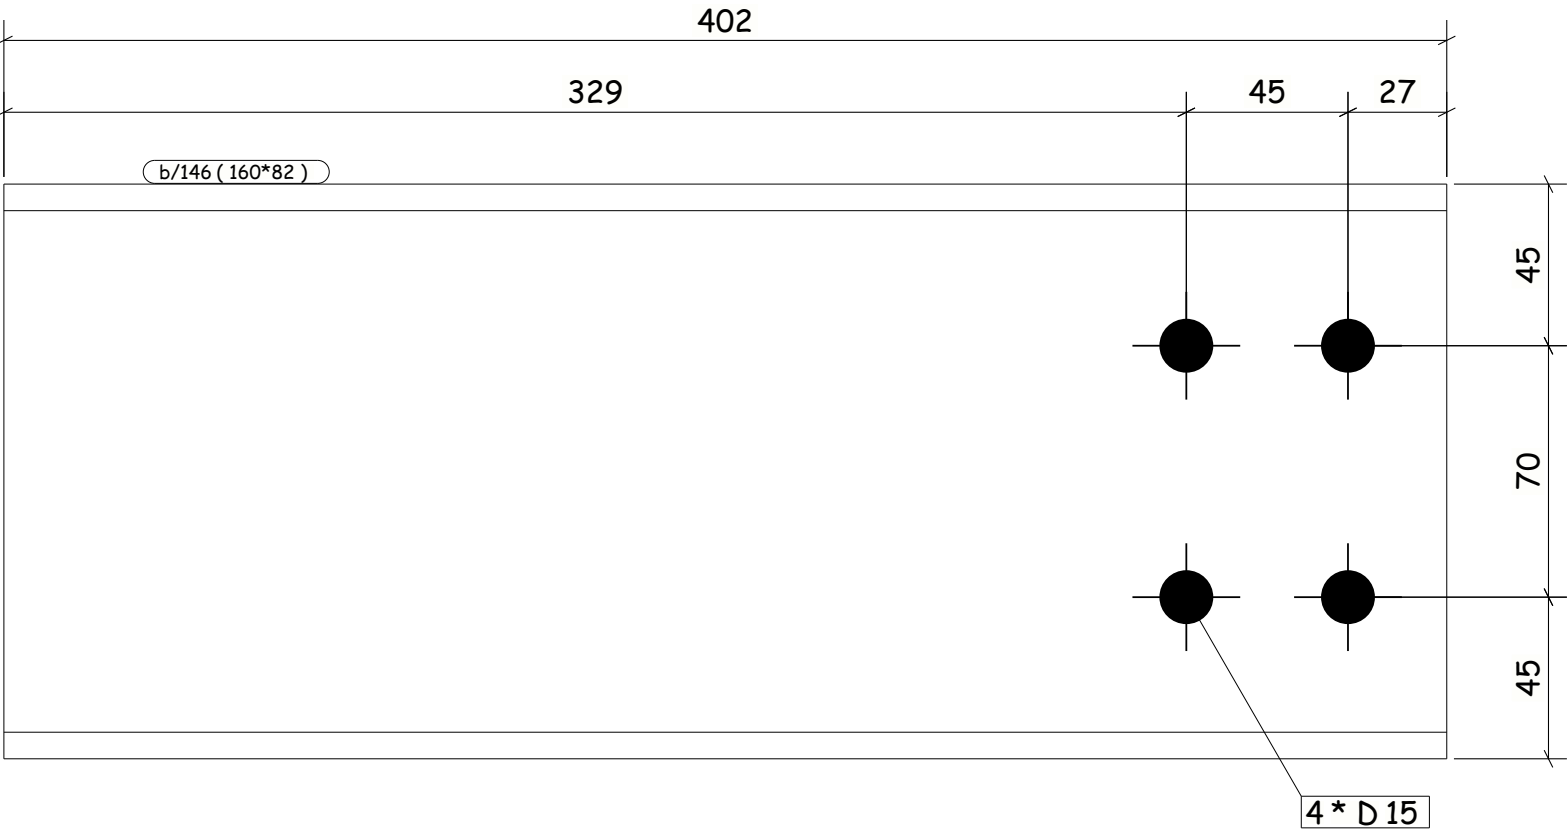

8 No BEAM

REQUIRED AS DRAWN MARKED b/146

LOT	0	QTY	8
PHASE	1	QTY	8

Rev	By	Date	Details				
b/146		IPE160	S235JR	8	401.7	0.25	6.1
Mark		Profile	Grade	QTY	Length	Area	Weight

Fabricación: HcB Ingeniería

Project: CTIB 2026

General Notes:

ALL HOLES 22 Dia UNO

FINISH: 0

Steel Grade: S235JR

Drawn:

Checked:

Scale: N.T.S.

HcB CTIB

Job No. / Dwg No. / Rev

1 / b/146 /

A4