


SHAFT DRAWING

ALLOCATION TO ASSEMBLIES	
Assembly Mark	TOTAL
B/372	1
B/986	3
B/1088	1
B/1176	1
Total	6

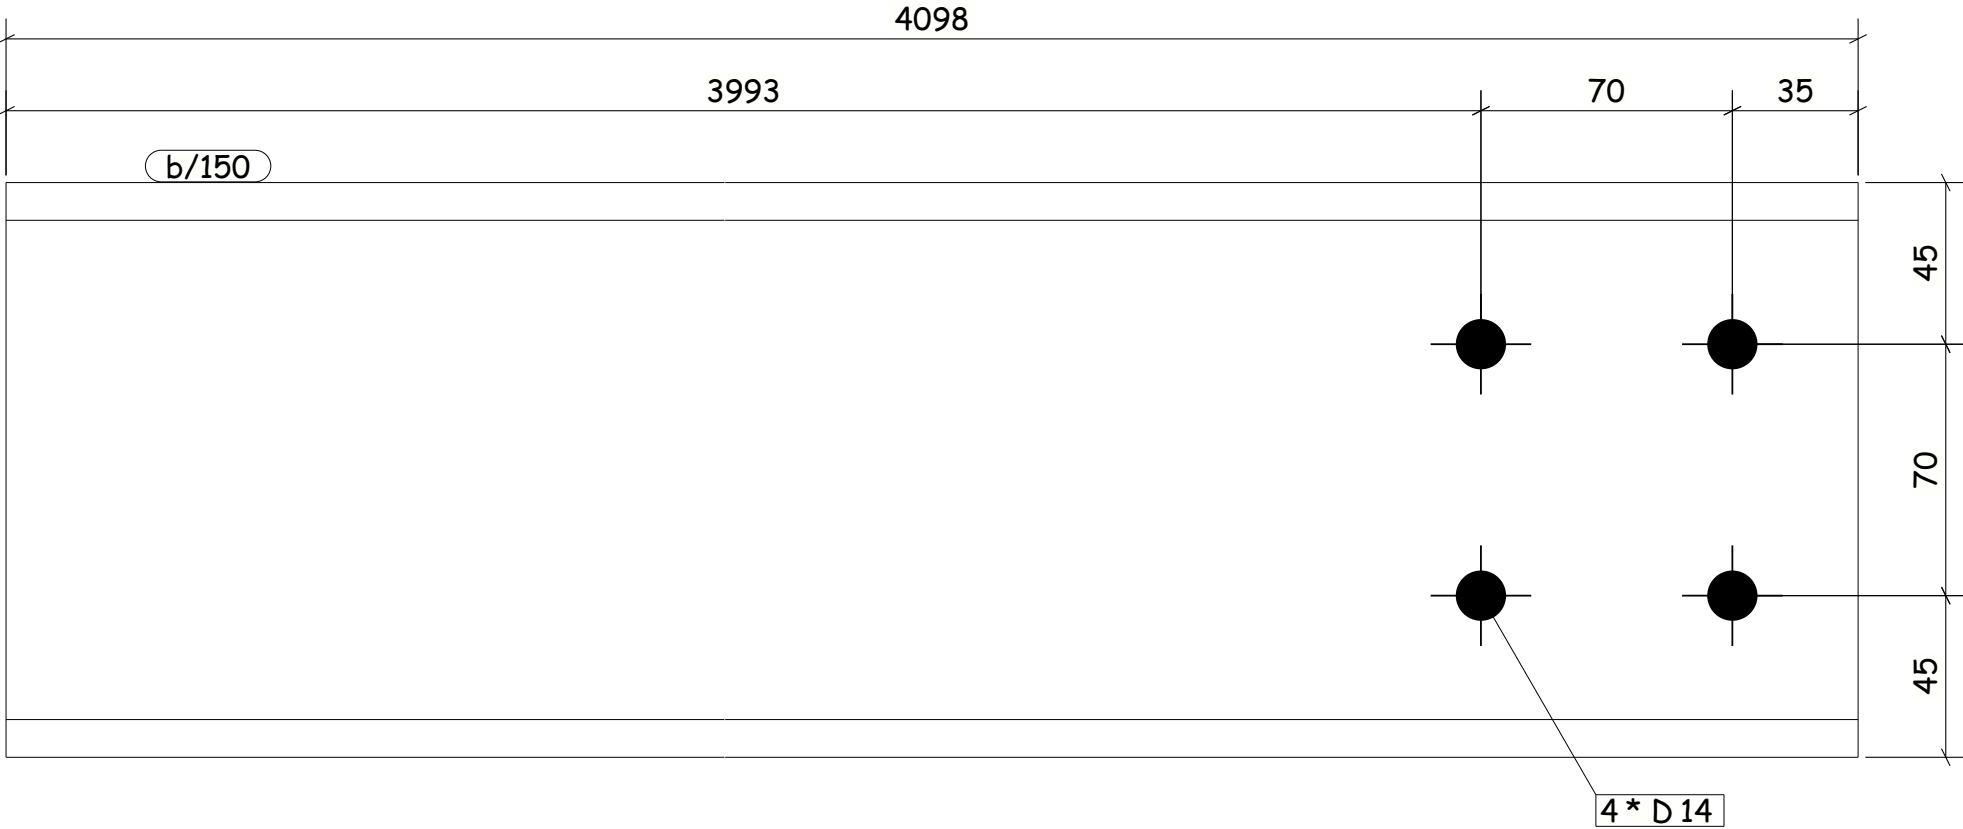

6 No BEAM

REQUIRED AS DRAWN MARKED b/150

LOT	0	QTY	6
PHASE	1	QTY	6

Rev	By	Date	Details				
b/150		UPN160	S235JR	6	4097.7	2.25	77.4
Mark		Profile	Grade	QTY	Length	Area	Weight

Fabricación: HcB Ingeniería

Project: CTIB 2026

General Notes:

ALL HOLES 22 Dia UNO

FINISH: 0

Steel Grade: S235JR

Drawn:

Checked:

Scale: N.T.S.

HcB CTIB

Job No. / Dwg No. / Rev

1 / b/150 /

A4