


SHAFT DRAWING

ALLOCATION TO ASSEMBLIES	
Assembly Mark	TOTAL
B/372	2
B/1088	2
B/1175	2
Total	6

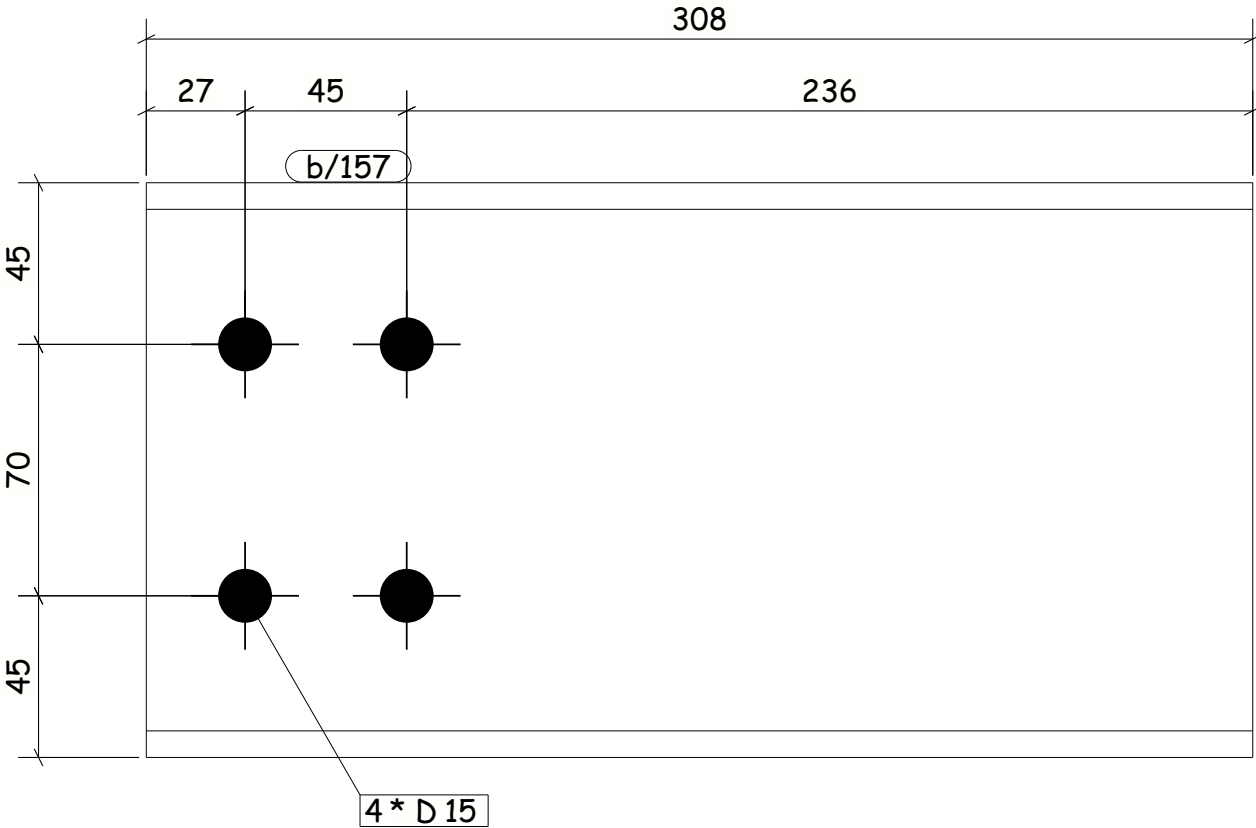

6 No BEAM

REQUIRED AS DRAWN MARKED b/157

LOT	0	QTY	6
PHASE	1	QTY	6

Rev	By	Date	Details				
b/157	IPE160		S235JR	6	308.0	0.19	4.7
Mark	Profile		Grade	QTY	Length	Area	Weight

Fabricación: HcB Ingeniería

Project: CTIB 2026

General Notes:

ALL HOLES 22 Dia UNO

FINISH: 0

Steel Grade: S235JR

Drawn:

Checked:

Scale: N.T.S.

HcB CTIB

Job No. / Dwg No. / Rev

1 / b/157 /

A4