


SHAFT DRAWING

ALLOCATION TO ASSEMBLIES	
Assembly Mark	TOTAL
B/1086	2
B/1165	3
B/1171	1
B/1172	3
B/1173	3
Total	12

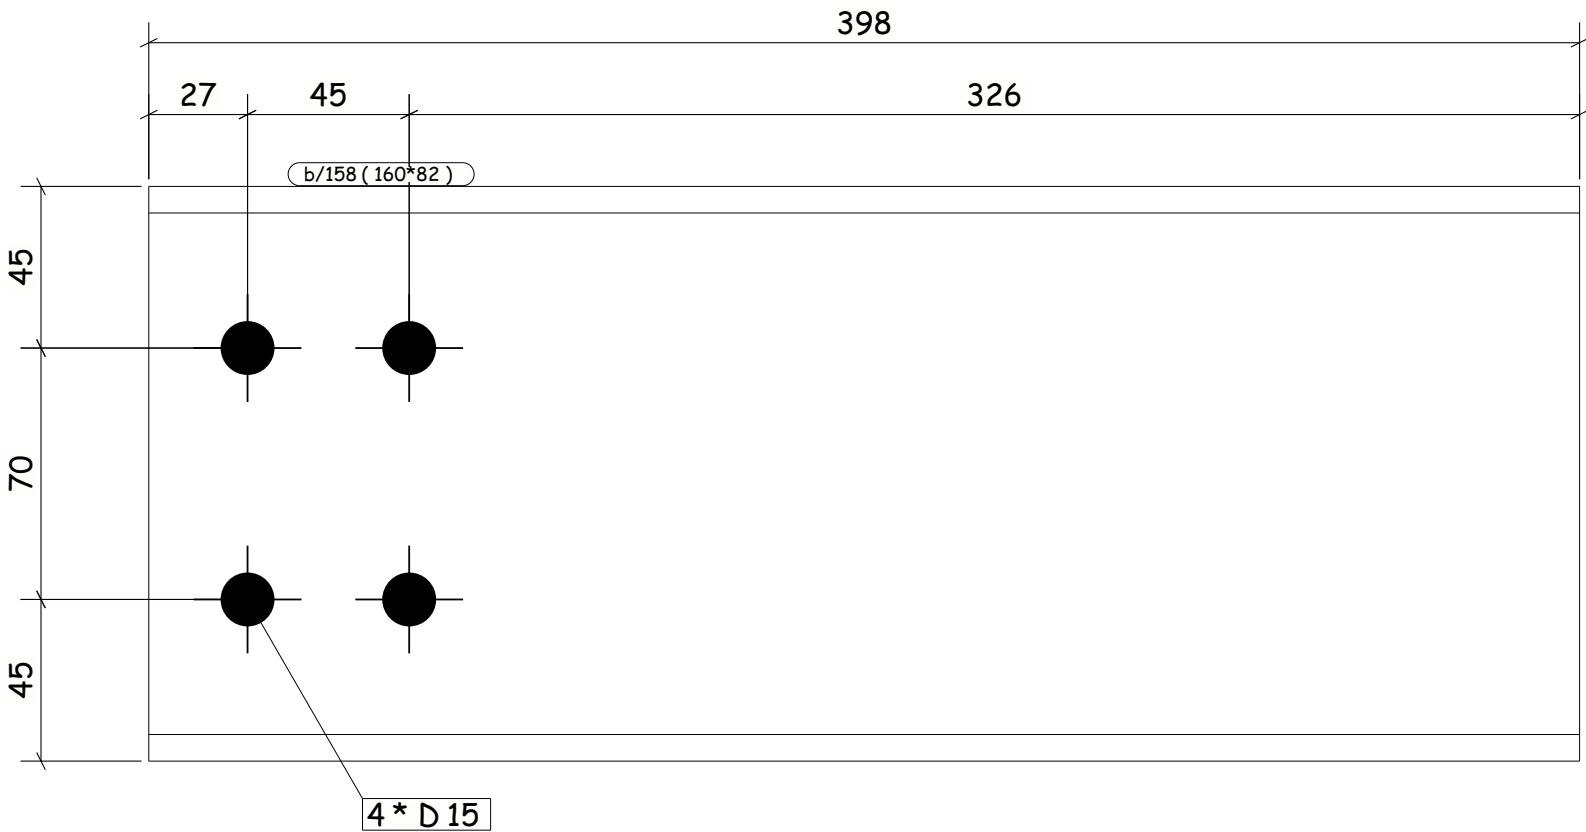

12 No BEAM

REQUIRED AS DRAWN MARKED b/158

LOT	0	QTY	12
PHASE	1	QTY	12

Rev	By	Date	Details				
b/158		IPE160	S235JR	12	398.3	0.25	6.1
Mark		Profile	Grade	QTY	Length	Area	Weight

Fabricación: HcB Ingeniería		HcB CTIB	
Project: CTIB 2026			
General Notes: ALL HOLES 22 Dia UNO FINISH: 0 Steel Grade: S235JR	Drawn:	Job No. / Dwg No. / Rev 1 / b/158 /	
	Checked:		
	Scale: N.T.S.		