


SHAFT DRAWING

ALLOCATION TO ASSEMBLIES	
Assembly Mark	TOTAL
C/22	3
Total	3

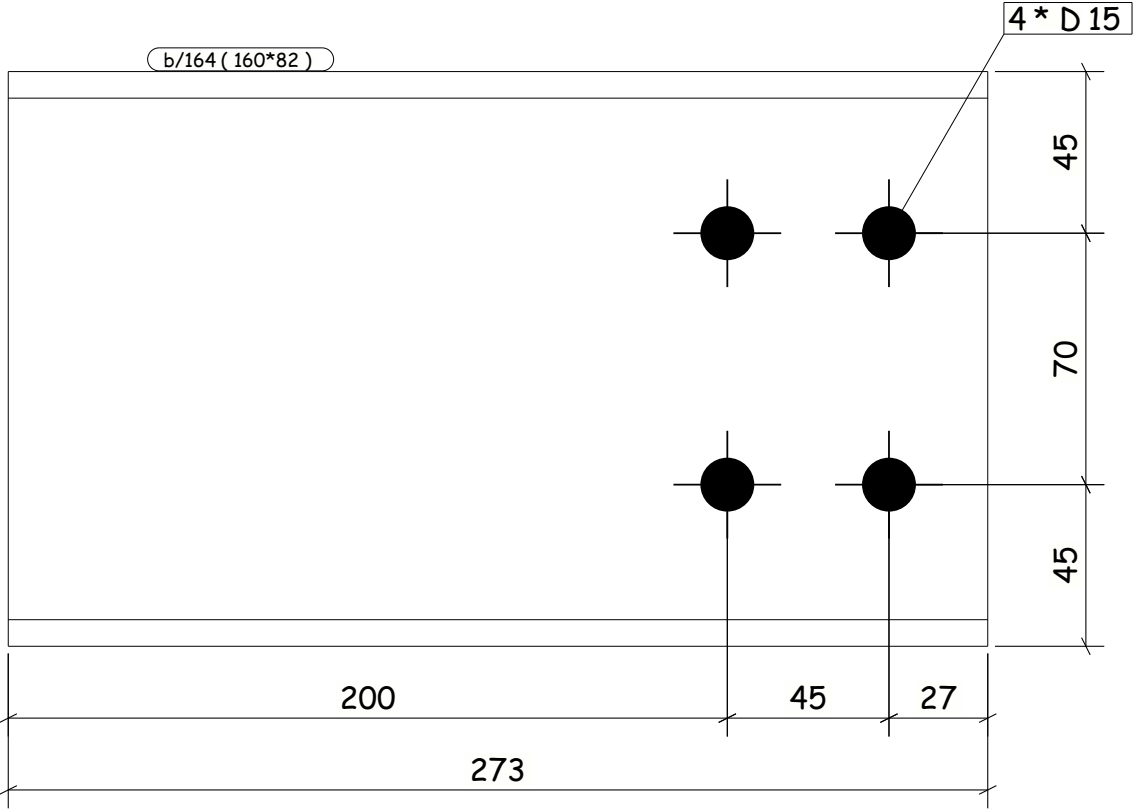

3 No BEAM REQUIRED AS DRAWN MARKED b/164

LOT	0	QTY	3
PHASE	1	QTY	3

Rev	By	Date	Details				
b/164		IPE160	S235JR	3	272.7	0.17	4.2
Mark		Profile	Grade	QTY	Length	Area	Weight

Fabricación: HcB Ingeniería	
Project: CTIB 2026	
General Notes:	Drawn:
ALL HOLES 22 Dia UNO	Checked:
FINISH: 0	Scale: N.T.S.
Steel Grade: S235JR	



Job No. /	Dwg No. /	Rev	A4
1 /	b/164 /		