


SHAFT DRAWING

ALLOCATION TO ASSEMBLIES		
Assembly Mark	75	TOTAL
B/44		1
Total		1

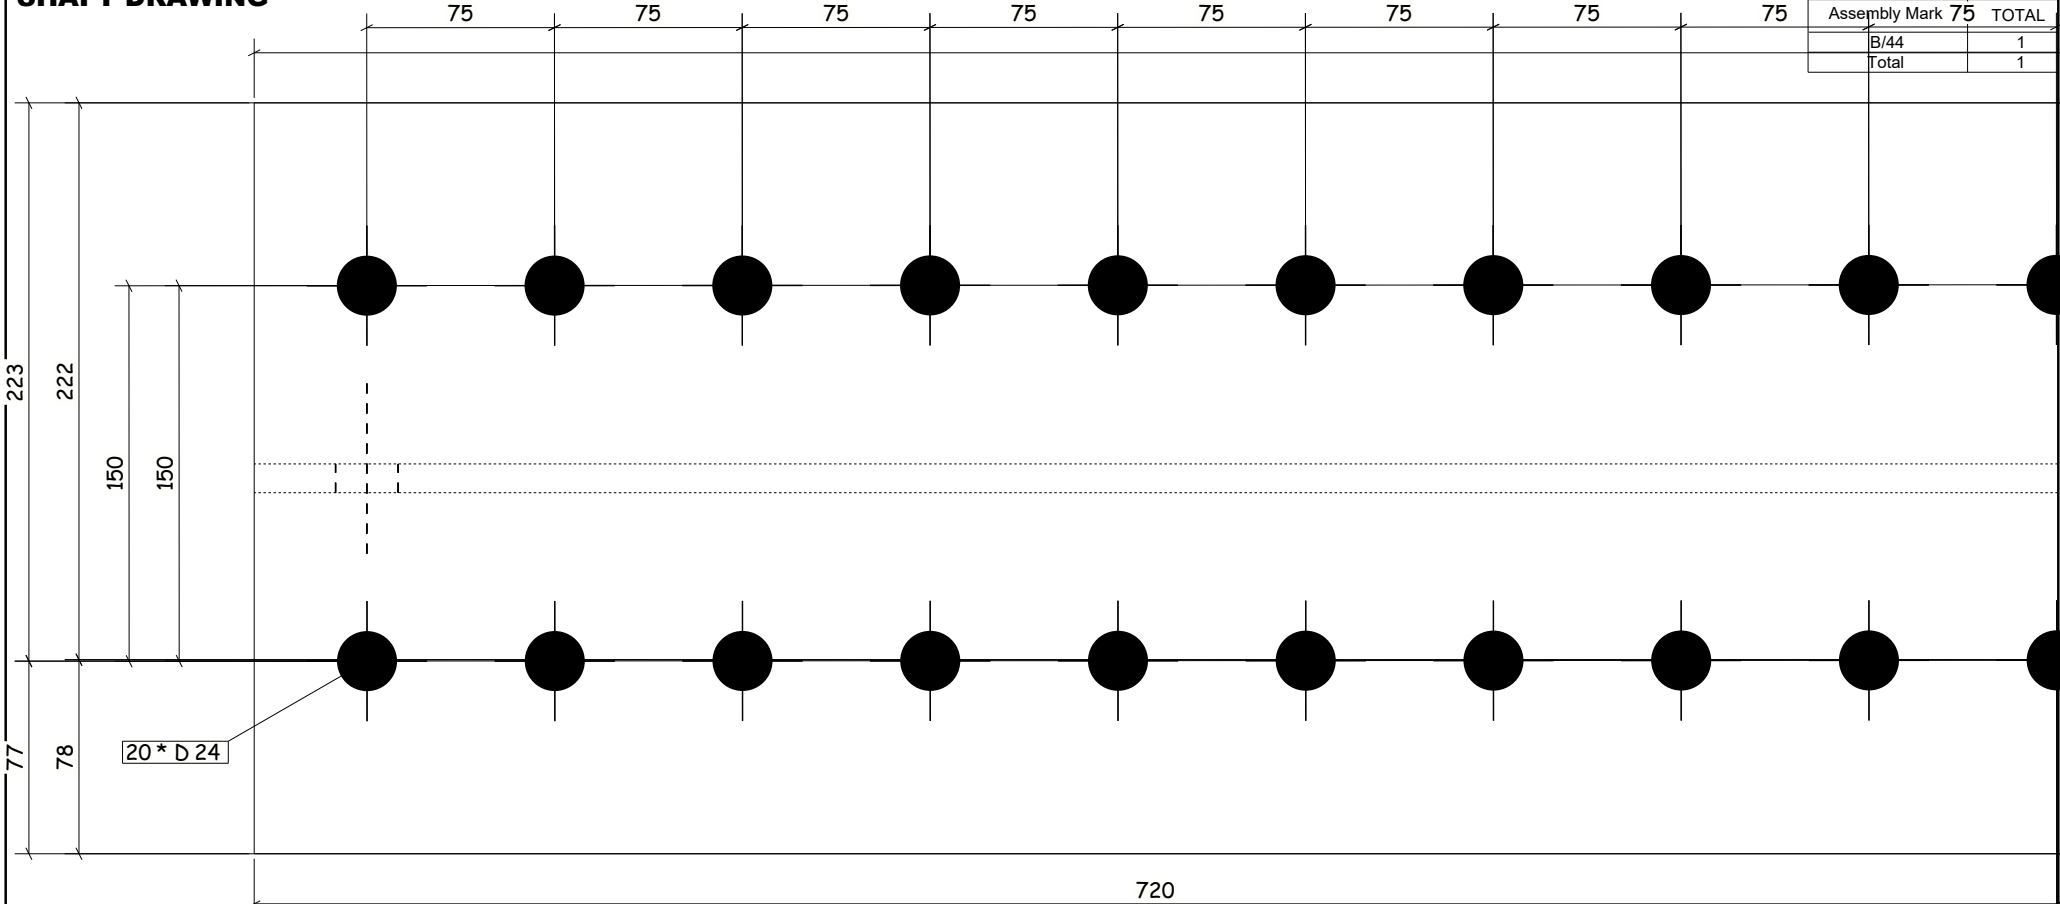

1 No BEAM

REQUIRED AS DRAWN MARKED b/22

b/22	0	QTY	1
PHASE	1		1

Fabricación: HcB Ingeniería

Project: 2026

General Notes:

ALL HOLES 22 Dia UNO

FINISH: 0

Steel Grade: S235JR

Drawn:

Checked:

Scale: N.T.S.

HcB STIB

Job No. / Dwg No. / Rev

1 / b/22 /