
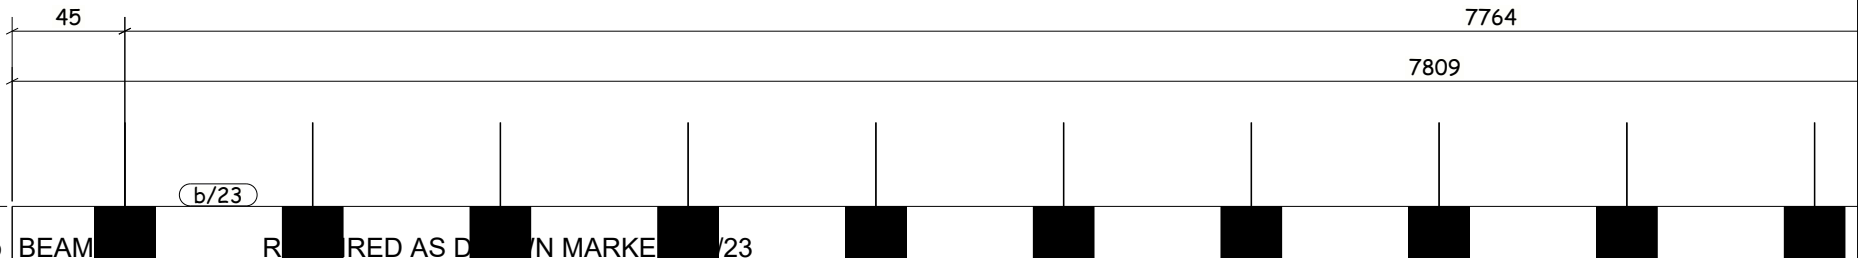


SHAFT DRAWING

ALLOCATION TO ASSEMBLIES	
Assembly 75κ	TOTAL
B/45	1
Total	1

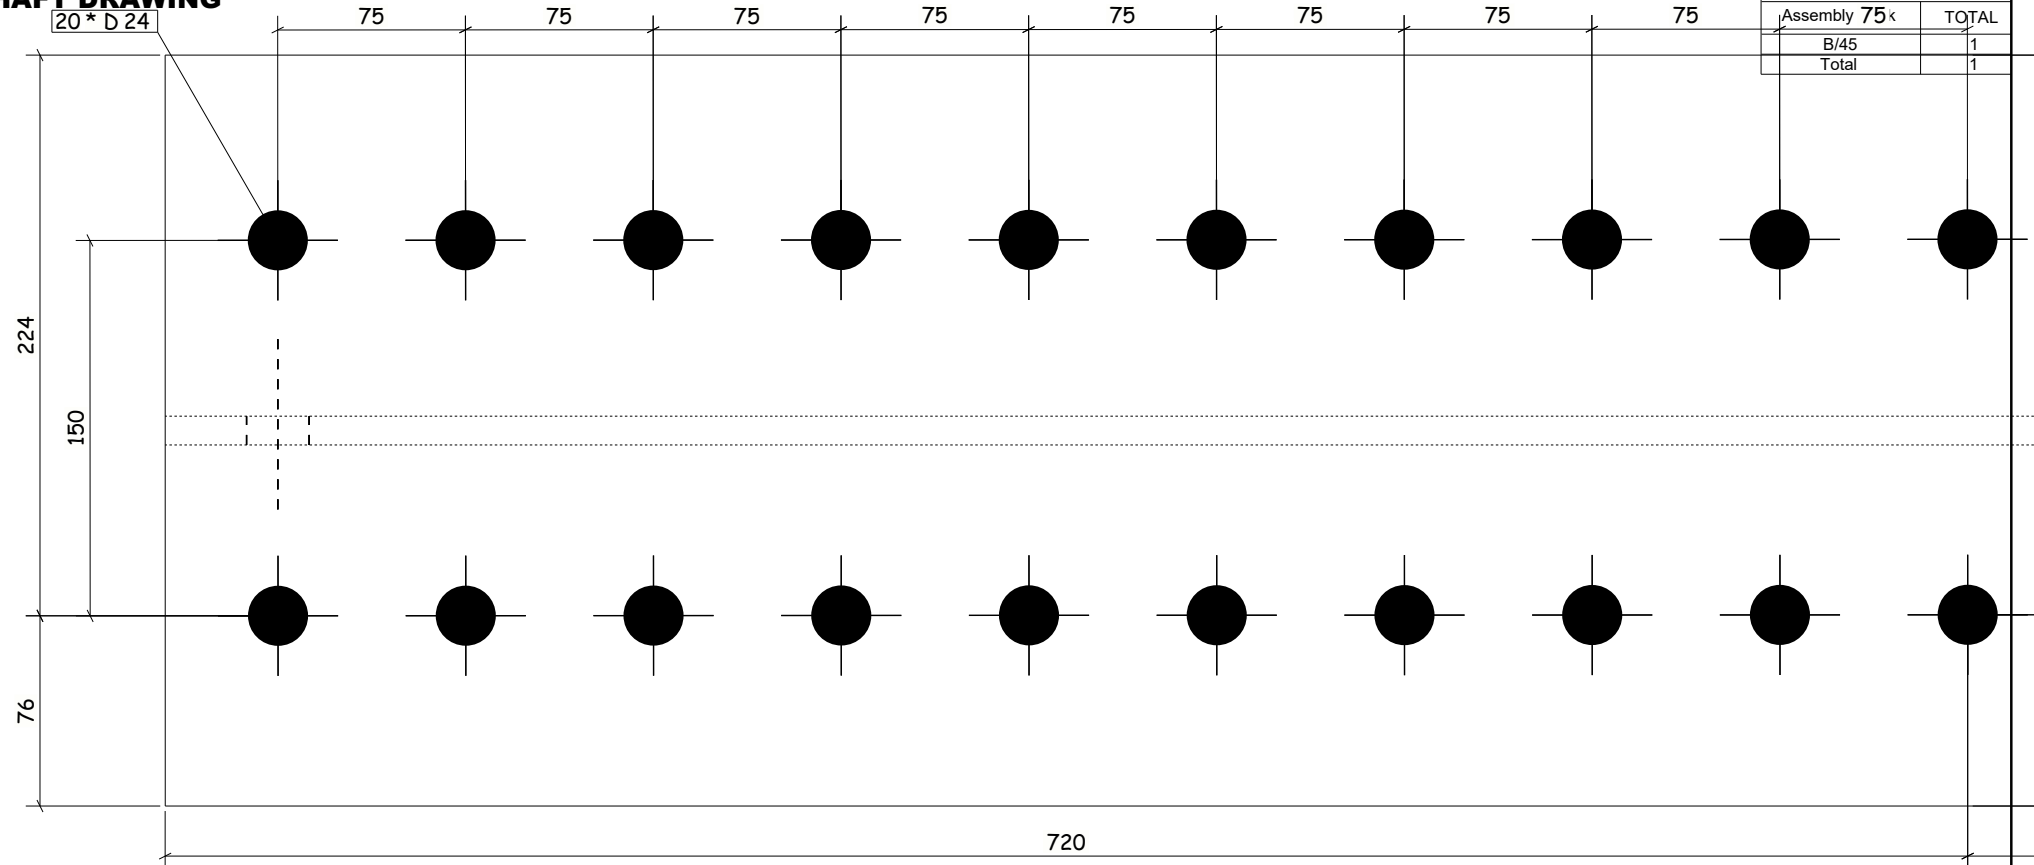

LOT	0	QTY	1
PHASE	1	QTY	1

Fabricación: HcB Ingeniería

Project: CTIB 2026

General Notes:

ALL HOLES 22 Dia UNO

FINISH: 0

Steel Grade: S235JR

Drawn:

Checked:

Scale: N.T.S.

HcB CTIB

Job No. / Dwg No. / Rev

1 / b/23 /

Rev	By	Date	Details				
b/23		A450	S235JR	1	7808.7	15.70	1052.9
Mark		Profile	Grade	QTY	Length	Area	Weight