


SHAFT DRAWING

ALLOCATION TO ASSEMBLIES	
Assembly Mark	TOTAL
B/1168	1
B/1179	1
Total	2

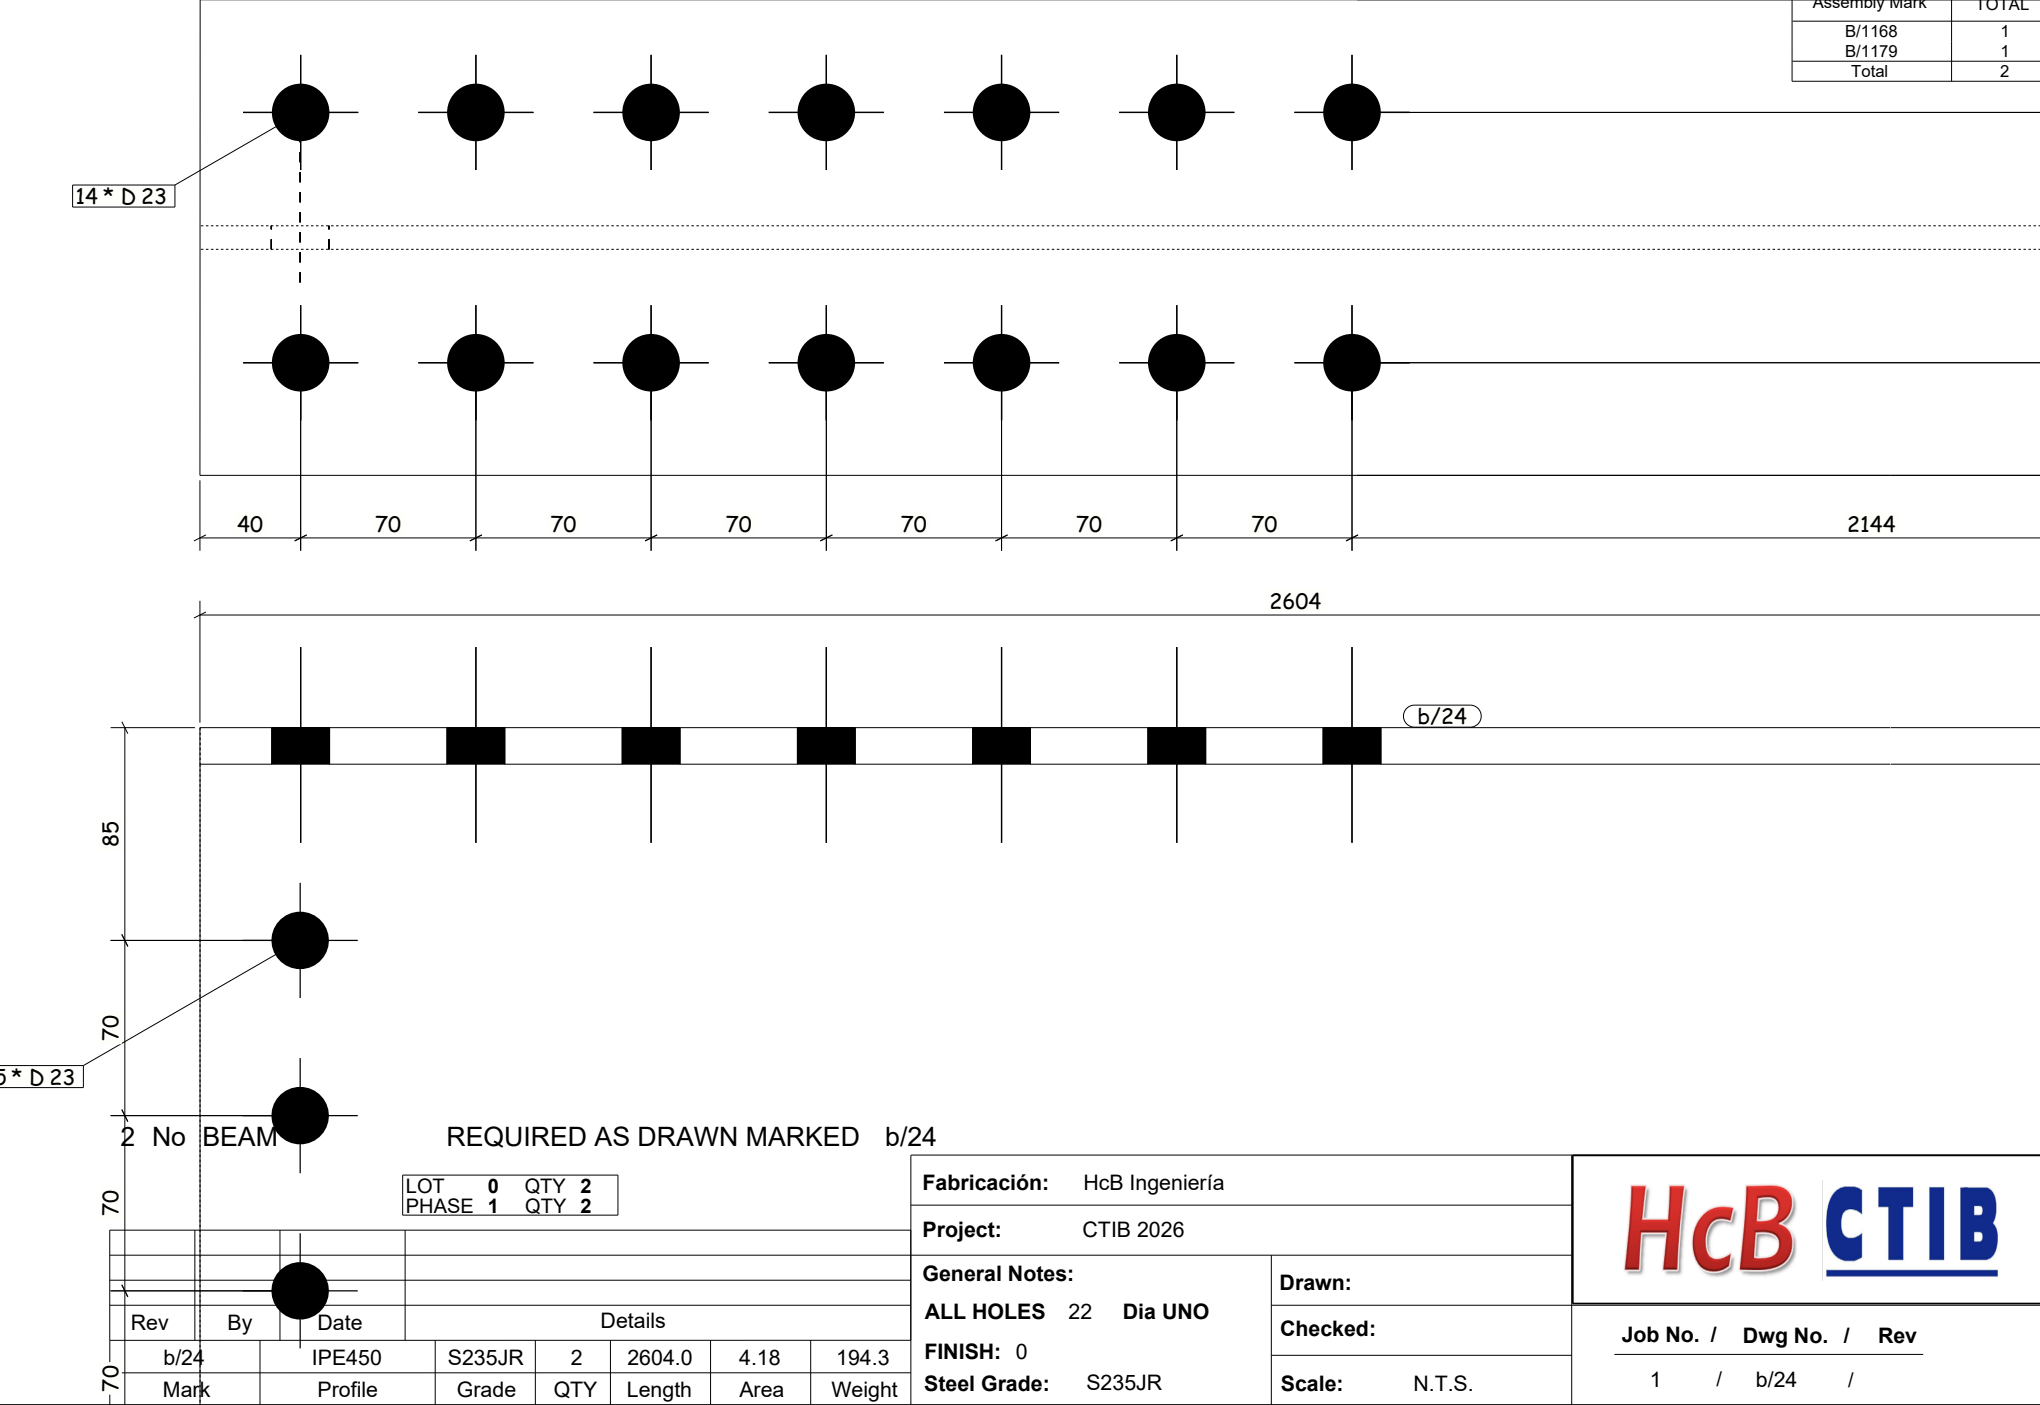

Fabricación: HcB Ingenieria

Project: CTIB 2026

General Notes:
ALL HOLES 22 Dia UNO

FINISH: 0
Steel Grade: S235JR

Drawn:

Checked:

Scale: N.T.S.

HcB CTIB

Job No. / Dwg No. / Rev

1 / b/24 /