
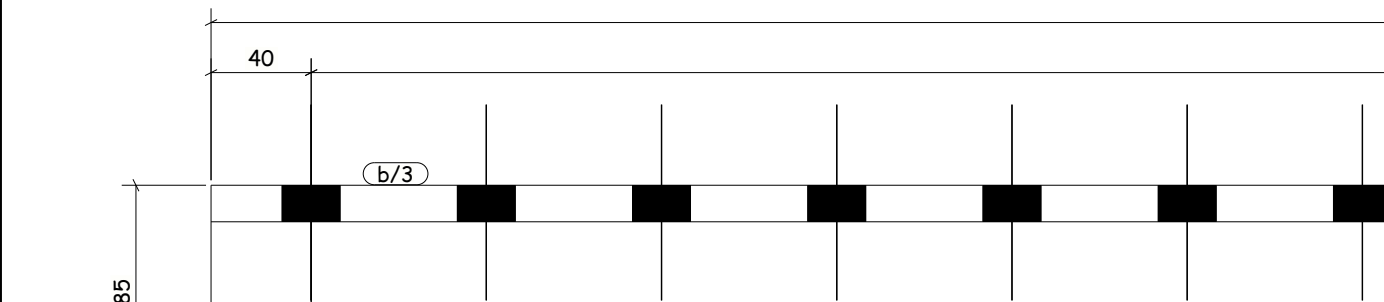


SHAFT DRAWING

ALLOCATION TO ASSEMBLIES	
Assembly Mark	TOTAL
B/35	1
B/52	1
Total	2

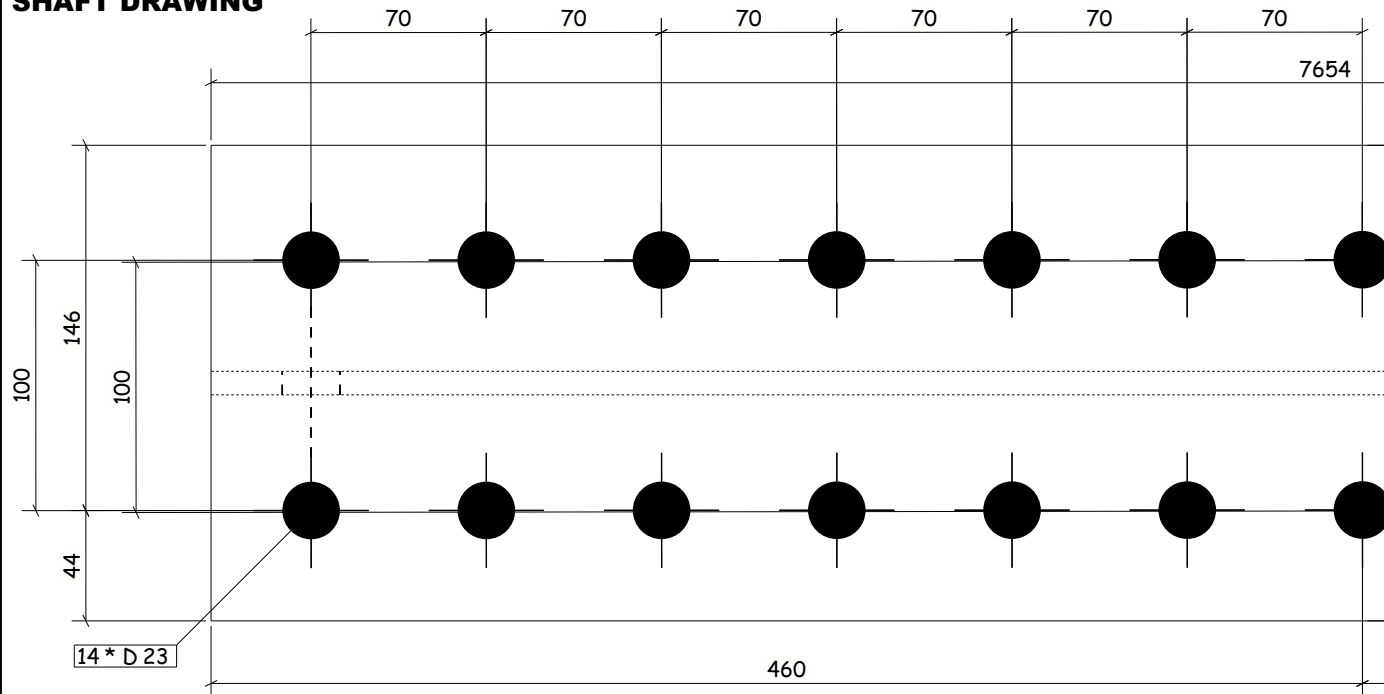

2	No	BEAM
---	----	------

REQUIRED AS DRAWN MARKED b/3

LOT	0	QTY	2
PHASE	1	QTY	2

Fabricación: HcB Ingeniería	
Project: CTIB 2026	
General Notes: ALL HOLES 22 Dia UNO FINISH: 0 Steel Grade: S235JR	Drawn:
	Checked:
	Scale: N.T.S.

HCB CTIB

Job No.	/	Dwg No.	/	Rev
1	/	b/3	/	

Rev	By	Date	Details				
b/3		IPE450	S235JR	2	8114.2	13.02	605.3
Mark		Profile	Grade	QTY	Length	Area	Weight