


SHAFT DRAWING

ALLOCATION TO ASSEMBLIES	
Assembly 175	TOTAL
B/170	1
Total	1

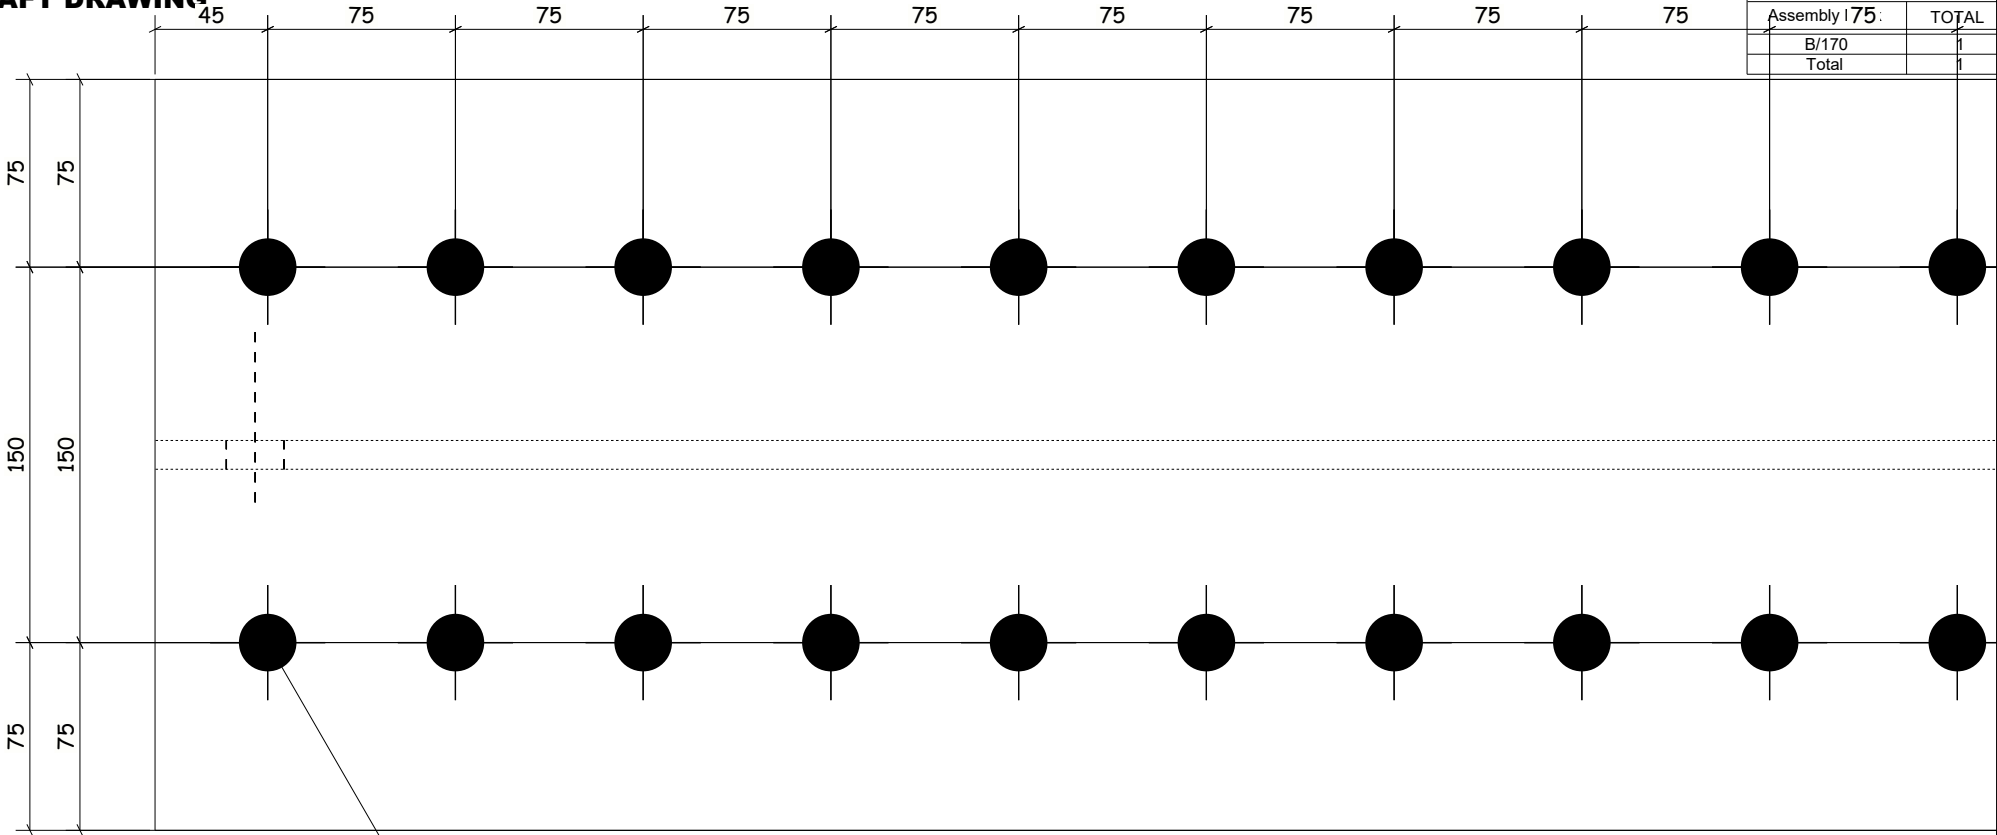

20 * D 23

1 No BEAM

40

b/32

REQUIRED AS DRAWN MARKED

b/32

LOT

QTY 1

PHASE 1

QTY 1

Fabricación

HCB Ingeniería

Project:

CTIB 2026

General Notes:

ALL HOLES 22 Dia UNO

FINISH: 0

Steel Grade: S235JR

Drawn:

Checked:

Scale: N.T.S.

HCB

CTIB

Job No. /

Dwg No. /

Rev

1 /

b/32 /

Rev	By	Date	Details				
b/32	Mark	EA450	S235JR	1	8101.0	16.29	1092.3
		Profile	Grade	QTY	Length	Area	Weight

Tekla structures

70