
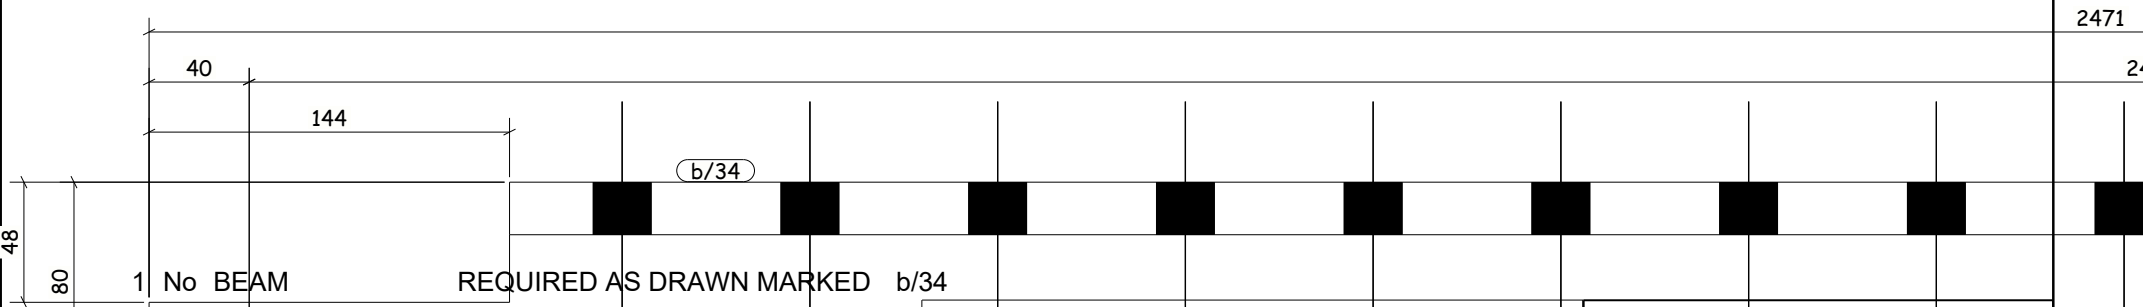


SHAFT DRAWING

ALLOCATION TO ASSEMBLIES	
Assembly Mark	TO 75
B/59	1
Total	1

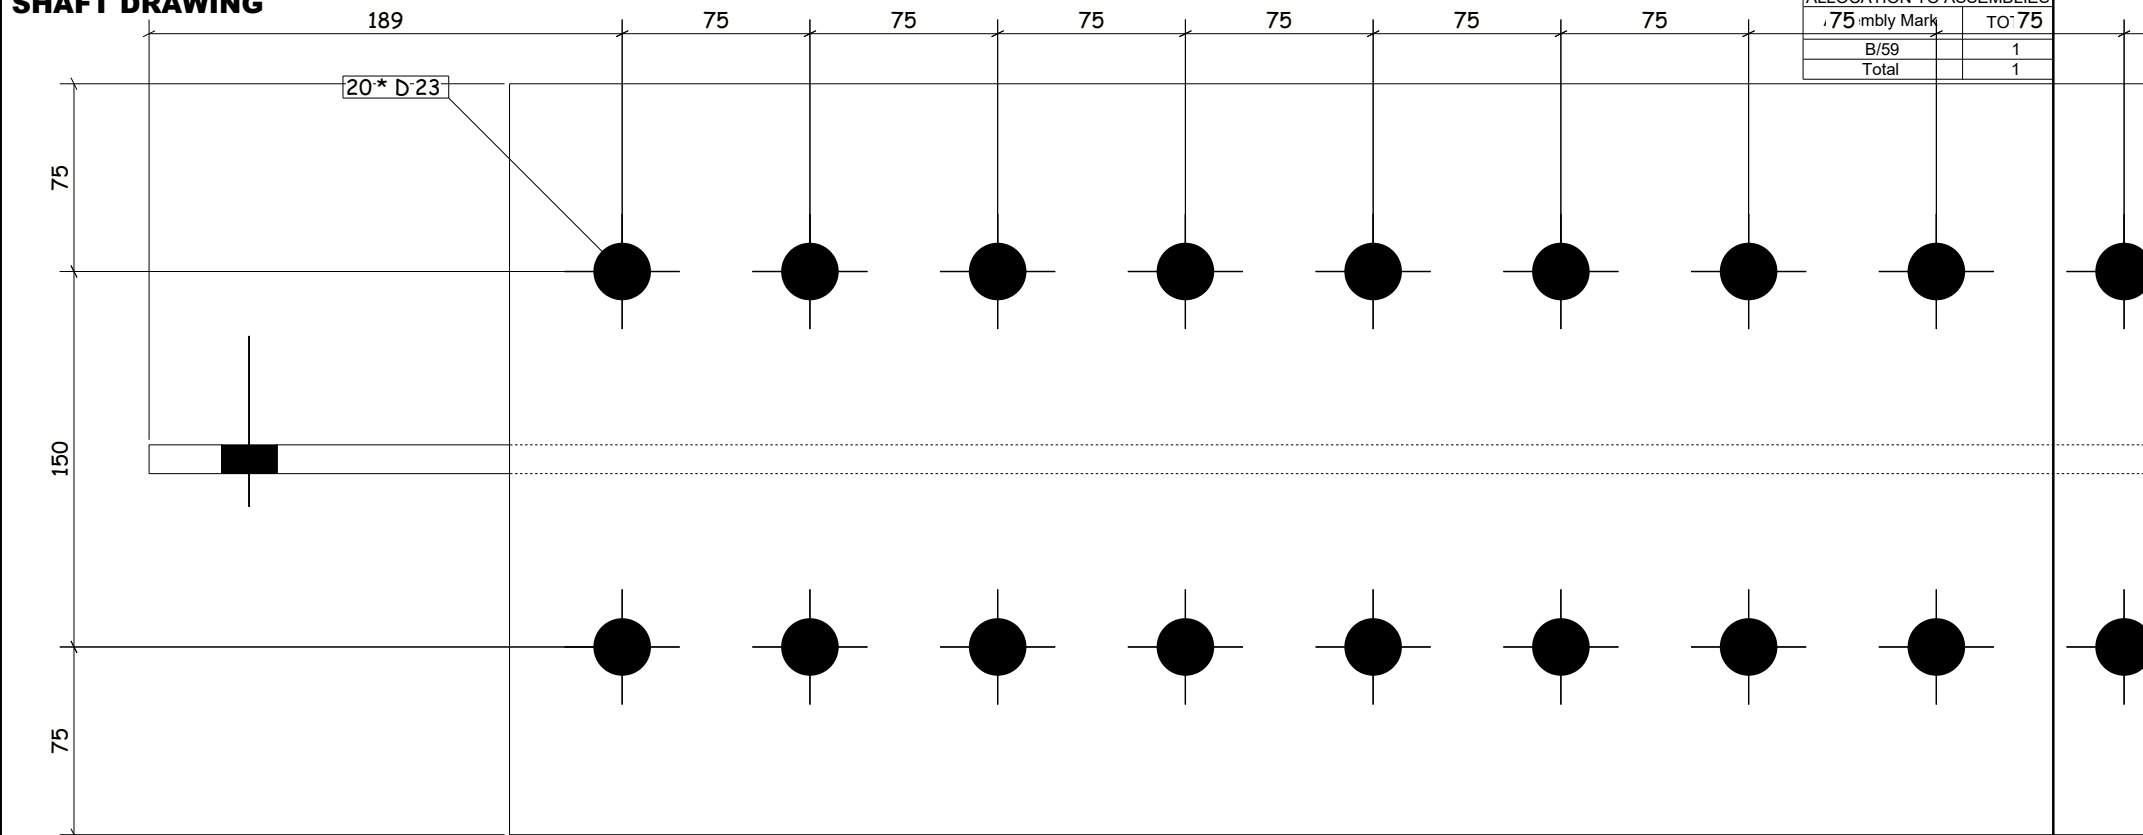

LOT	0	QTY	1
PHASE	1	QTY	1

Fabricación: HcB Ingeniería

Project: CTIB 2026

General Notes:

ALL HOLES	22	Dia UNO
-----------	----	---------

FINISH: 0
Steel Grade: S235JR

Drawn:

Checked:

Scale: N.T.S.

HCB CTIB

Job No. / Dwg No. / Rev

1 / b/34 /

Rev	By	Date	Details				
b/34		HEA450	S235JR	1	2471.2	4.97	318.3
Mark		Profile	Grade	QTY	Length	Area	Weight