
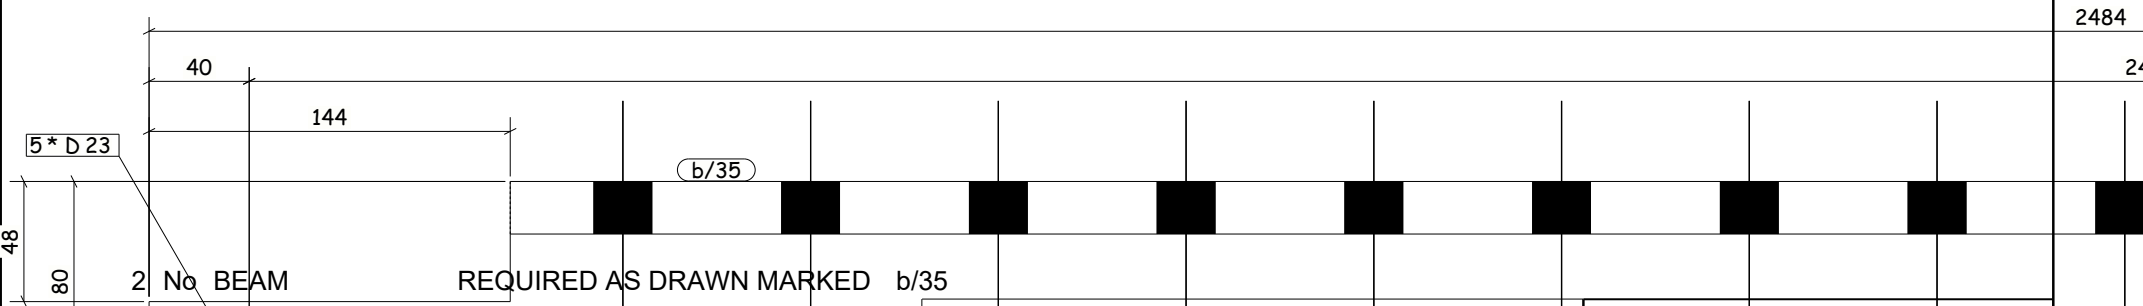


SHAFT DRAWING

ALLOCATION TO ASSEMBLIES	
75 mby Mark	TO 75
B/1	1
B/57	1
Total	2

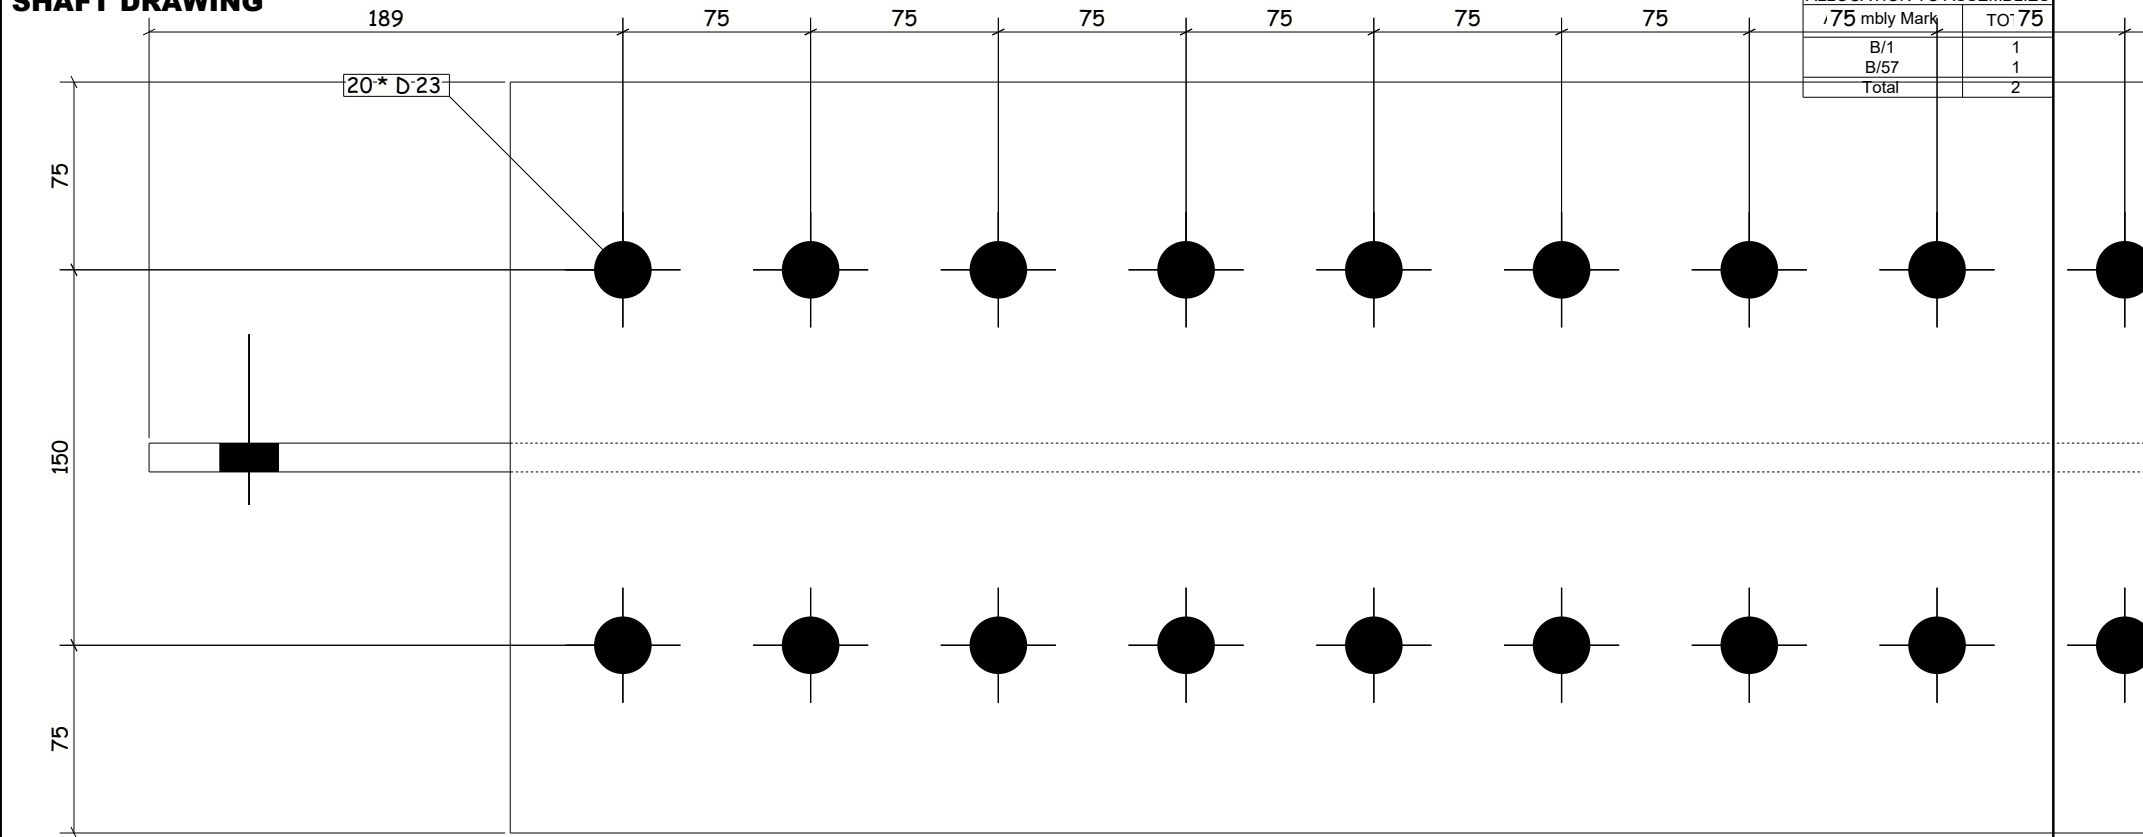

LOT	0	QTY	2
PHASE	1	QTY	2

Fabricación: HcB Ingeniería

Project: CTIB 2026

General Notes:

ALL HOLES 22 Dia UNO

FINISH: 0
Steel Grade: S235JR

Drawn:

Checked:

Scale: N.T.S.

HcB CTIB

Job No. / Dwg No. / Rev

1 / b/35 /

Rev	By	Date	Details				
b/35		HEA450	S235JR	2	2484.2	5.00	320.0
Mark		Profile	Grade	QTY	Length	Area	Weight