
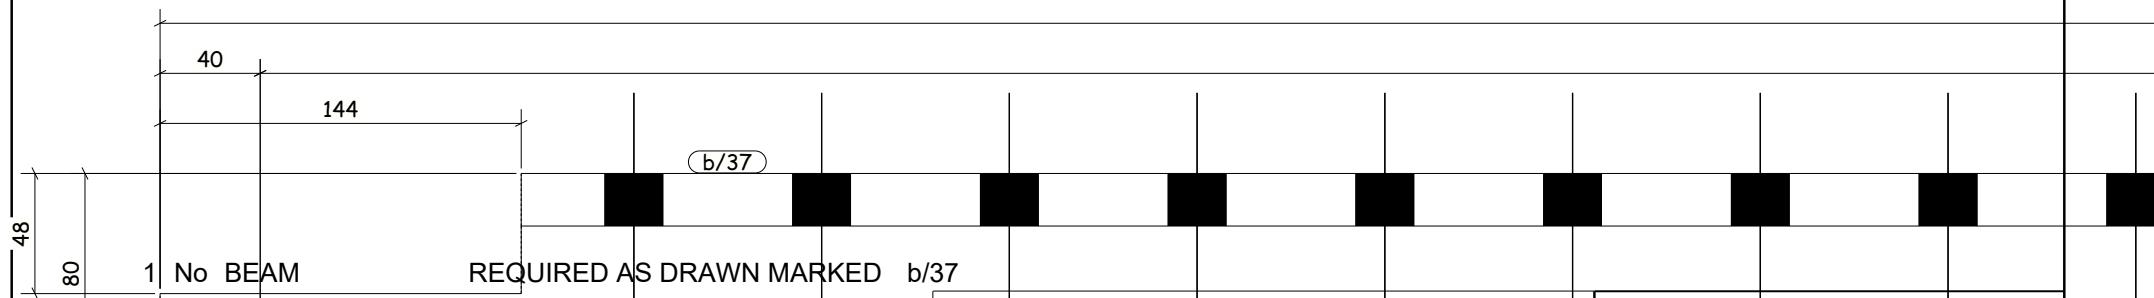


## SHAFT DRAWING

| ALLOCATION TO ASSEMBLIES |       |
|--------------------------|-------|
| 75 mbyl Mark             | TO 75 |
| B/56                     | 1     |
| Total                    | 1     |

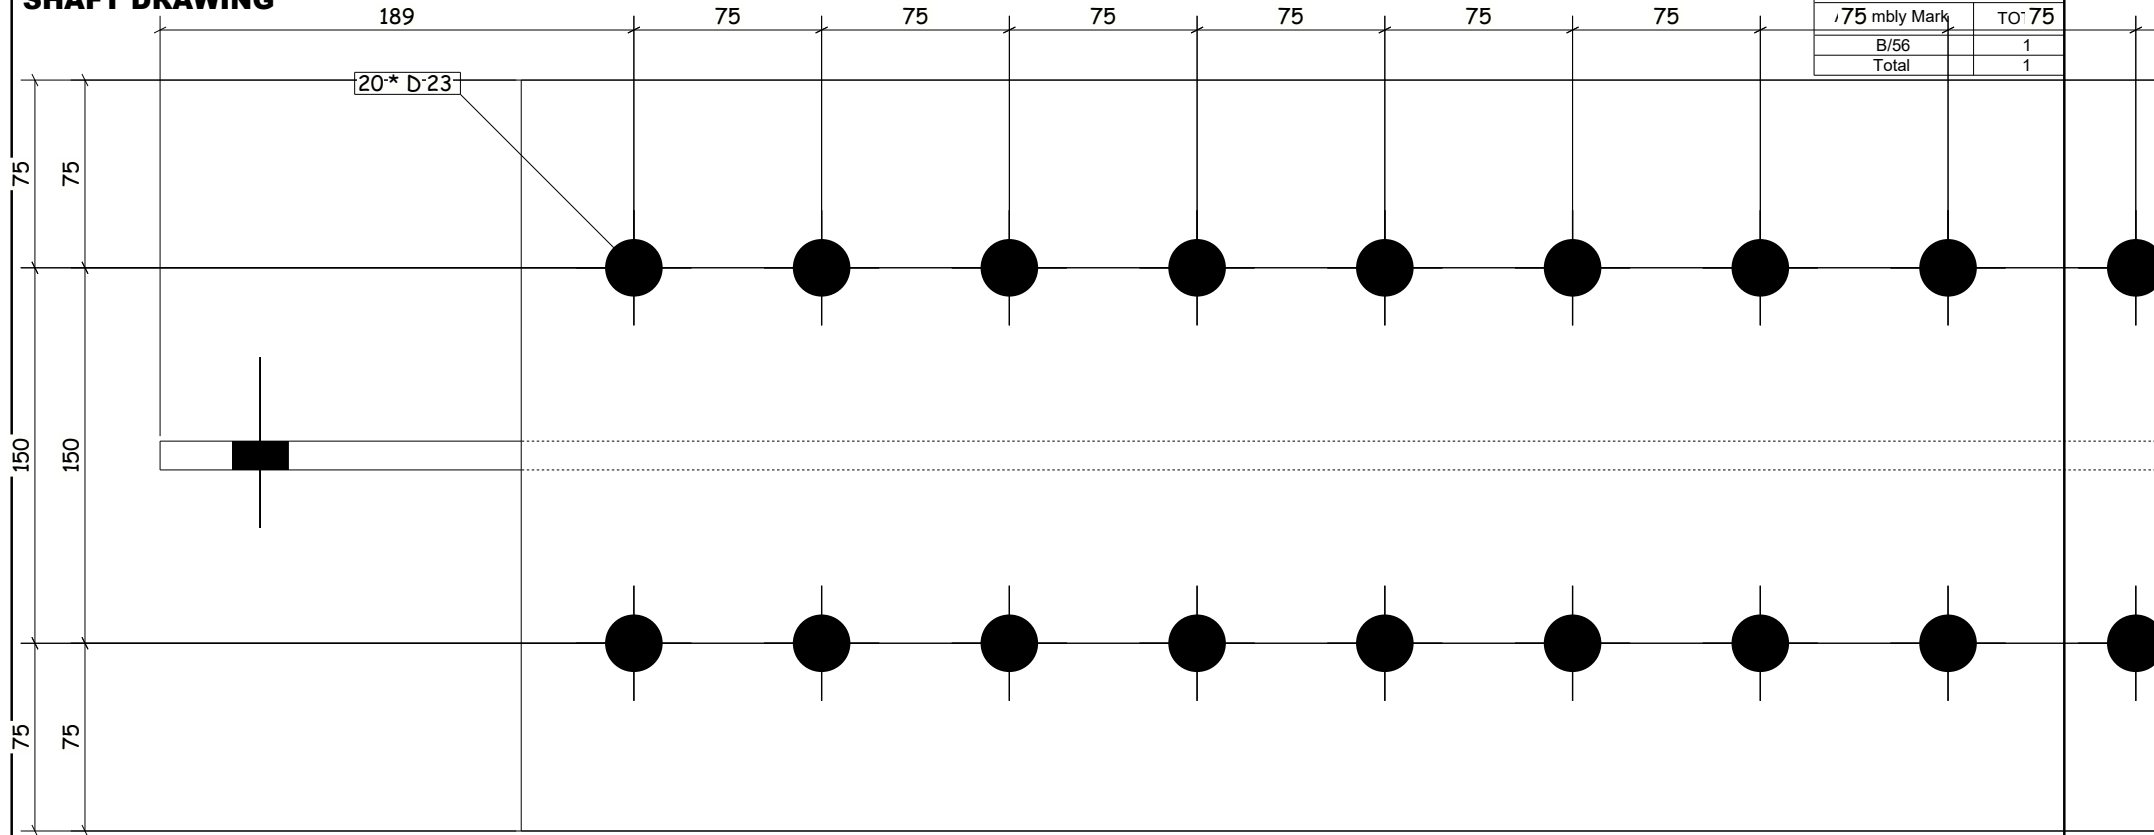

|       |   |     |   |
|-------|---|-----|---|
| LOT   | 0 | QTY | 1 |
| PHASE | 1 | QTY | 1 |

|     |      |         |         |     |        |       |        |  |
|-----|------|---------|---------|-----|--------|-------|--------|--|
|     |      |         |         |     |        |       |        |  |
|     |      |         |         |     |        |       |        |  |
|     |      |         |         |     |        |       |        |  |
| Rev | By   | Date    | Details |     |        |       |        |  |
|     | b/37 | HEA450  | S235JR  | 1   | 8321.8 | 16.74 | 1107.1 |  |
|     | Mark | Profile | Grade   | QTY | Length | Area  | Weight |  |

**Fabricación:** HcB Ingeniería

**Project:** CTIB 2026

|                       |
|-----------------------|
| <b>General Notes:</b> |
|-----------------------|

**ALL HOLES 22 Dia UNO**

**FINISH:** 0  
**Steel Grade:** S235JR

**Drawn:**

**Checked:**

**Scale:** N.T.S.

HCB CTIB

Job No. / Dwg No. / Rev

1 / b/37 /