


SHAFT DRAWING


ALLOCATION TO ASSEMBLIES	
Assembly Mark	TOTAL
C/2	1
Total	1

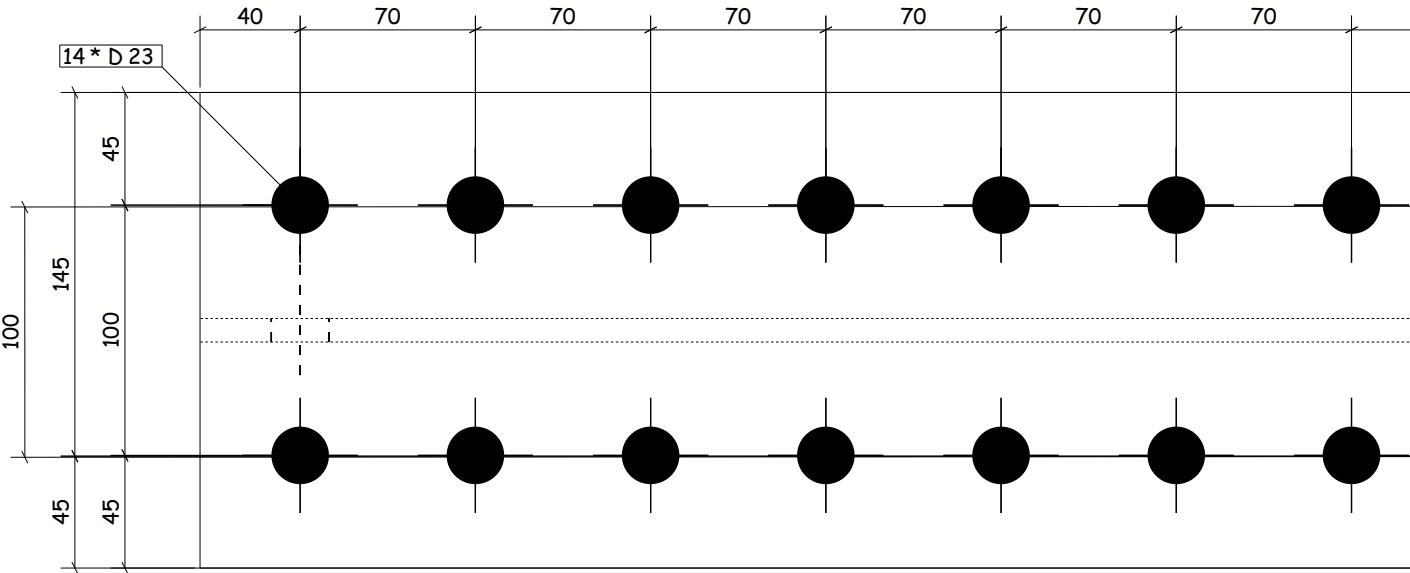

8074

8115

8075

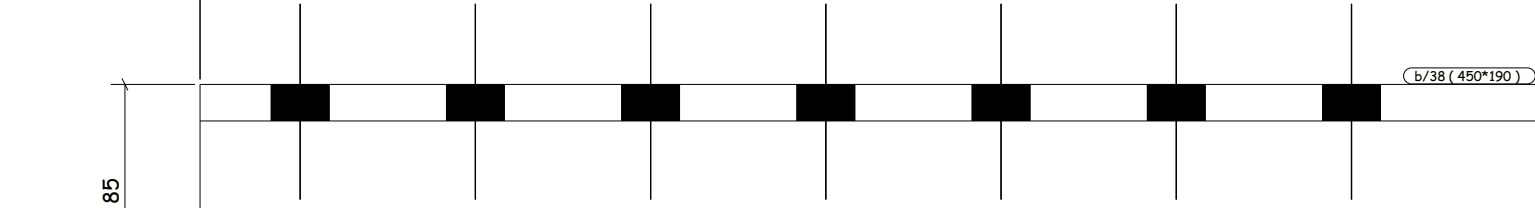

1 No BEAM

REQUIRED AS DRAWN MARKED b/38

LOT	0	QTY	1
PHASE	1	QTY	1

Fabricación: HcB Ingeniería

Project: CTIB 2026

General Notes:

ALL HOLES 22 Dia UNO

FINISH: 0

Steel Grade: S235JR

Drawn:

Checked:

Scale: N.T.S.

HcB CTIB

Job No. / Dwg No. / Rev

1 / b/38 /

5 * Ø 23

Rev	By	Date	Details					
b/38			IPE450	S235JR	1	8114.6	13.02	605.4
Mark			Profile	Grade	QTY	Length	Area	Weight

Tekla structures