
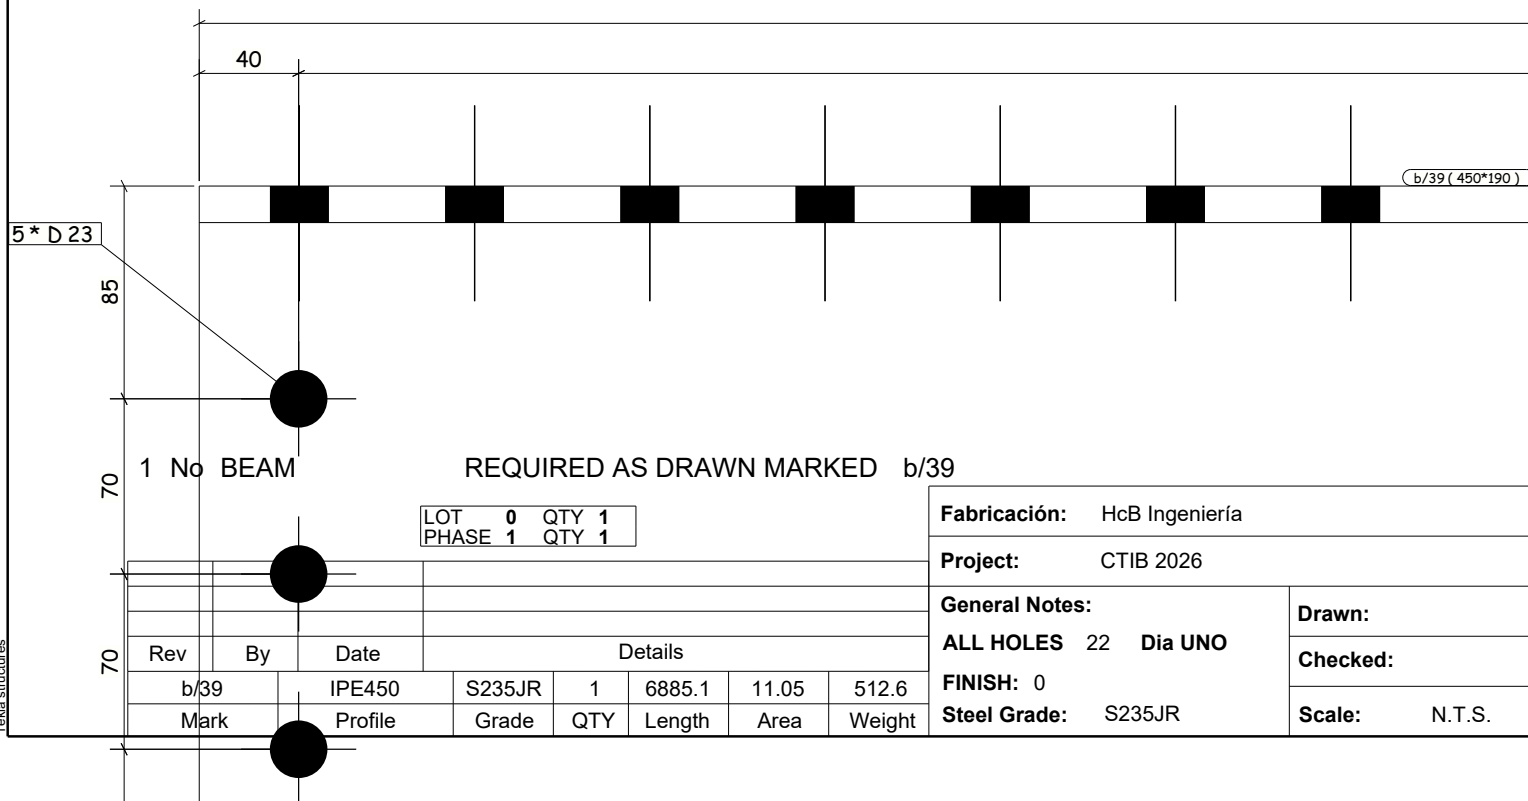


SHAFT DRAWING

ALLOCATION TO ASSEMBLIES	
Ass: 3907 lark	TOTAL
B/117	1
Total	1

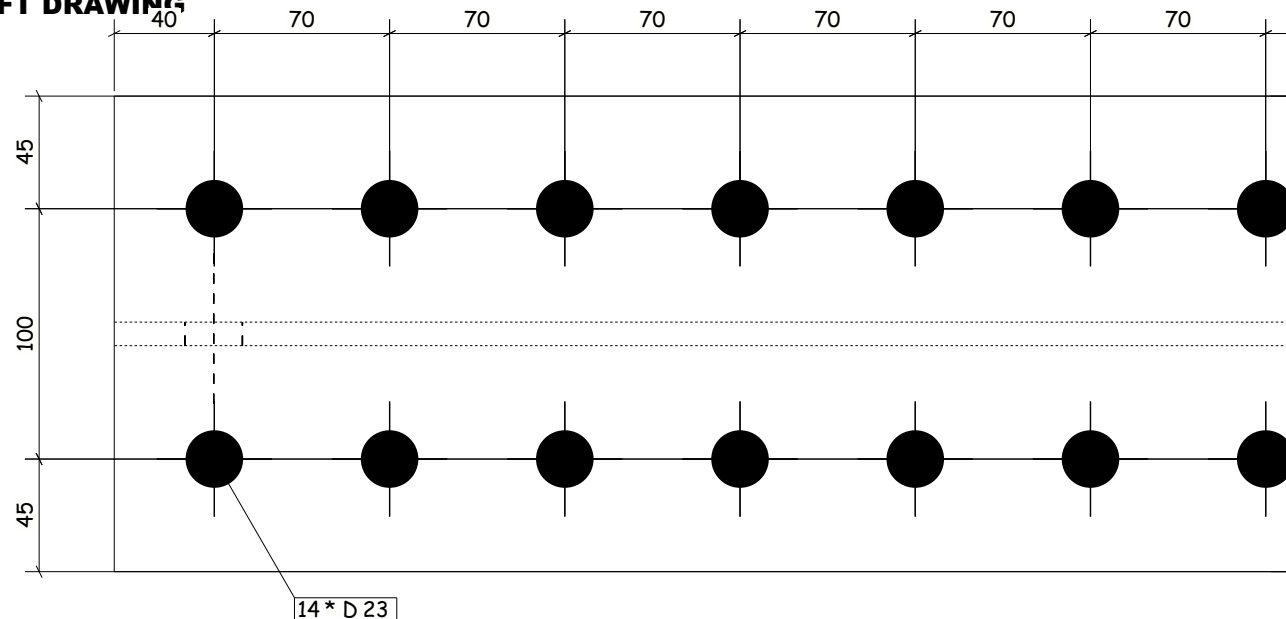

Fabricación: HcB Ingeniería

Project: CTIB 2026

General Notes:

ALL HOLES 22 Dia UNO

FINISH: 0

Steel Grade: S235JR

Drawn:

Checked:

Scale: N.T.S.

HcB CTIB

Job No. / Dwg No. / Rev

1 / b/39 /