



SHAFT DRAWING

ALLOCATION TO ASSEMBLIES		
Assembly Mark	TOTAL	
B/1165 6264	1	
Total	1	

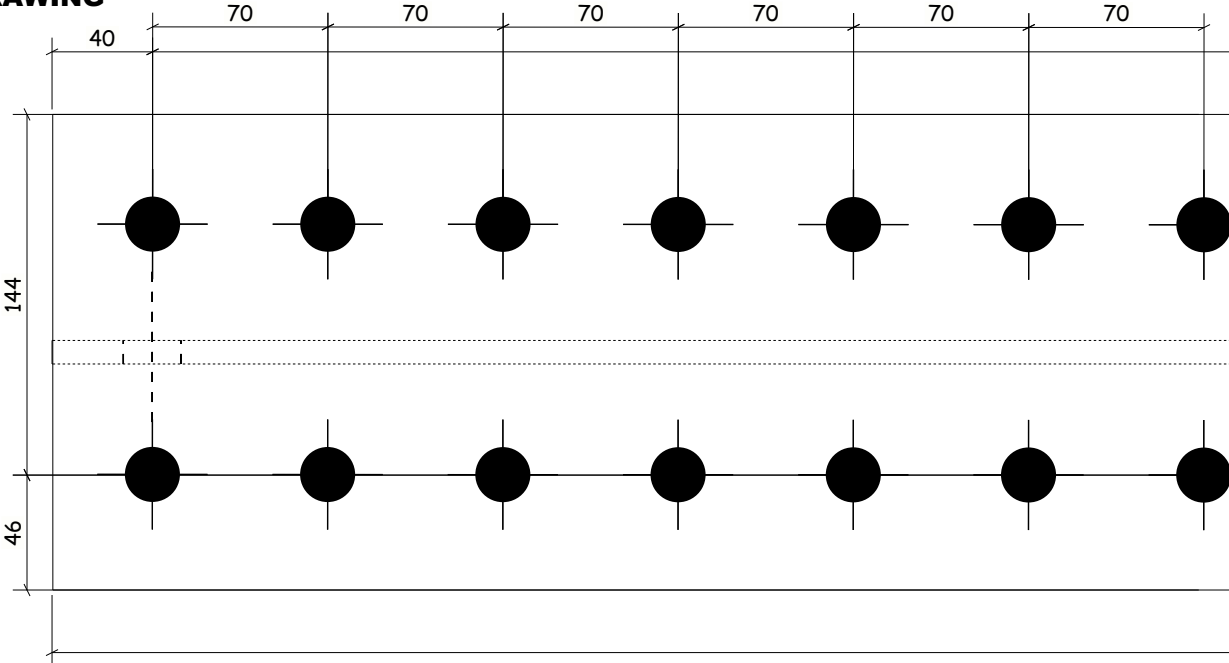

6264

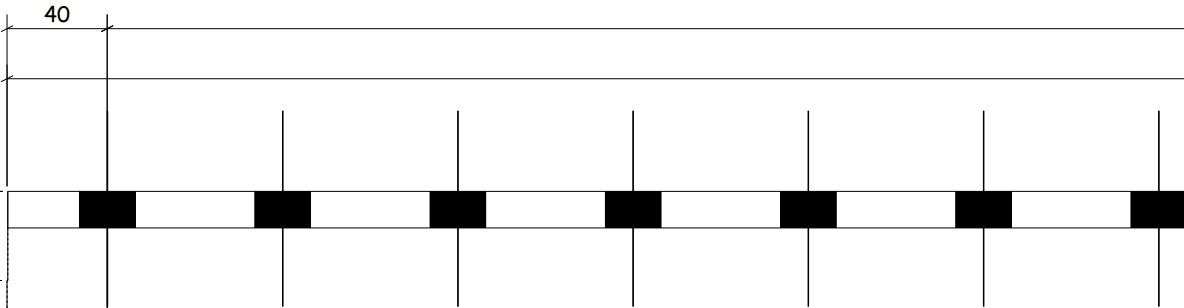

6264

6304

b/40

1 No BEAM

REQUIRED AS DRAWN MARKED b/40

LOT	0	QTY	1
PHASE	1	QTY	1

Fabricación: HcB Ingeniería

Project: CTIB 2026

General Notes:
ALL HOLES 22 Dia UNO

FINISH: 0
Steel Grade: S235JR

Drawn:

Checked:

Scale: N.T.S.

HcB CTIB

Job No. / Dwg No. / Rev
1 / b/40 /

5 * D 23

Rev	By	Date	Details				
70	b/40	IPE450	S235JR	1	6304.3	10.12	470.3
Mark	Profile	Grade	QTY	Length	Area	Weight	

Tekla structures