


SHAFT DRAWING

ALLOCATION TO ASSEMBLIES	
Asser 7919 k	TOTAL
B/1172	1
Total	1

39 70 70 70 70 70 70

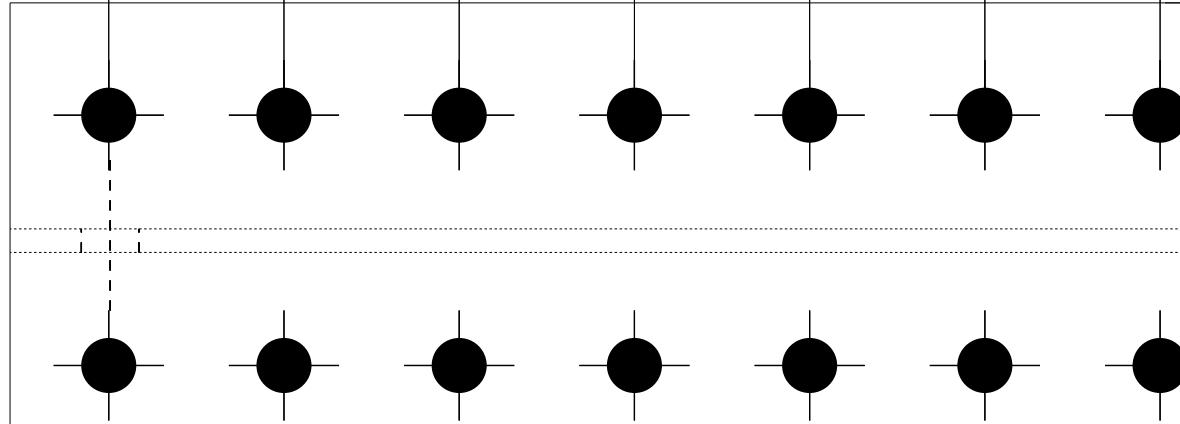

8836

8756

40

(b/41)

85

70

5 * D 23

1 No BEAM

REQUIRED AS DRAWN MARKED b/41

LOT	0	QTY	1
PHASE	1	QTY	1

Fabricación: HcB Ingeniería

Project: CTIB 2026

General Notes:

ALL HOLES 22 Dia UNO

FINISH: 0

Steel Grade: S235JR

Drawn:

Checked:

Scale: N.T.S.

HcB CTIB

Job No. / Dwg No. / Rev

1 / b/41 /

70

Rev

By

Date

Details

b/41

Mark

E450

Profile

S235JR

Grade

1

QTY

8835.7

Length

14.18

Area

659.2

Weight

70