


SHAFT DRAWING

ALLOCATION TO ASSEMBLIES	
Assembly Mark	TOTAL
B/1173	1
Total	1

5841

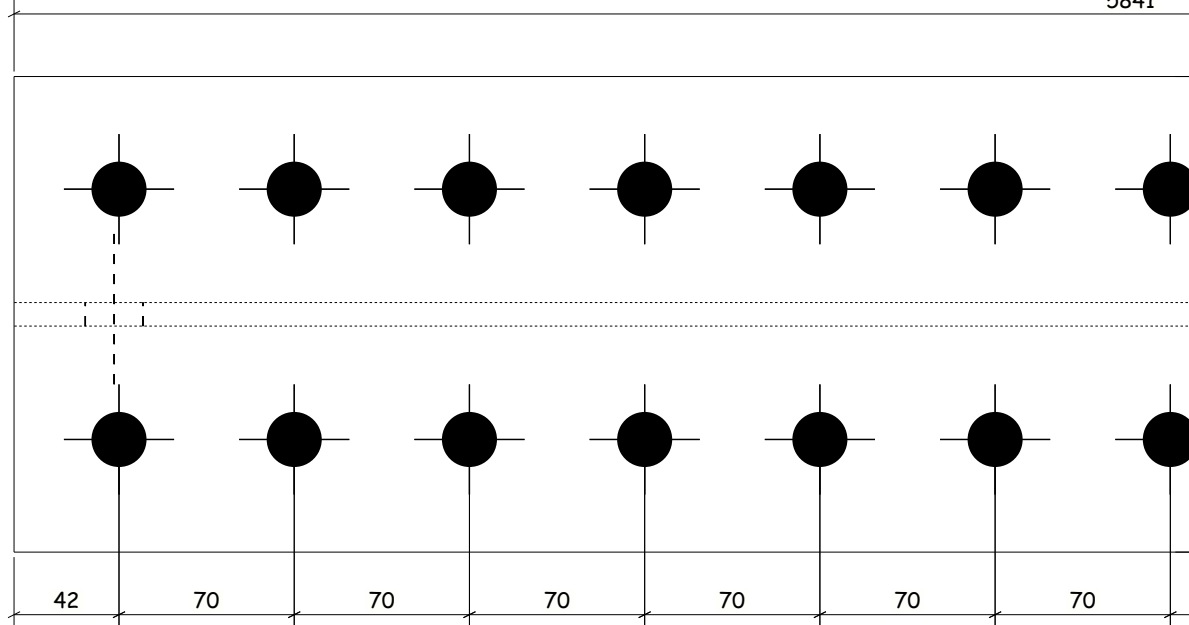


6261

6301

6261

40

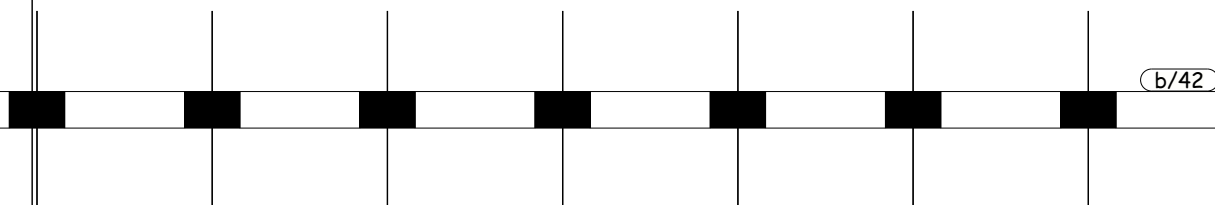

b/42

85

1	No	BEAM
---	----	------

REQUIRED AS DRAWN MARKED b/42

LOT	0	QTY	1
PHASE	1	QTY	1

Fabricación: HcB Ingeniería

Project: CTIB 2026

General Notes:

ALL HOLES 22 Dia UNO

FINISH: 0

Steel Grade: S235JR

Drawn:

Checked:

Scale: N.T.S.

HCB CTIB

Job No. / Dwg No. / Rev

1 / b/42 /

Rev	By	Date	Details				
b/42		PE450	S235JR	1	6300.8	10.11	470.0
Mark		Profile	Grade	QTY	Length	Area	Weight

Tekla structures

5 * D 23

70