


SHAFT DRAWING

ALLOCATION TO ASSEMBLIES	
Assembly Mark	TOTAL
B/180	3
Total	3

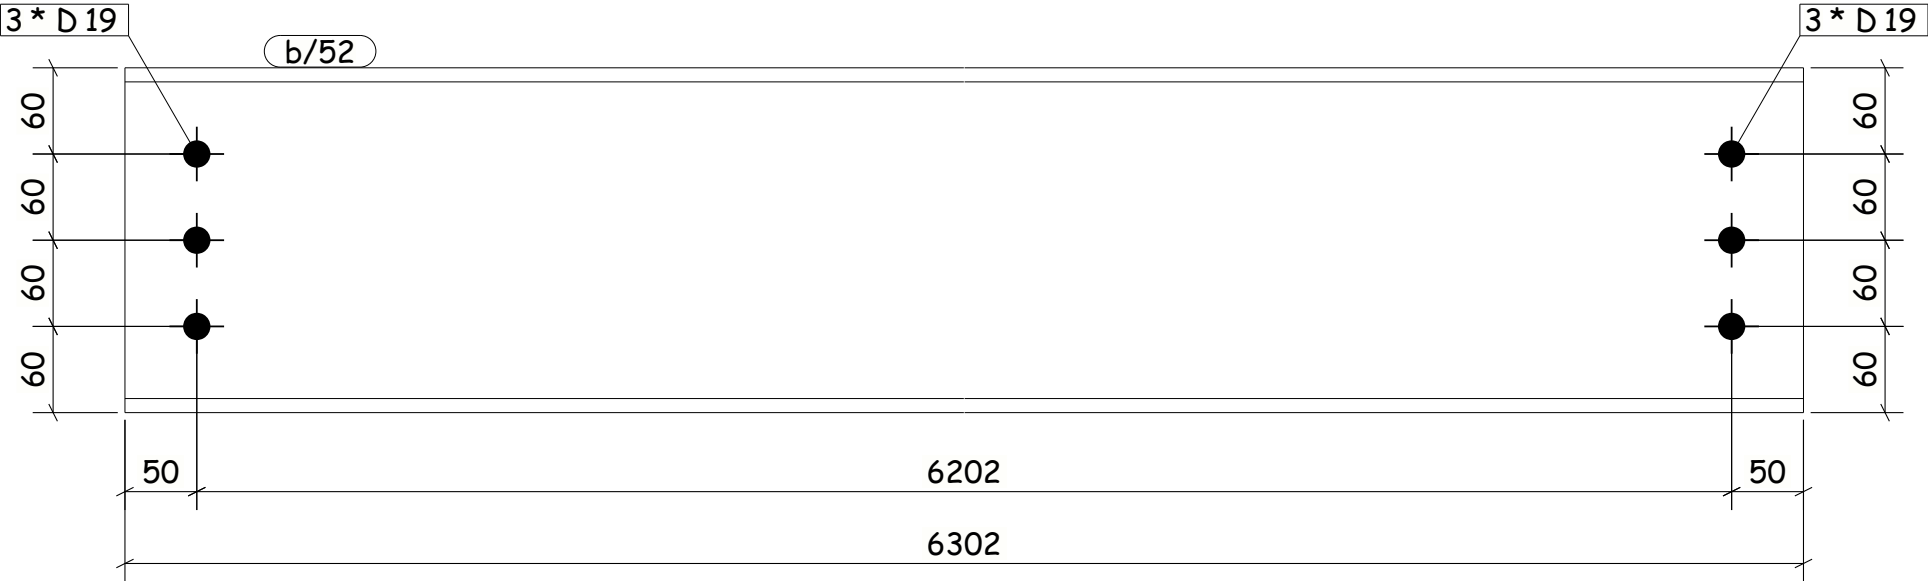

3 No BEAM

REQUIRED AS DRAWN MARKED b/52

LOT	0	QTY	3
PHASE	1	QTY	3

Rev	By	Date	Details				
b/52		IPE240	S235JR	3	6301.8	5.81	183.9
Mark		Profile	Grade	QTY	Length	Area	Weight

Fabricación: HcB Ingeniería

Project: CTIB 2026

General Notes:

ALL HOLES 22 Dia UNO

FINISH: 0

Steel Grade: S235JR

Drawn:

Checked:

Scale: N.T.S.

HcB CTIB

Job No. / Dwg No. / Rev

1 / b/52 /

A4