


SHAFT DRAWING

ALLOCATION TO ASSEMBLIES	
Assembly Mark	TOTAL
B/187	1
Total	1

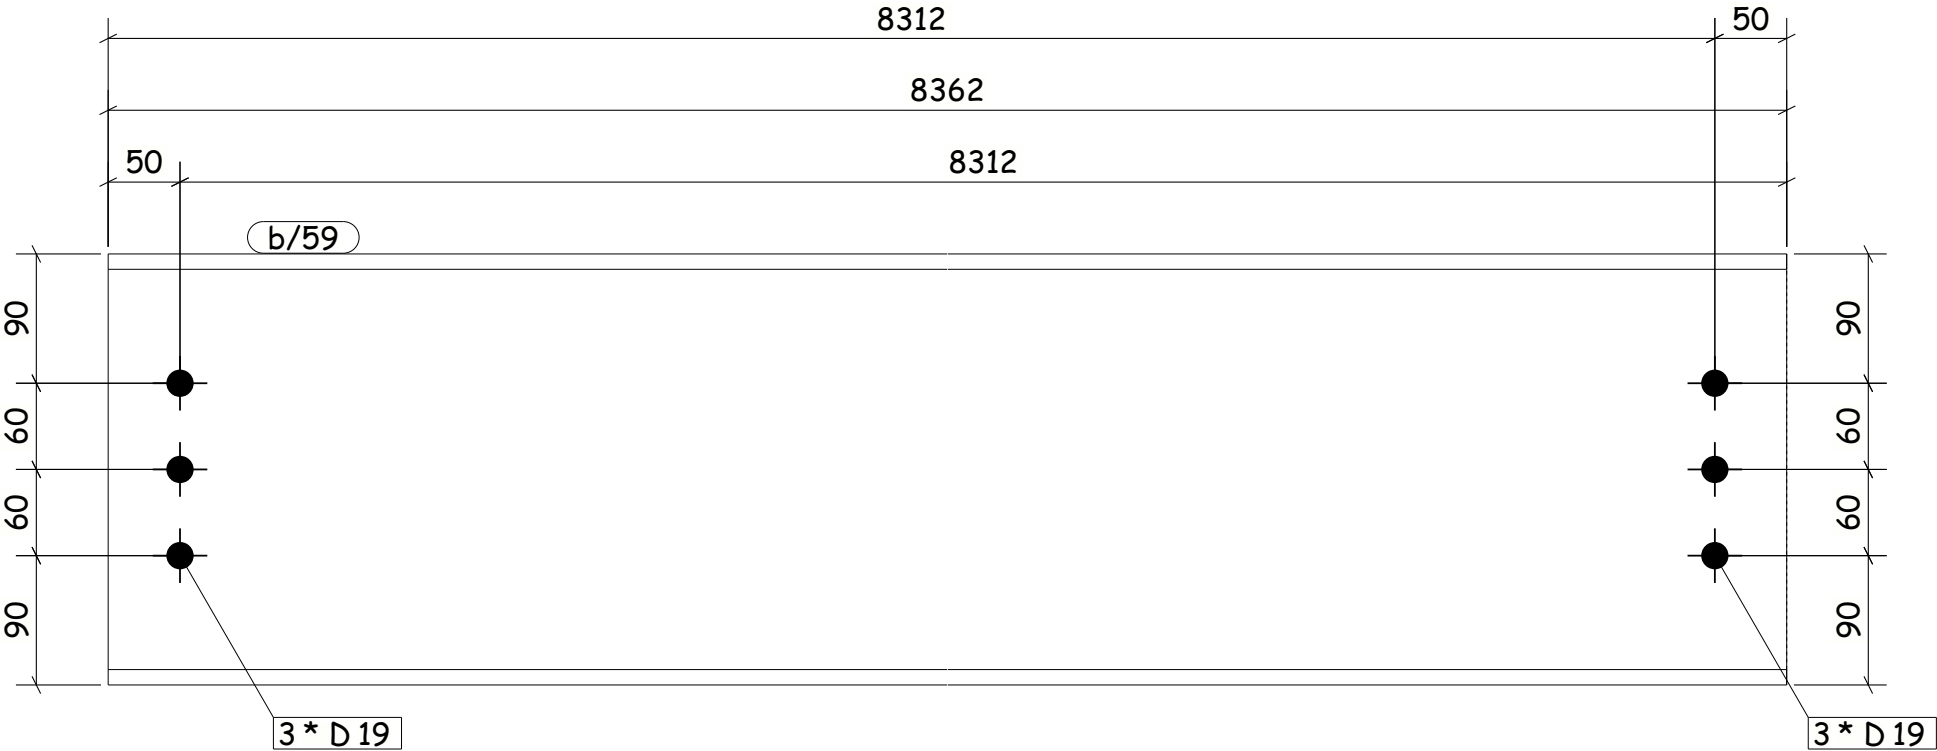

1 No BEAM

REQUIRED AS DRAWN MARKED b/59

LOT	0	QTY	1
PHASE	1	QTY	1

Rev	By	Date	Details				
b/59	IPE300		S235JR	1	8361.7	9.69	340.5
Mark	Profile		Grade	QTY	Length	Area	Weight

Fabricación: HcB Ingeniería

Project: CTIB 2026

General Notes:

ALL HOLES 22 Dia UNO

FINISH: 0

Steel Grade: S235JR

Drawn:

Checked:

Scale: N.T.S.

HcB CTIB

Job No. / Dwg No. / Rev

1 / b/59 /

A4