


SHAFT DRAWING

ALLOCATION TO ASSEMBLIES	
Assembly Mark	TOTAL
B/46	1
Total	1

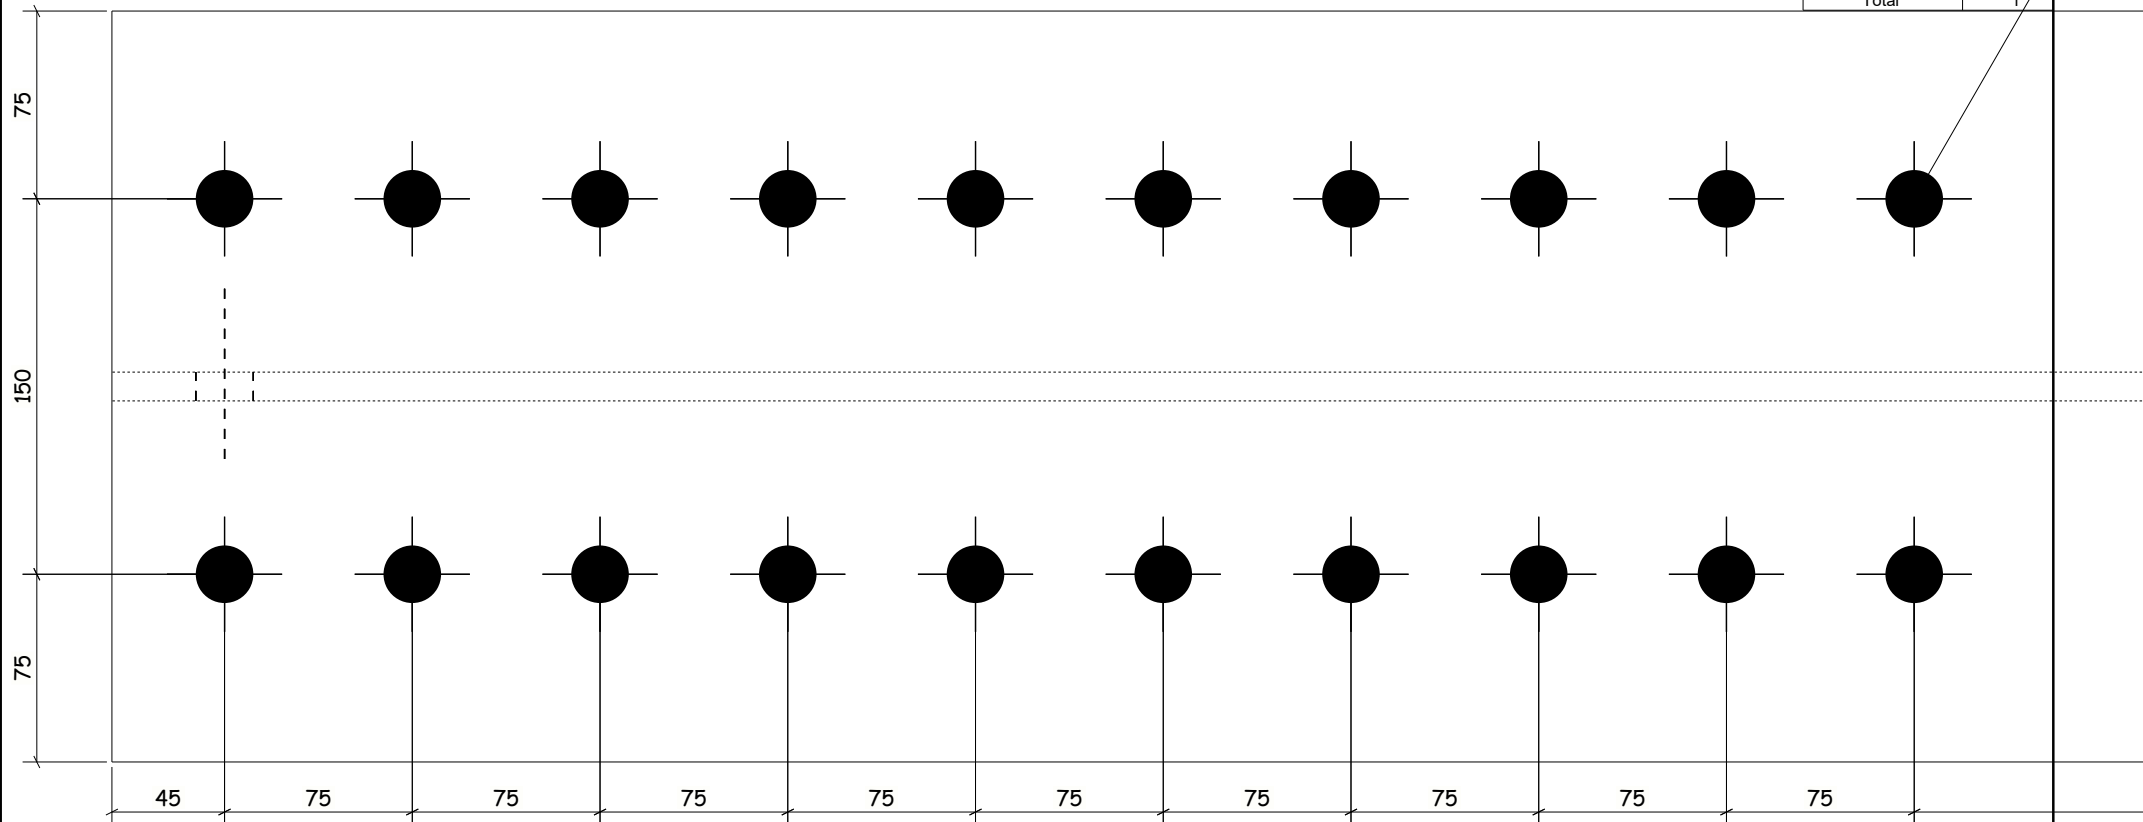

1 No BEAM

REQUIRED AS DRAWN MARKED b/6

LOT	0	QTY	1
PHASE	1	QTY	1

Fabricación: HcB Ingeniería		7867			
Project: CTIB 2026					
General Notes:		Drawn:			
ALL HOLES 22 Dia UNO		Ch		Job No	
F : 0				Dwg No. /	
Steel Grade: S235JR		Scale: N.T.S.		1 / b/6 /	

5 * D 23

Tekla structures

801