


SHAFT DRAWING

ALLOCATION TO ASSEMBLIES	
Assembly Mark	TOTAL
B/198	2
Total	2

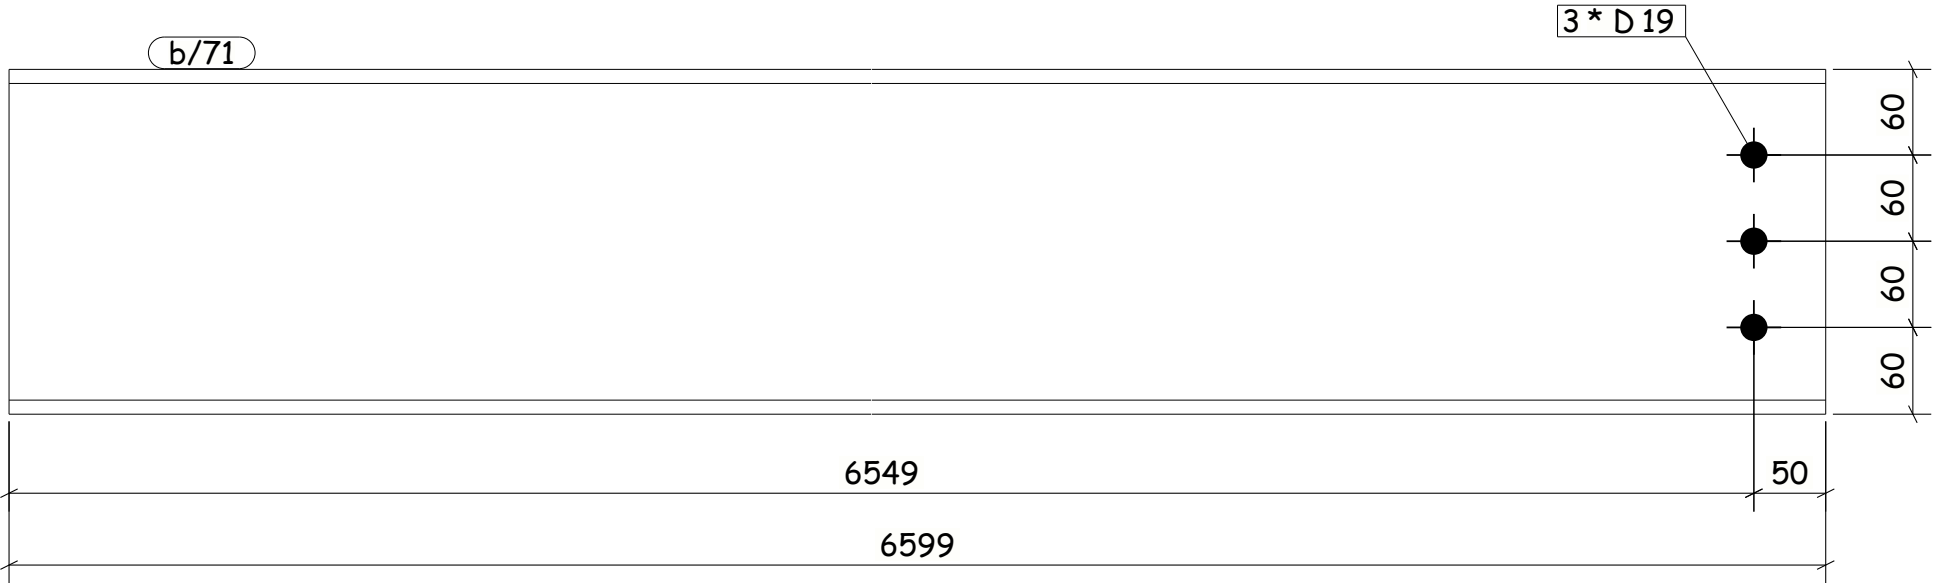

2 No BEAM REQUIRED AS DRAWN MARKED b/71

LOT	0	QTY	2
PHASE	1	QTY	2

Rev	By	Date	Details				
b/71	IPE240		S235JR	2	6598.6	6.08	192.6
Mark	Profile		Grade	QTY	Length	Area	Weight

Fabricación: HcB Ingeniería

Project: CTIB 2026

General Notes:

ALL HOLES 22 Dia UNO

FINISH: 0

Steel Grade: S235JR

Drawn:

Checked:

Scale: N.T.S.



Job No. / Dwg No. / Rev

1 / b/71 /

A4