


SHAFT DRAWING

ALLOCATION TO ASSEMBLIES	
Assembly Mark	TOTAL
B/201	1
Total	1

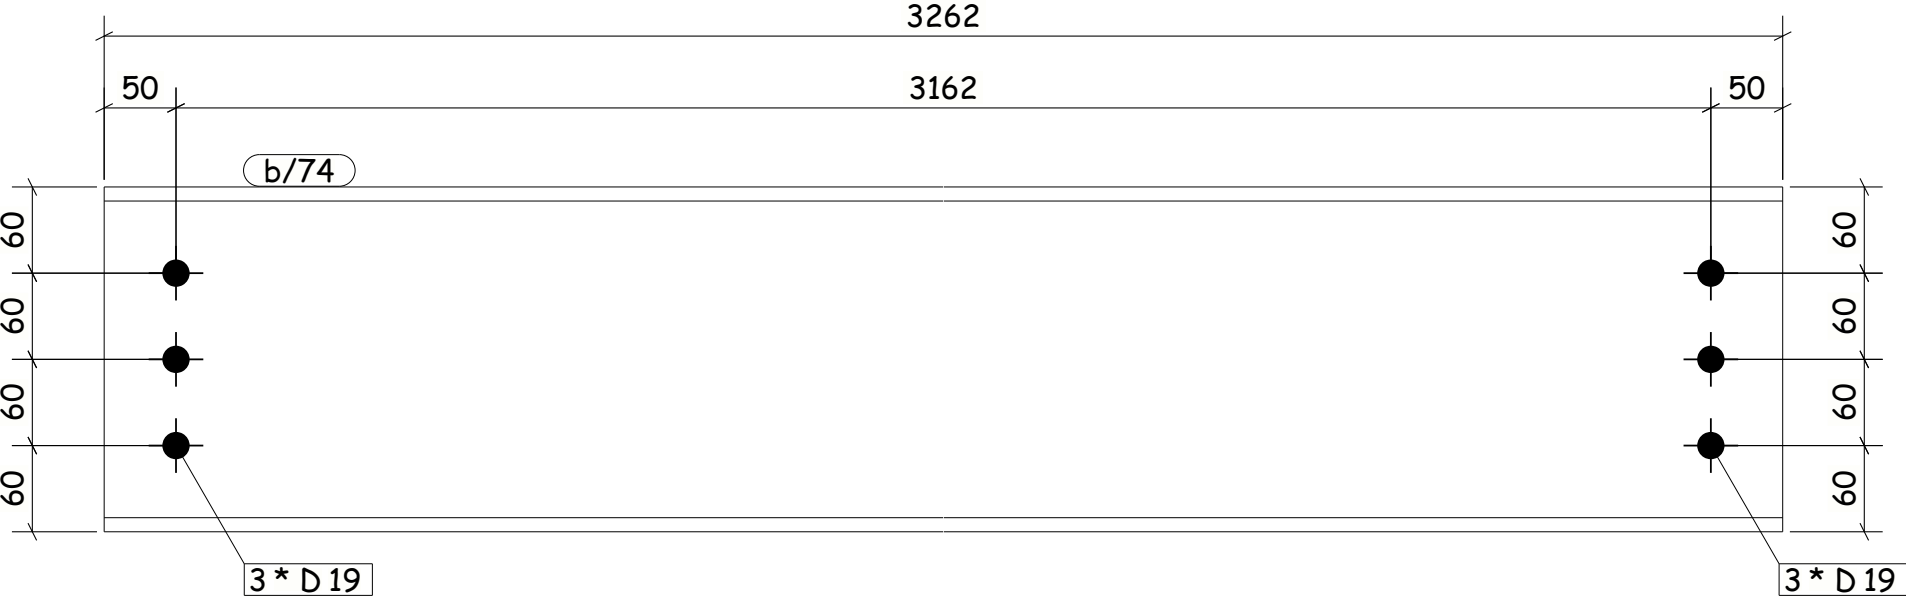

1 No BEAM

REQUIRED AS DRAWN MARKED b/74

LOT	0	QTY	1
PHASE	1	QTY	1

Rev	By	Date	Details				
b/74	IPE240		S235JR	1	3261.7	3.01	95.2
Mark	Profile		Grade	QTY	Length	Area	Weight

Fabricación: HcB Ingeniería	
Project: CTIB 2026	
General Notes:	Drawn:
ALL HOLES 22 Dia UNO	Checked:
FINISH: 0	Scale: N.T.S.
Steel Grade: S235JR	



Job No. /	Dwg No. /	Rev	A4
1 /	b/74 /		