


SHAFT DRAWING

ALLOCATION TO ASSEMBLIES	
Assembly Mark	TOTAL
B/112	1
Total	1

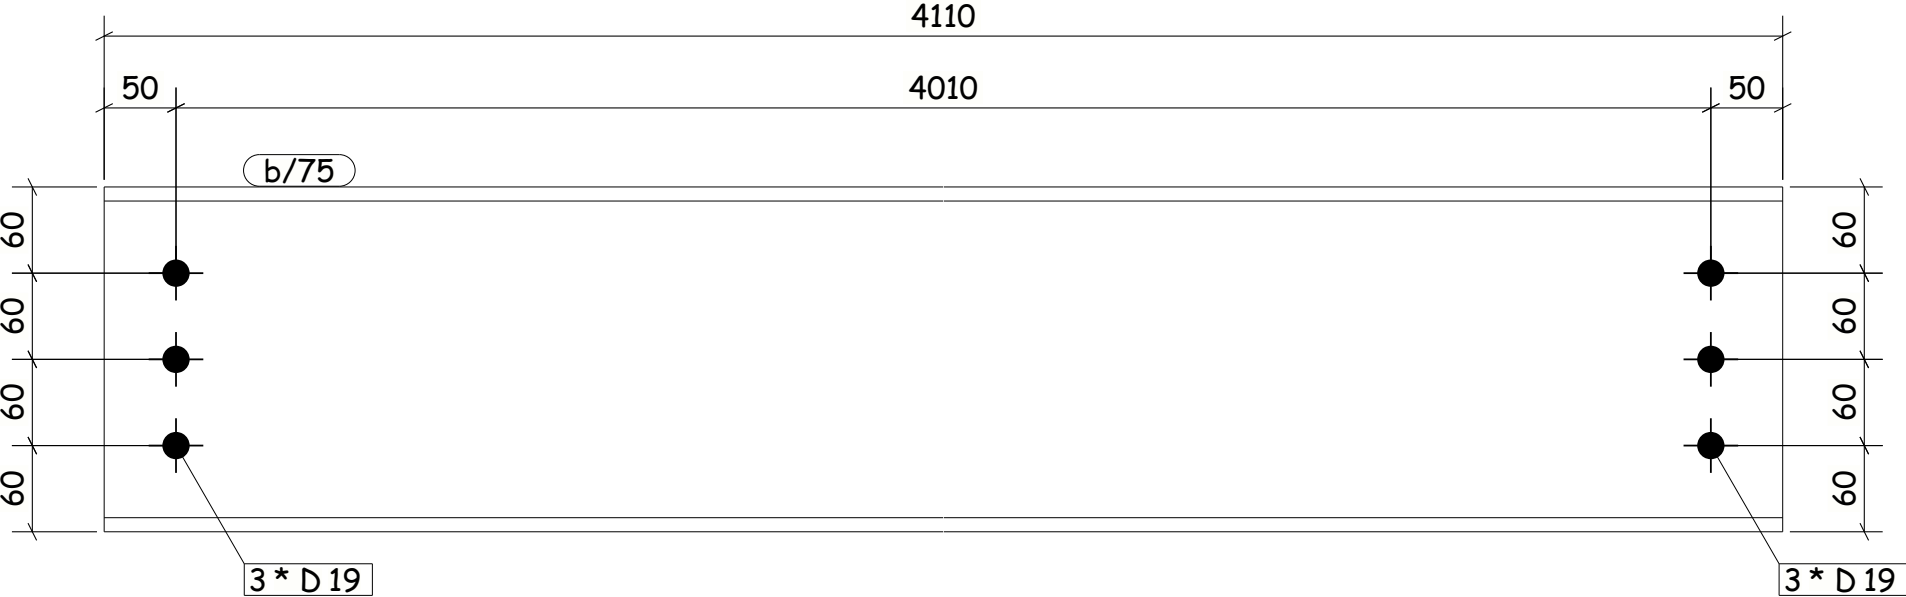

1 No BEAM

REQUIRED AS DRAWN MARKED b/75

LOT	0	QTY	1
PHASE	1	QTY	1

Rev	By	Date	Details				
b/75		IPE240	S235JR	1	4110.1	3.79	120.0
Mark		Profile	Grade	QTY	Length	Area	Weight

Fabricación: HcB Ingeniería

Project: CTIB 2026

General Notes:

ALL HOLES 22 Dia UNO

FINISH: 0

Steel Grade: S235JR

Drawn:

Checked:

Scale: N.T.S.

HcB CTIB

Job No. / Dwg No. / Rev

1 / b/75 /

A4