


SHAFT DRAWING

ALLOCATION TO ASSEMBLIES	
Assembly Mark	TOTAL
B/203	2
Total	2

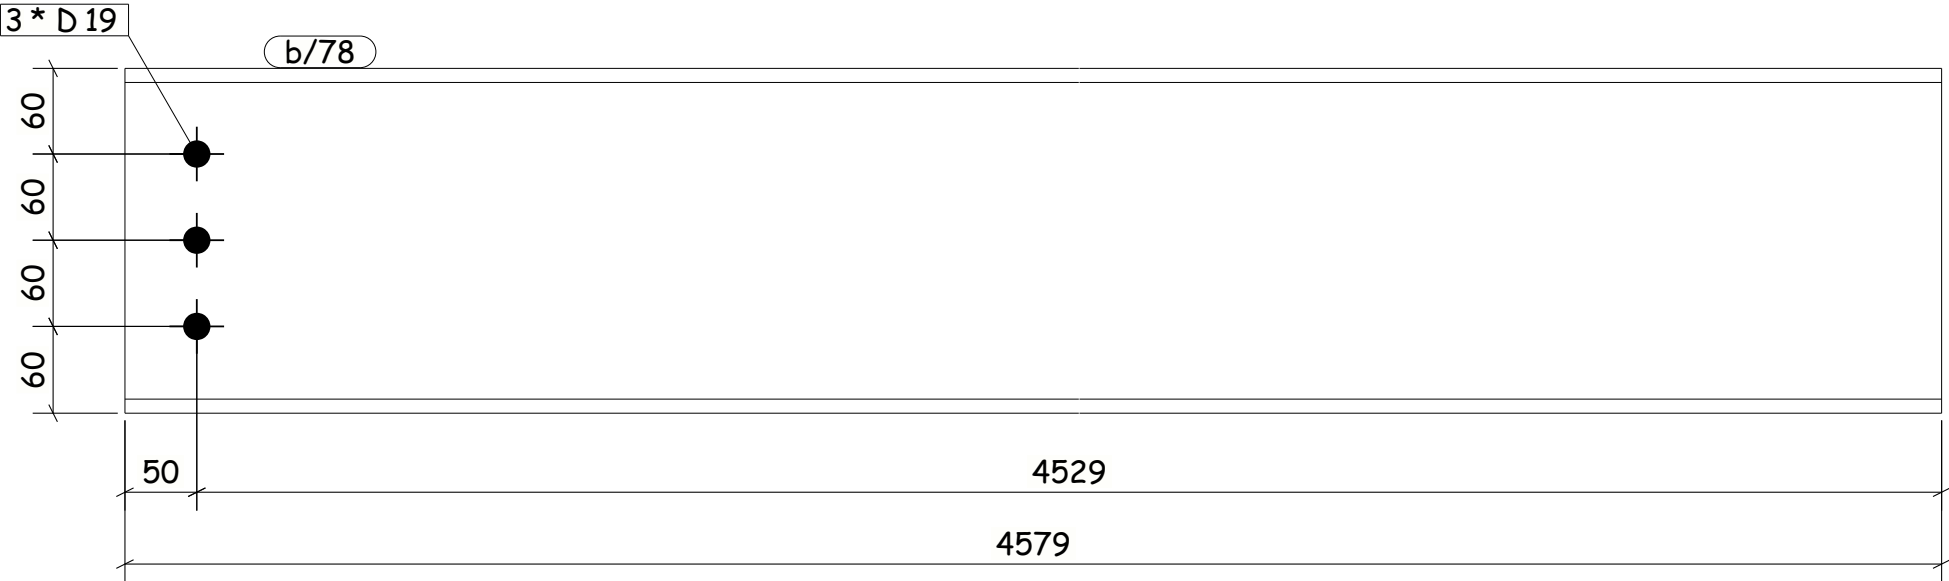

2 No BEAM REQUIRED AS DRAWN MARKED b/78

LOT	0	QTY	2
PHASE	1	QTY	2

Rev	By	Date	Details				
b/78		IPE240	S235JR	2	4578.6	4.22	133.6
Mark		Profile	Grade	QTY	Length	Area	Weight

Fabricación: HcB Ingeniería	
Project: CTIB 2026	
General Notes:	Drawn:
ALL HOLES 22 Dia UNO	Checked:
FINISH: 0	Scale: N.T.S.
Steel Grade: S235JR	



Job No. /	Dwg No. /	Rev	A4
1 /	b/78 /		