
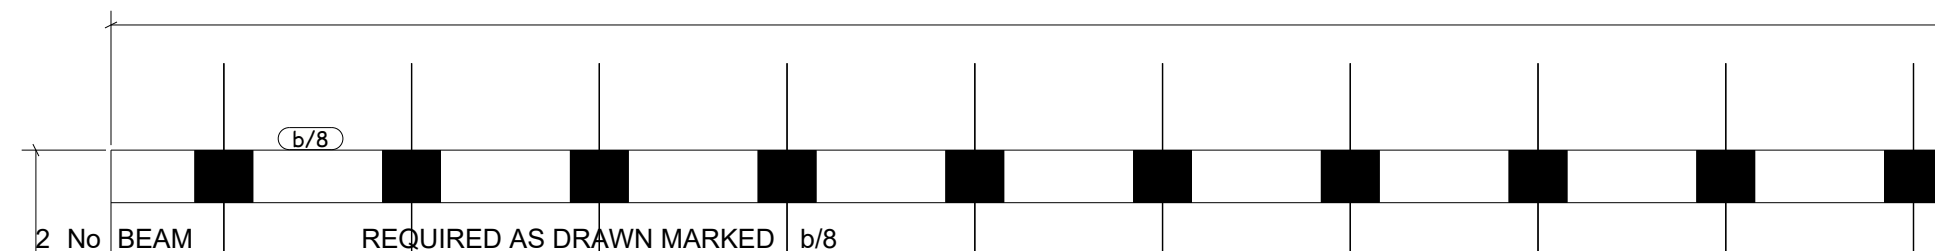


SHAFT DRAWING

ALLOCATION TO ASSEMBLIES	
Assembly	TOTAL
B/169	1
B/1043	1
Total	2

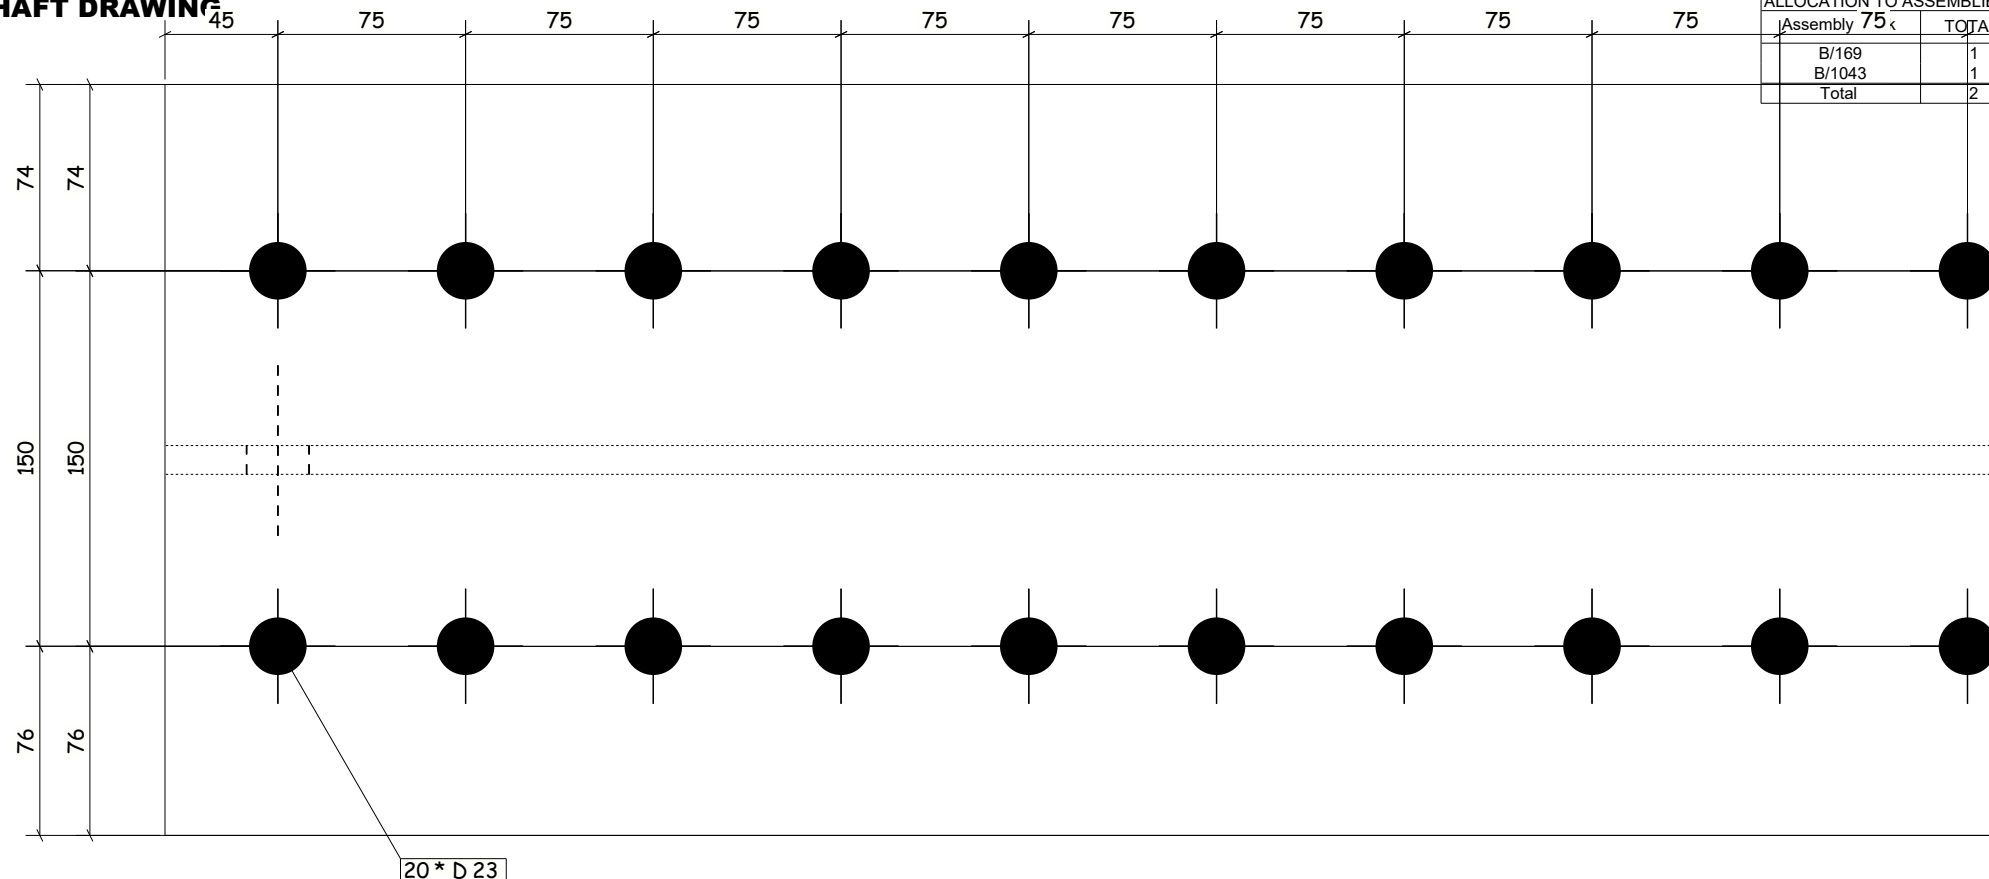

LOT	0	QTY	2
PHASE	1	QTY	2

Fabricación: HcB Ingeniería

Project: CTIB 2026

General Notes:

ALL HOLES 22 Dia UNO

FINISH: 0

Steel Grade: S235JR

Drawn:

Checked:

Scale: N.T.S.

HCB CTIB

Job No. / Dwg No. / Rev

1 / b/8 /

Rev	By	Date	Details				
b/8		HEA450	S235JR	2	9254.2	18.61	1247.8
Mark		Profile	Grade	QTY	Length	Area	Weight

Tekla structures

4 * D 25