


SHAFT DRAWING

| ALLOCATION TO ASSEMBLIES |       |
|--------------------------|-------|
| Assembly Mark            | TOTAL |
| B/77                     | 1     |
| Total                    | 1     |

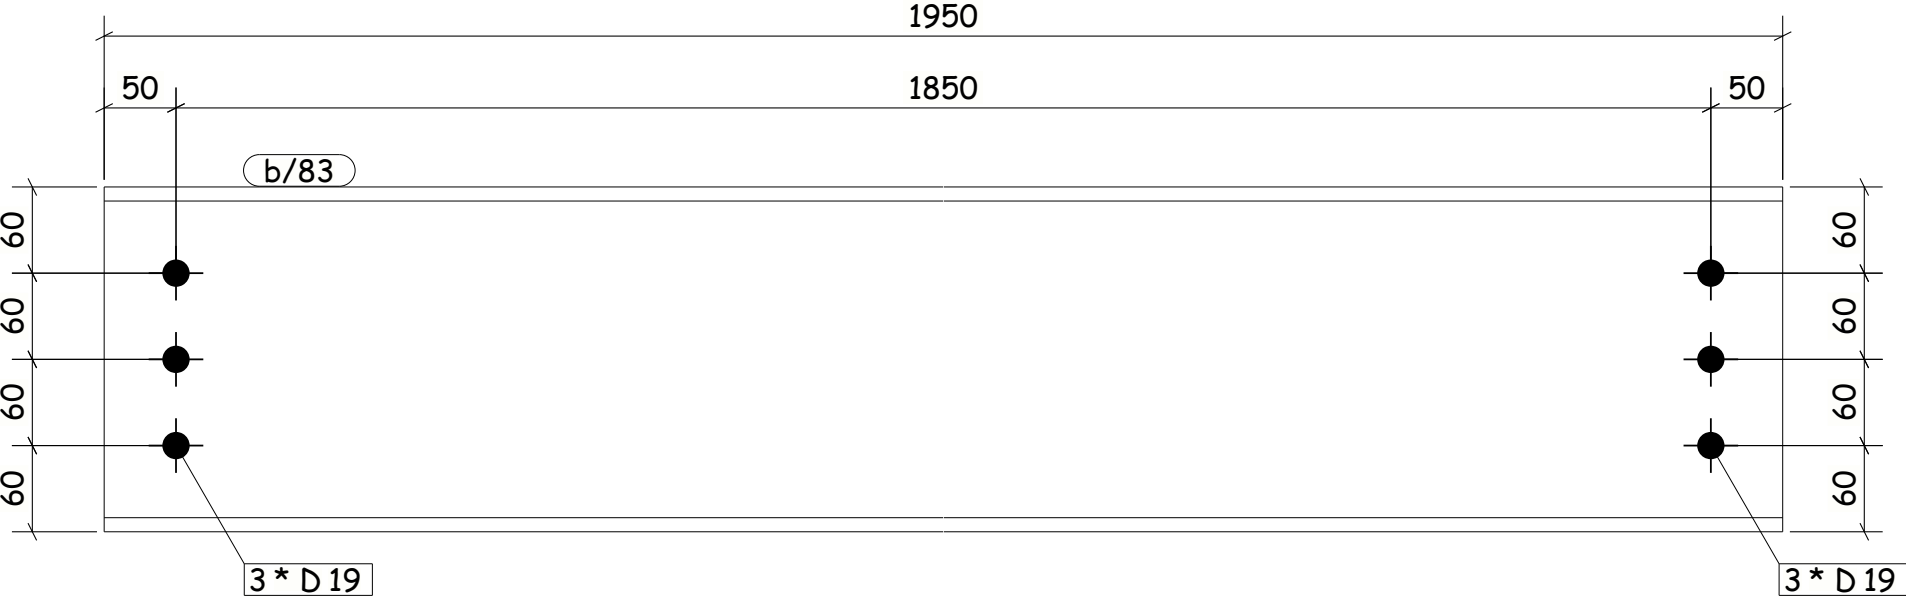

1 No BEAM

REQUIRED AS DRAWN MARKED b/83

|       |   |     |   |
|-------|---|-----|---|
| LOT   | 0 | QTY | 1 |
| PHASE | 1 | QTY | 1 |

| Rev  | By | Date    | Details |     |        |      |        |
|------|----|---------|---------|-----|--------|------|--------|
| b/83 |    | IPE240  | S235JR  | 1   | 1950.0 | 1.80 | 56.9   |
| Mark |    | Profile | Grade   | QTY | Length | Area | Weight |

Fabricación: HcB Ingeniería

Project: CTIB 2026

General Notes:

ALL HOLES 22 Dia UNO

FINISH: 0

Steel Grade: S235JR

Drawn:

Checked:

Scale: N.T.S.

**HcB CTIB**

Job No. / Dwg No. / Rev

1 / b/83 /

A4