
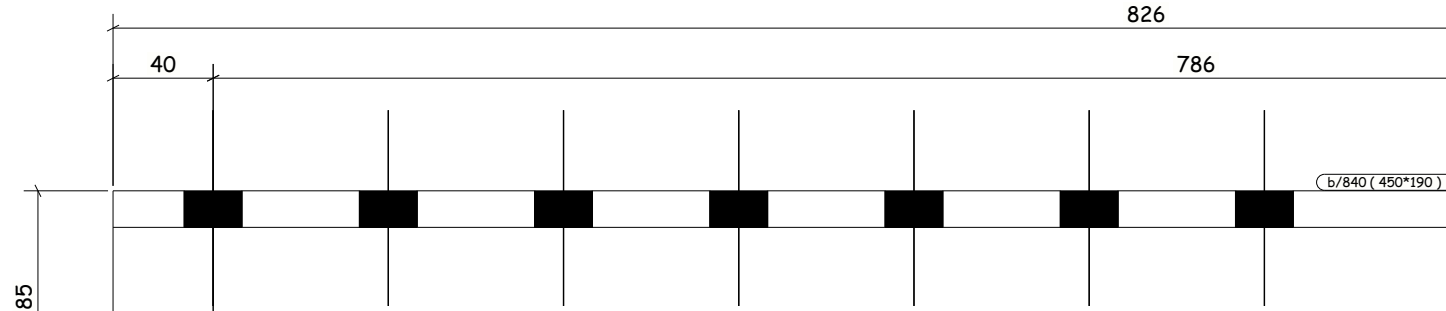


SHAFT DRAWING

ALLOCATION TO ASSEMBLIES	
Assembly Mark	TOTAL
C/2	1
Total	1

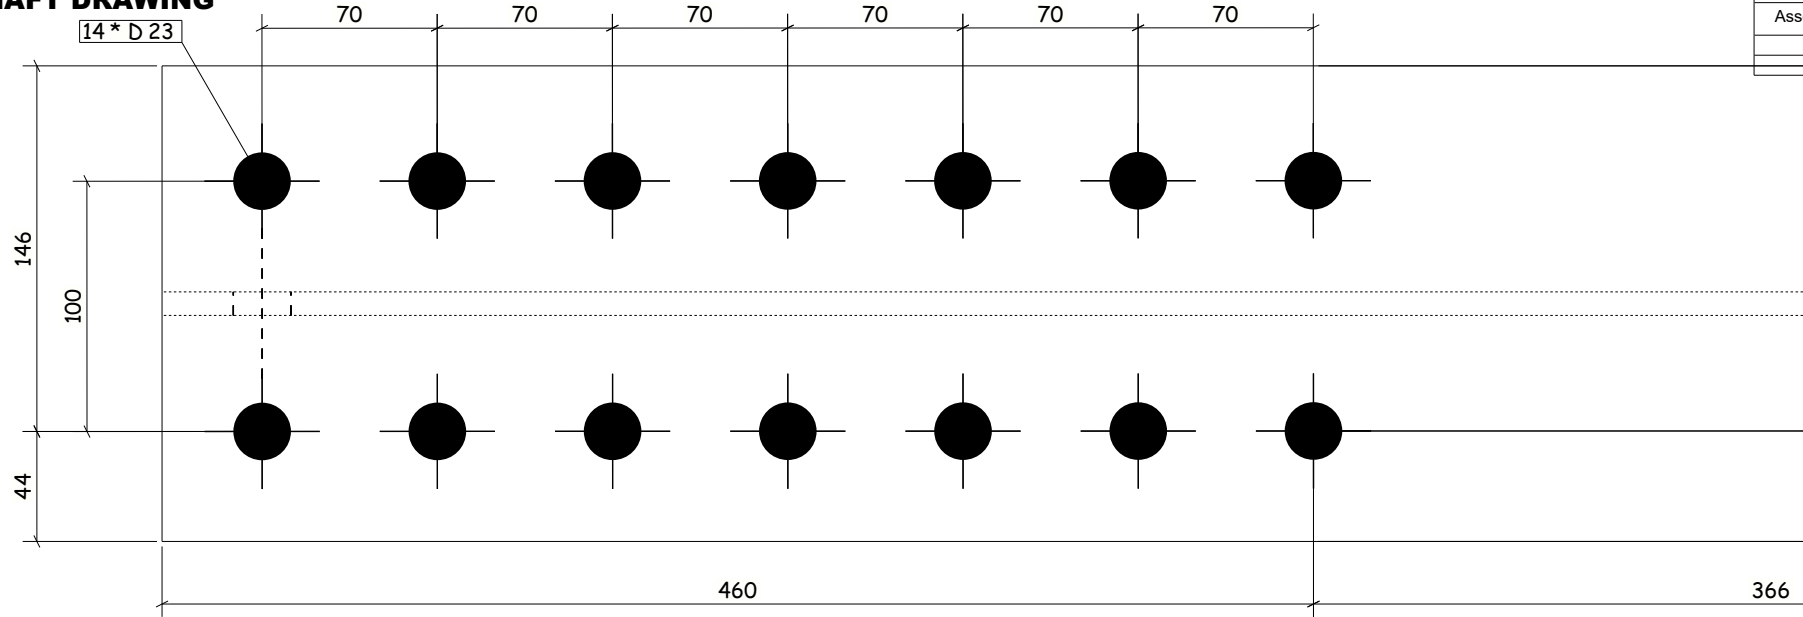

5 * D 23 No BEAM REQUIRED AS DRAWN MARKED b/840

LOT	0	QTY	1
PHASE	1	QTY	1

Fabricación: HcB Ingeniería

Project: CTIB 2026

General Notes:

ALL HOLES 22 Dia UNO

FINISH: 0

Steel Grade: S235JR

Drawn:

Checked:

Scale: N.T.S.

HcB CTIB

Job No. / Dwg No. / Rev

1 / b/840 /

Rev	By	Date	Details				
b/840	IPE450	S235JR	1	825.5	1.32	61.6	
Mark	profile	Grade	QTY	Length	Area	Weight	