


SHAFT DRAWING

ALLOCATION TO ASSEMBLIES	
Assembly Mark	TOTAL
B/1174	1
B/1275	1
C/2	1
Total	3

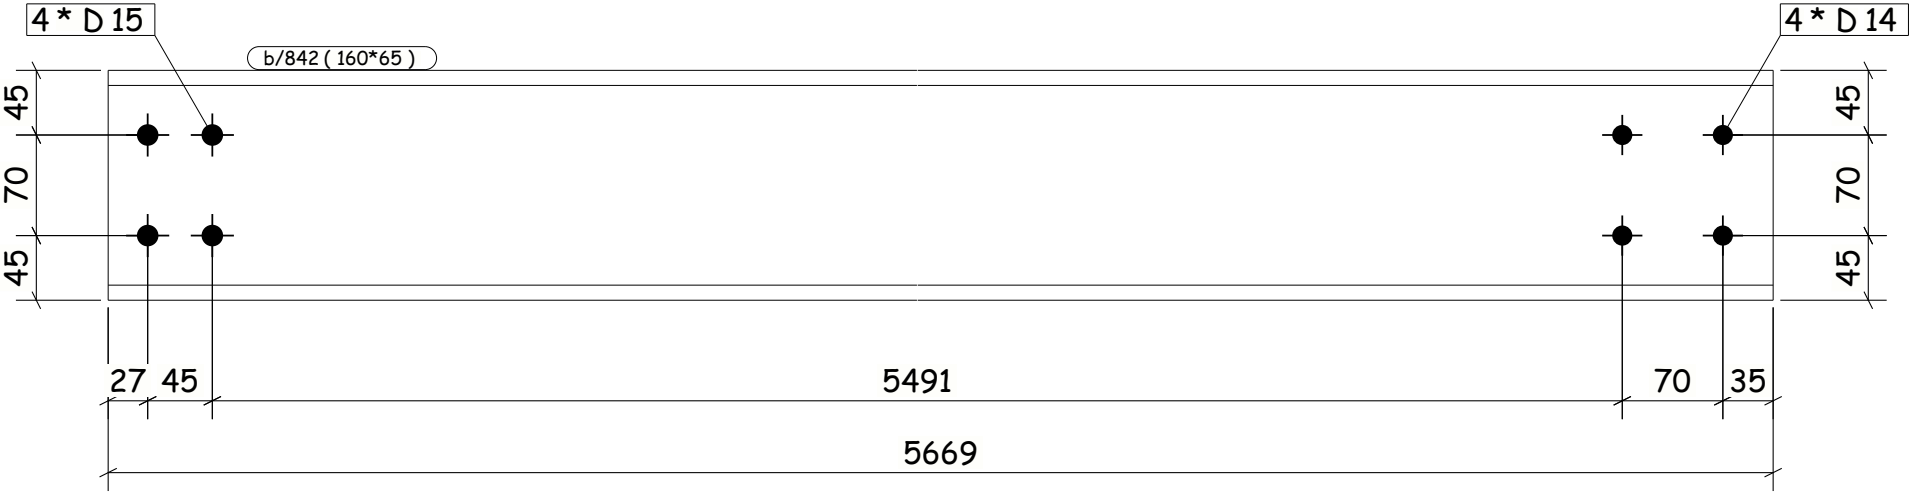

3 No BEAM REQUIRED AS DRAWN MARKED b/842

LOT	0	QTY	3
PHASE	1	QTY	3

Rev	By	Date	Details				
b/842		UPN160	S235JR	3	5668.6	3.12	107.1
Mark		Profile	Grade	QTY	Length	Area	Weight

Fabricación: HcB Ingeniería	
Project: CTIB 2026	
General Notes: ALL HOLES 22 Dia UNO FINISH: 0 Steel Grade: S235JR	Drawn:
	Checked:
	Scale: N.T.S.



Job No. /	Dwg No. /	Rev	A4
1 /	b/842 /		