


SHAFT DRAWING

ALLOCATION TO ASSEMBLIES	
Assembly Mark	TOTAL
B/13	8
B/14	1
B/30	1
B/274	1
B/372	1
B/384	1
B/385	1
B/428	1
B/485	1
B/987	1
B/988	1
B/989	1
B/991	1
B/1023	1
B/1032	1
B/1033	1
B/1060	2
B/1061	1
B/1062	1
B/1063	1
B/1088	1
B/1118	1
B/1119	1
B/1120	1
B/1287	1
Total	33

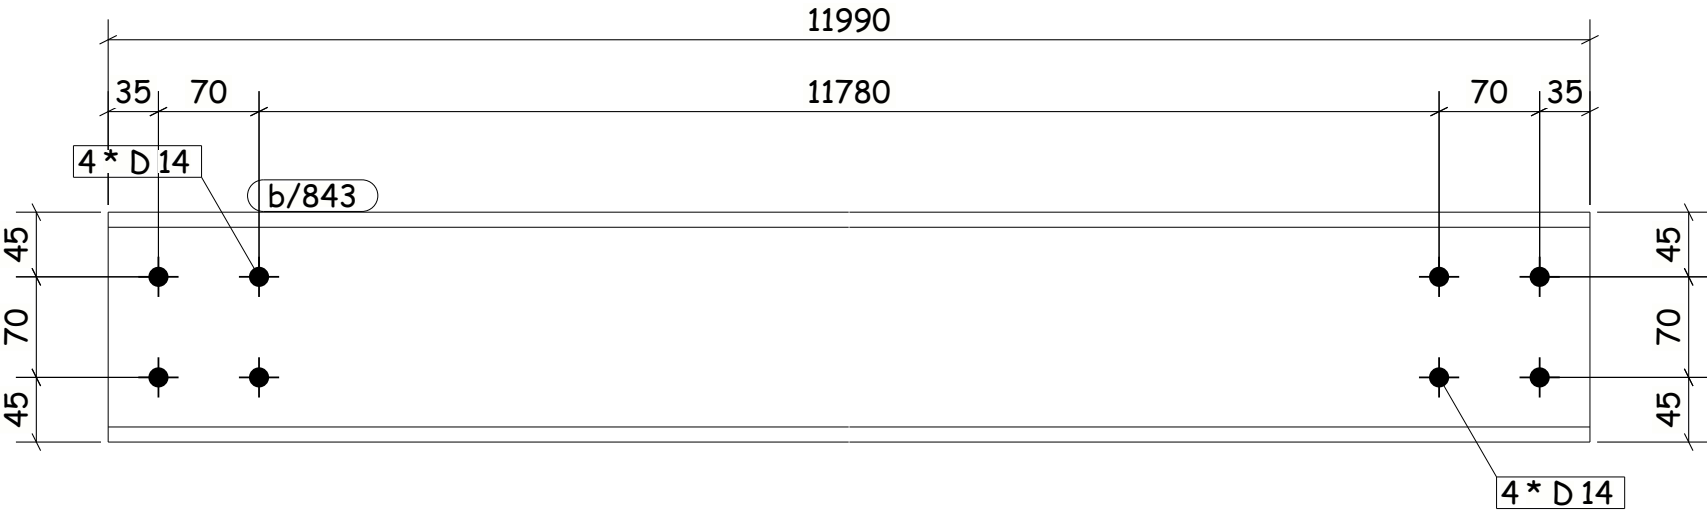

33 No BEAM

REQUIRED AS DRAWN MARKED b/843

LOT	0	QTY	33
PHASE	1	QTY	33

Rev	By	Date	Details				
b/843		UPN160	S235JR	33	11990.0	6.59	226.6
Mark		Profile	Grade	QTY	Length	Area	Weight

Fabricación: HcB Ingeniería

Project: CTIB 2026

General Notes:

ALL HOLES 22 Dia UNO

FINISH: 0

Steel Grade: S235JR

Drawn:

Checked:

Scale: N.T.S.

HcB CTIB

Job No. / Dwg No. / Rev

1 / b/843 /

A4