


SHAFT DRAWING

ALLOCATION TO ASSEMBLIES	
Assembly Mark	TOTAL
B/30	1
B/274	1
B/991	1
B/1185	1
Total	4

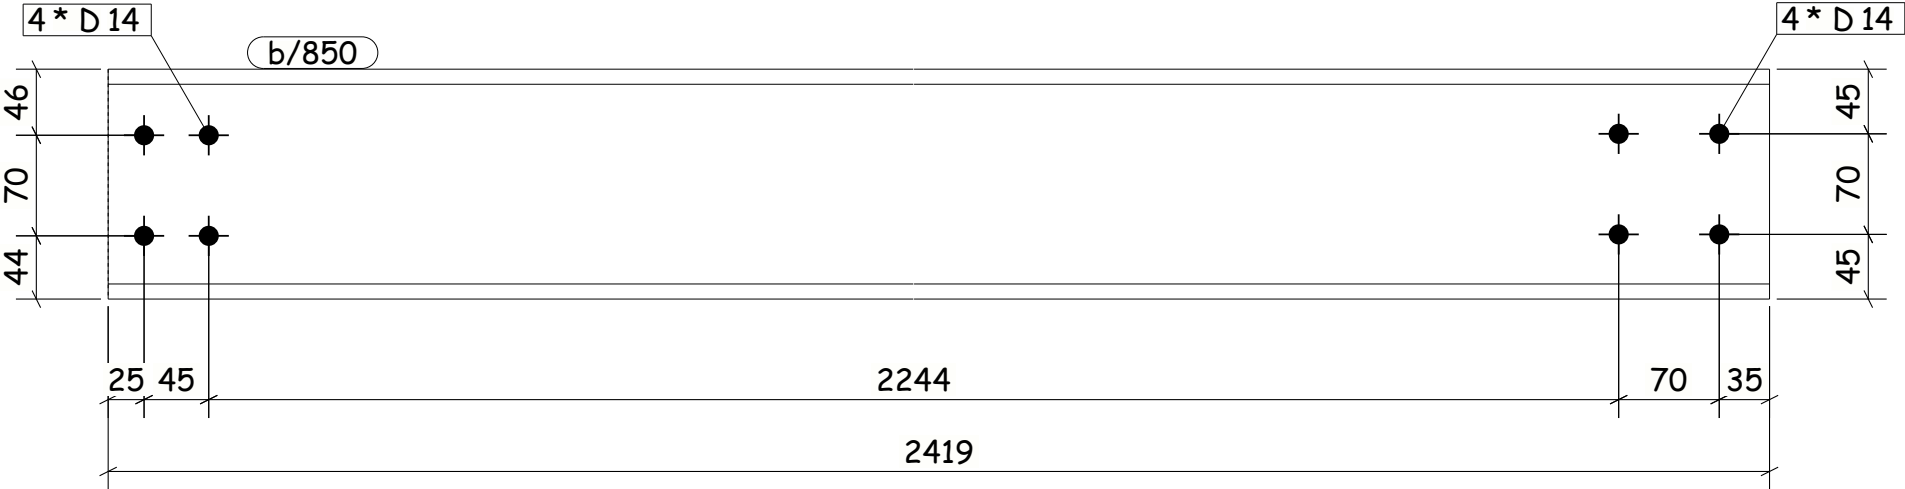

4 No BEAM REQUIRED AS DRAWN MARKED b/850

LOT	0	QTY	4
PHASE	1	QTY	4

Rev	By	Date	Details				
b/850	UPN160		S235JR	4	2419.3	1.33	45.7
Mark	Profile		Grade	QTY	Length	Area	Weight

Fabricación: HcB Ingeniería	
Project: CTIB 2026	
General Notes:	Drawn:
ALL HOLES 22 Dia UNO	Checked:
FINISH: 0	Scale: N.T.S.
Steel Grade: S235JR	



Job No. /	Dwg No. /	Rev	A4
1 /	b/850 /		