


SHAFT DRAWING

ALLOCATION TO ASSEMBLIES	
Assembly Mark	TOTAL
B/30	1
B/274	1
B/485	1
B/991	1
B/1032	1
Total	5

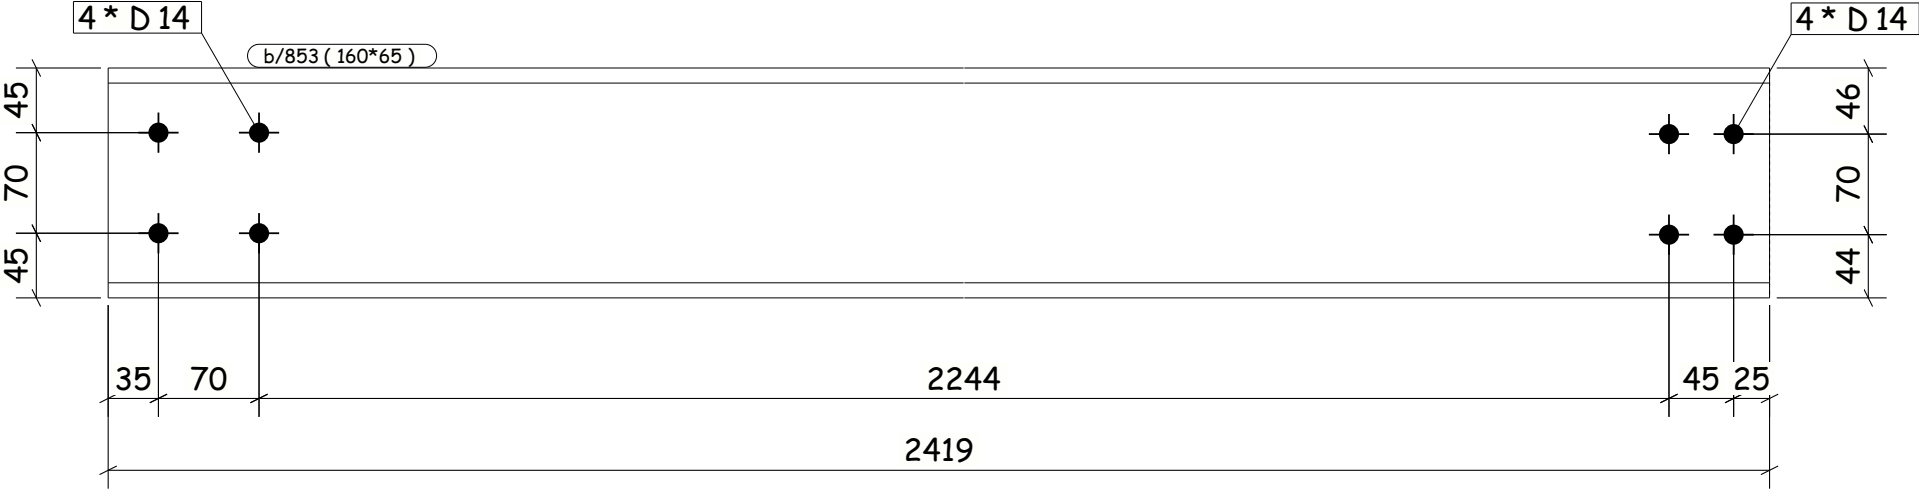

5 No BEAM REQUIRED AS DRAWN MARKED b/853

LOT	0	QTY	5
PHASE	1	QTY	5

Rev	By	Date	Details				
b/853		UPN160	S235JR	5	2419.2	1.33	45.7
Mark		Profile	Grade	QTY	Length	Area	Weight

Fabricación: HcB Ingeniería	
Project: CTIB 2026	
General Notes:	Drawn:
ALL HOLES 22 Dia UNO	Checked:
FINISH: 0	Scale: N.T.S.
Steel Grade: S235JR	



Job No. /	Dwg No. /	Rev	A4
1 /	b/853 /		