


SHAFT DRAWING

| ALLOCATION TO ASSEMBLIES |       |
|--------------------------|-------|
| Assembly Mark            | TOTAL |
| B/372                    | 1     |
| B/1088                   | 1     |
| B/1178                   | 1     |
| Total                    | 3     |

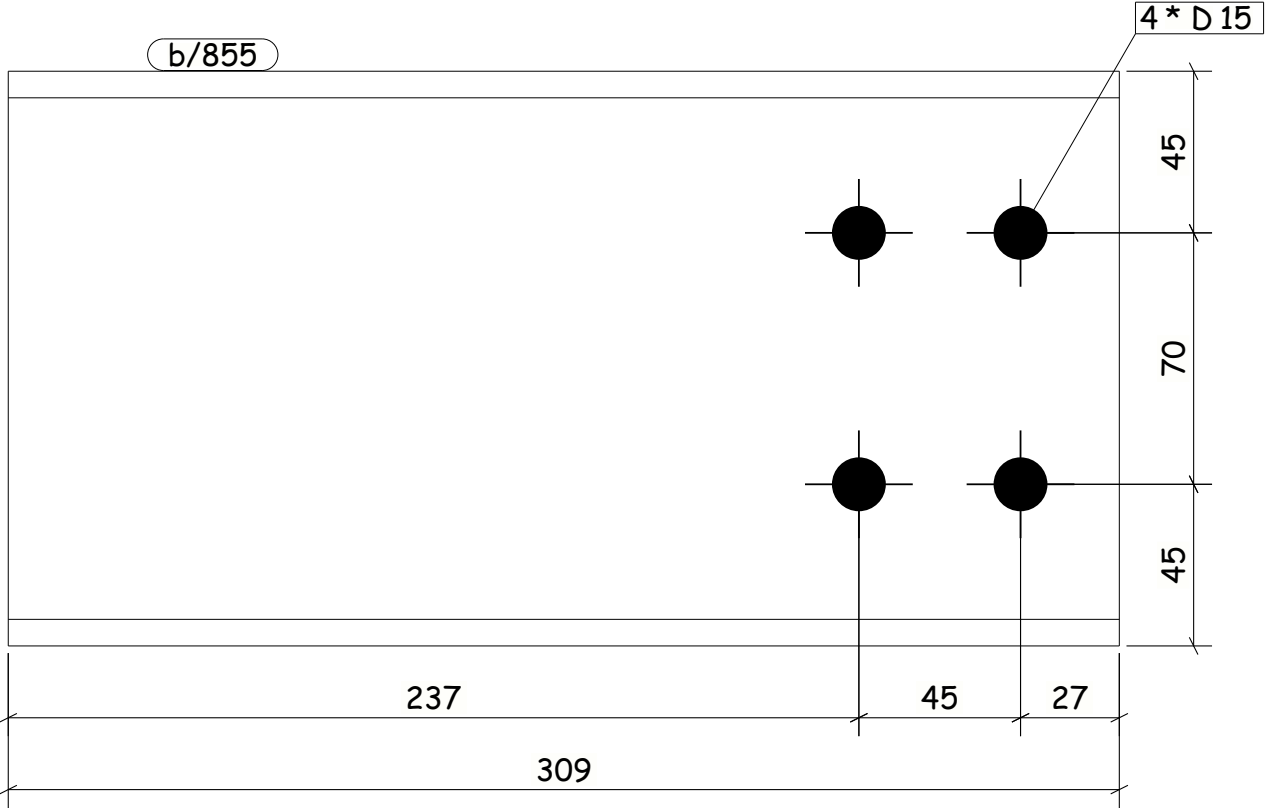

3 No BEAM

REQUIRED AS DRAWN MARKED b/855

|       |   |     |   |
|-------|---|-----|---|
| LOT   | 0 | QTY | 3 |
| PHASE | 1 | QTY | 3 |

| Rev   | By | Date    | Details |     |        |      |        |
|-------|----|---------|---------|-----|--------|------|--------|
| b/855 |    | IPE160  | S235JR  | 3   | 309.3  | 0.19 | 4.7    |
| Mark  |    | Profile | Grade   | QTY | Length | Area | Weight |

|                             |               |
|-----------------------------|---------------|
| Fabricación: HcB Ingeniería |               |
| Project: CTIB 2026          |               |
| General Notes:              | Drawn:        |
| ALL HOLES 22 Dia UNO        | Checked:      |
| FINISH: 0                   | Scale: N.T.S. |
| Steel Grade: S235JR         |               |



|           |           |     |    |
|-----------|-----------|-----|----|
| Job No. / | Dwg No. / | Rev | A4 |
| 1 /       | b/855 /   |     |    |