


SHAFT DRAWING

ALLOCATION TO ASSEMBLIES	
Assembly Mark	TOTAL
B/32	1
B/1068	2
Total	3

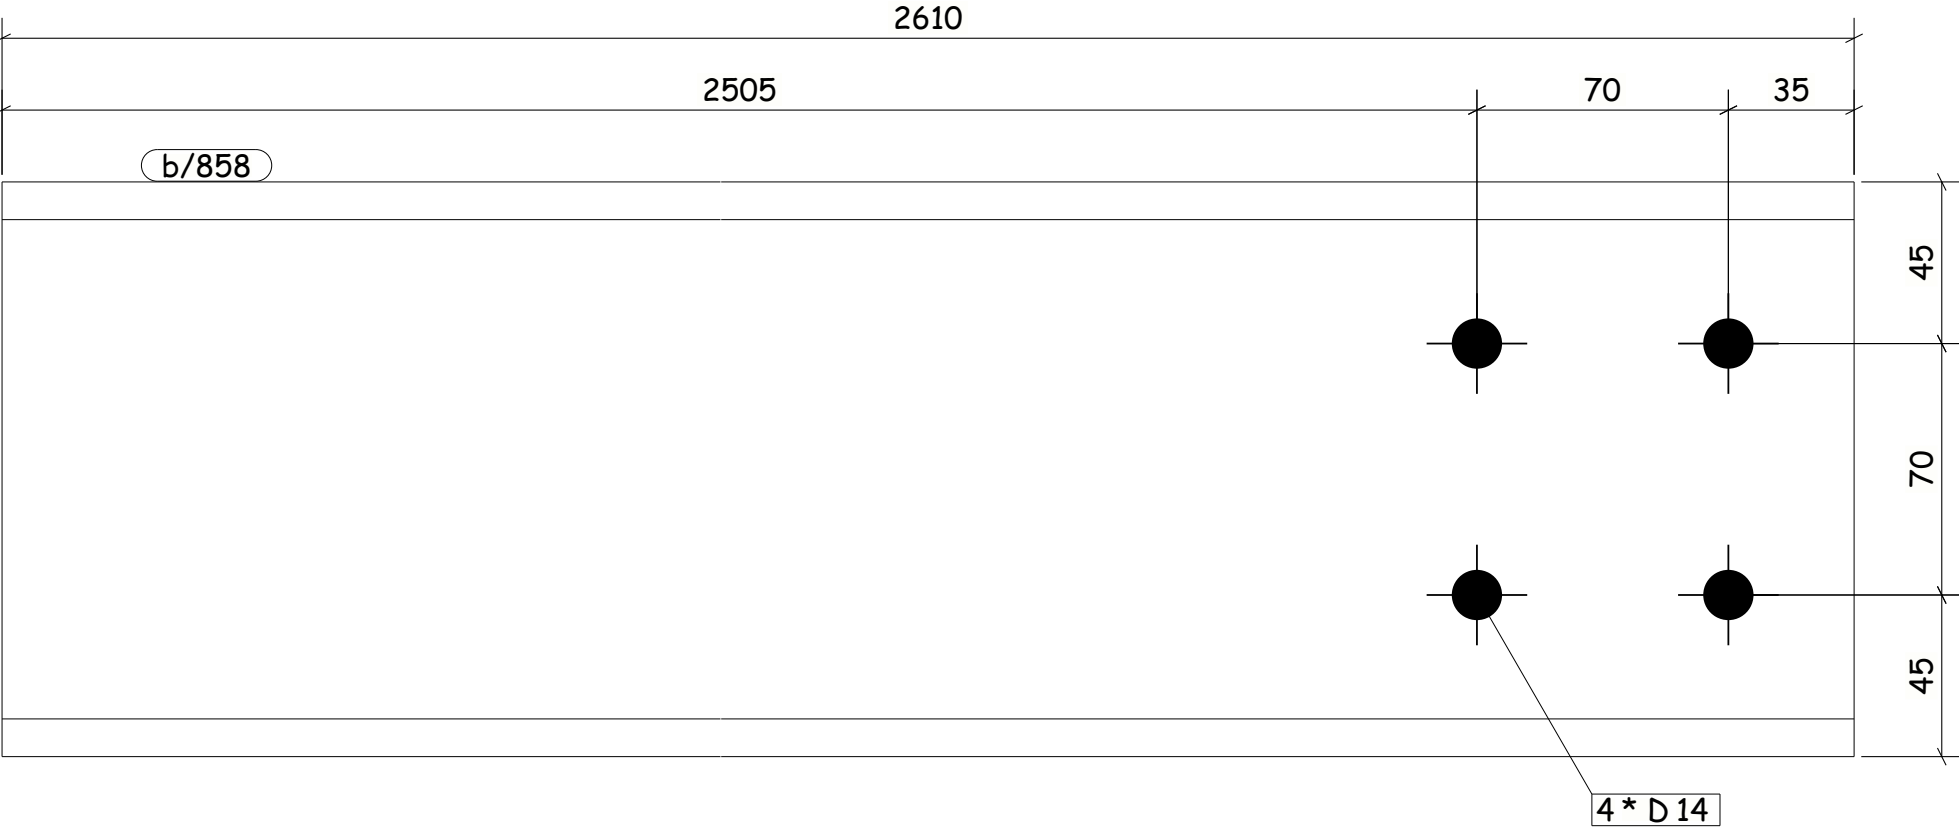

3 No BEAM REQUIRED AS DRAWN MARKED b/858

LOT	0	QTY	3
PHASE	1	QTY	3

Rev	By	Date	Details				
b/858	UPN160		S235JR	3	2610.2	1.44	49.3
Mark	Profile		Grade	QTY	Length	Area	Weight

Fabricación: HcB Ingeniería	
Project: CTIB 2026	
General Notes: ALL HOLES 22 Dia UNO FINISH: 0 Steel Grade: S235JR	Drawn:
	Checked:
	Scale: N.T.S.



Job No. /	Dwg No. /	Rev	A4
1 /	b/858 /		