


SHAFT DRAWING

ALLOCATION TO ASSEMBLIES	
Assembly Mark	TOTAL
B/78	1
B/210	3
Total	4

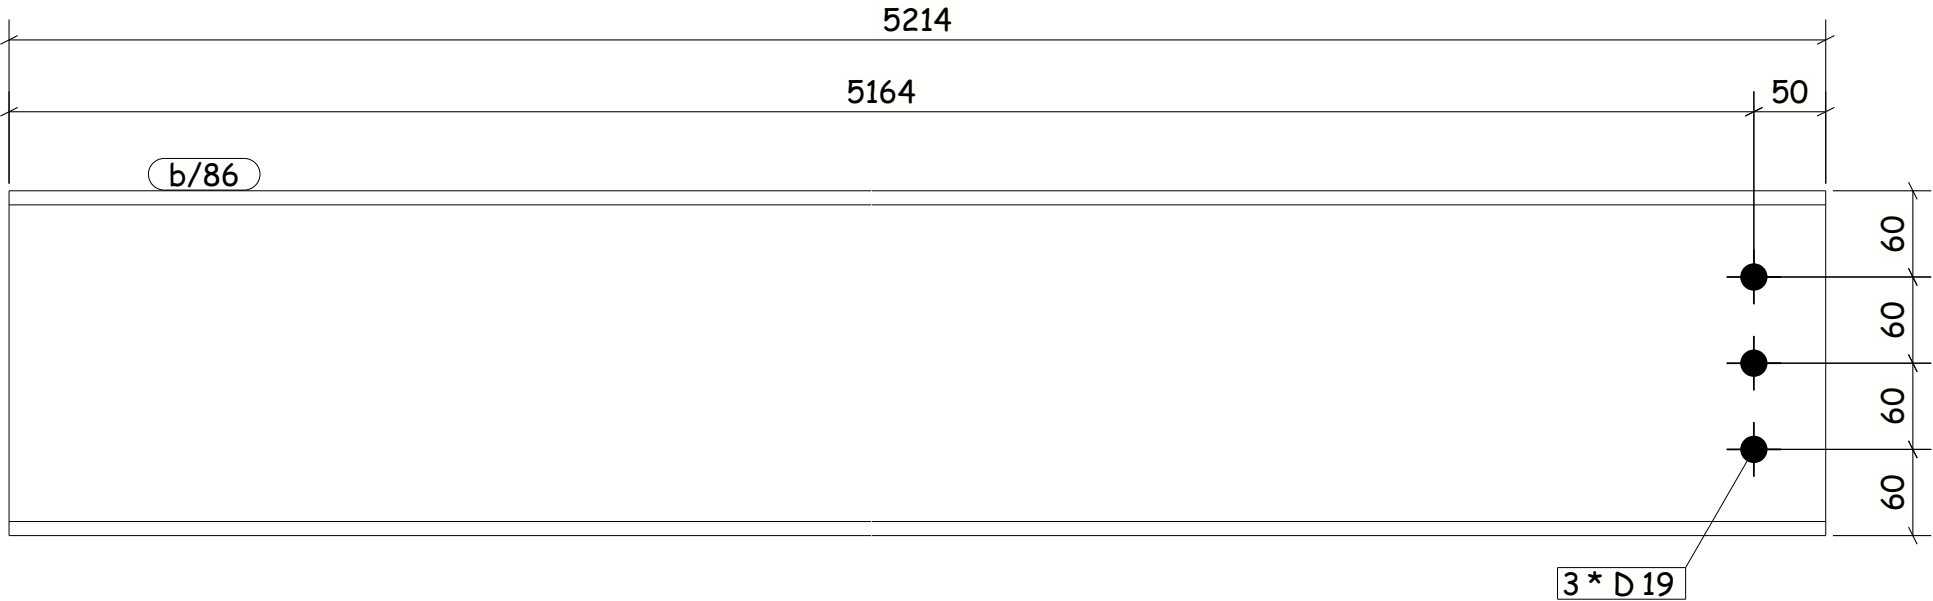

4 No BEAM REQUIRED AS DRAWN MARKED b/86

LOT	0	QTY	4
PHASE	1	QTY	4

Rev	By	Date	Details				
b/86		IPE240	S235JR	4	5213.9	4.81	152.2
Mark		Profile	Grade	QTY	Length	Area	Weight

Fabricación: HcB Ingeniería	
Project: CTIB 2026	
General Notes: ALL HOLES 22 Dia UNO FINISH: 0 Steel Grade: S235JR	Drawn:
	Checked:
	Scale: N.T.S.

HcB

CTIB

Job No. /	Dwg No. /	Rev	A4
1 /	b/86 /		