


SHAFT DRAWING

ALLOCATION TO ASSEMBLIES	
Assembly Mark	TOTAL
B/987	1
B/1061	1
B/1119	1
Total	3

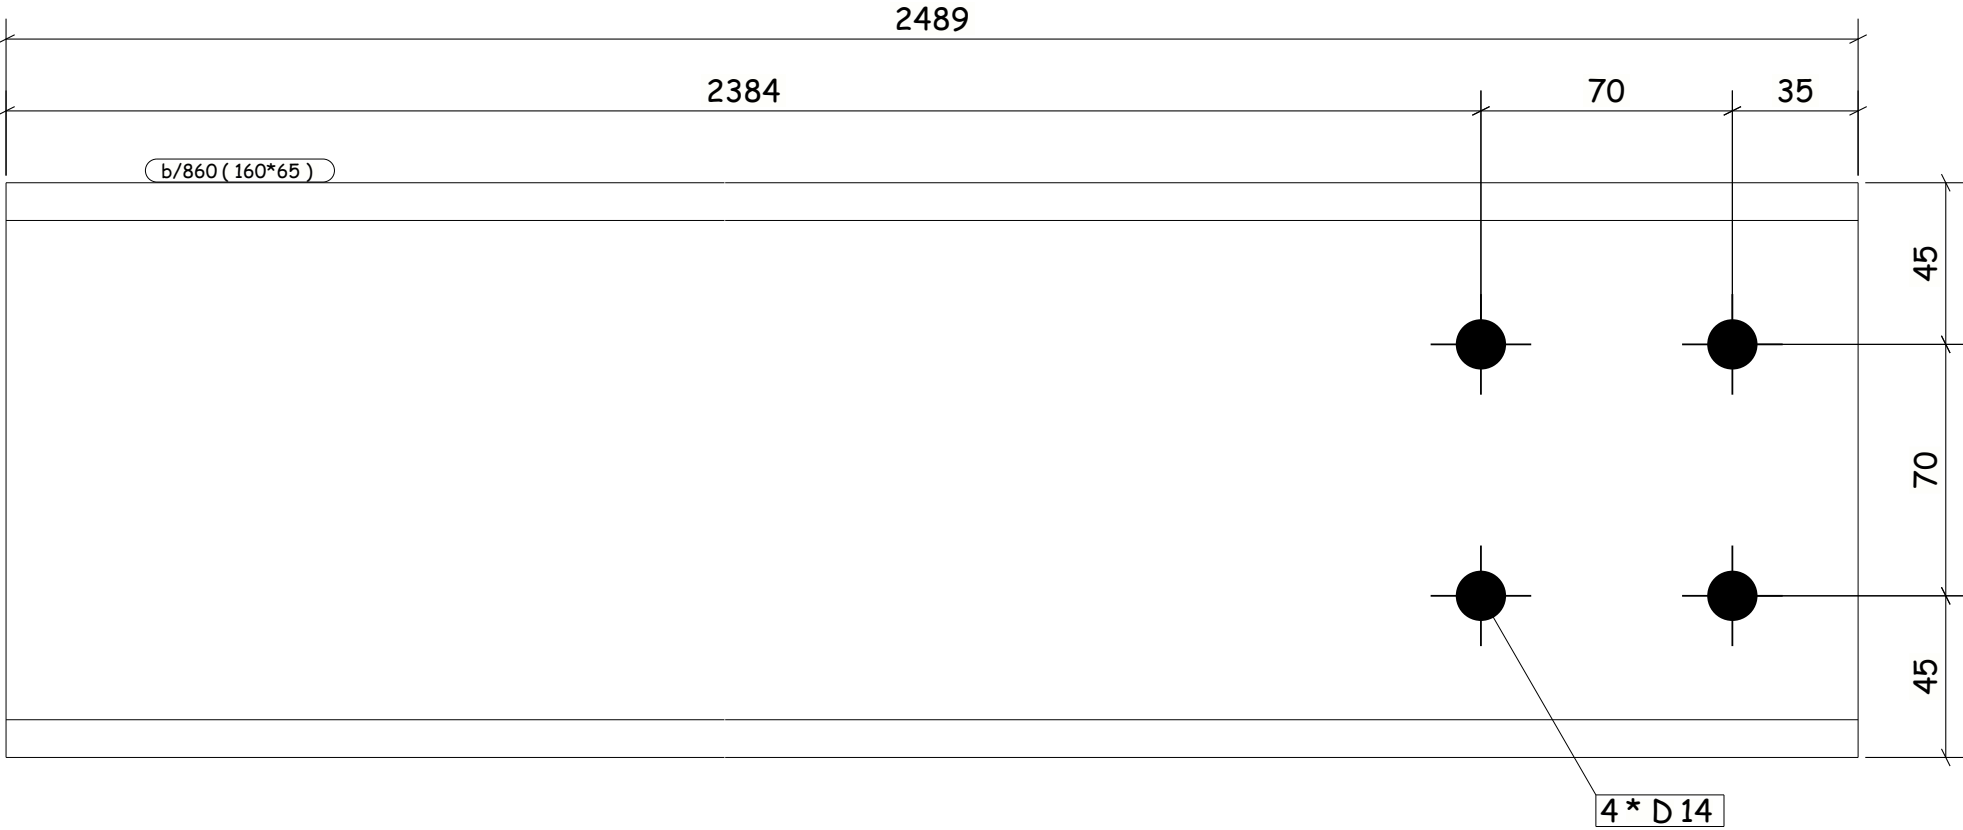

3 No BEAM REQUIRED AS DRAWN MARKED b/860

LOT	0	QTY	3
PHASE	1	QTY	3

Rev	By	Date	Details				
b/860		UPN160	S235JR	3	2489.3	1.37	47.0
Mark		Profile	Grade	QTY	Length	Area	Weight

Fabricación: HcB Ingeniería

Project: CTIB 2026

General Notes:

ALL HOLES 22 Dia UNO

FINISH: 0

Steel Grade: S235JR

Drawn:

Checked:

Scale: N.T.S.

HcB CTIB

Job No. / Dwg No. / Rev

1 / b/860 /

A4