


SHAFT DRAWING

ALLOCATION TO ASSEMBLIES	
Assembly Mark	TOTAL
B/1160	1
Total	1

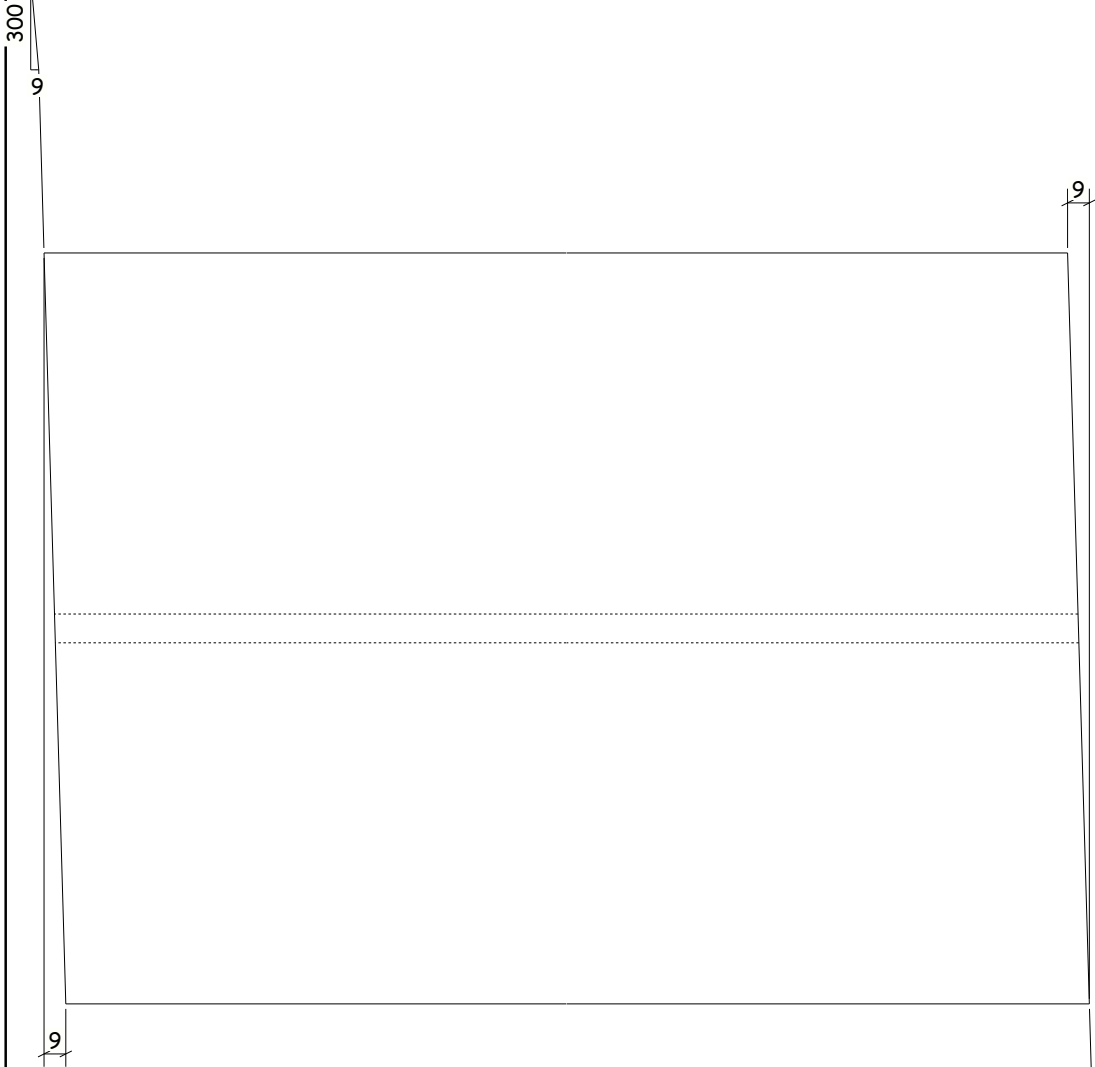

1 No BEAM REQUIRED AS DRAWN MARKED b/865

LOT	0	QTY	1
PHASE	1	QTY	1

Rev	By	Date	Details				
b/865	b/865	HEA450	S235JR	1	6479.4	13.03	872.5
Mark		Profile	Grade	QTY	Length	Area	Weight

Fabricación: 9-cB Ingeniería	
Project: COB 2026	
General Notes:	
ALL HOLES 22	Dia UNO
FINISH: 0	
Steel Grade:	S235JR

Drawn:
Checked:
Scale: N.T.S.



Job No. /	Dwg No. /	Rev
1	/ b/865	/