
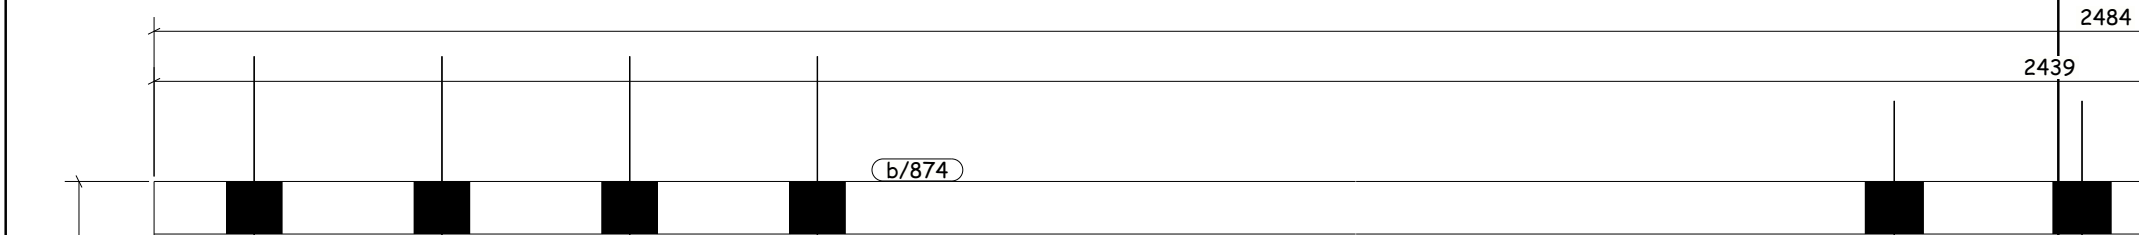


SHAFT DRAWING

ALLOCATION TO ASSEMBLIES	
Assembly Mark	75 CTAL
B/58	1
Total	1

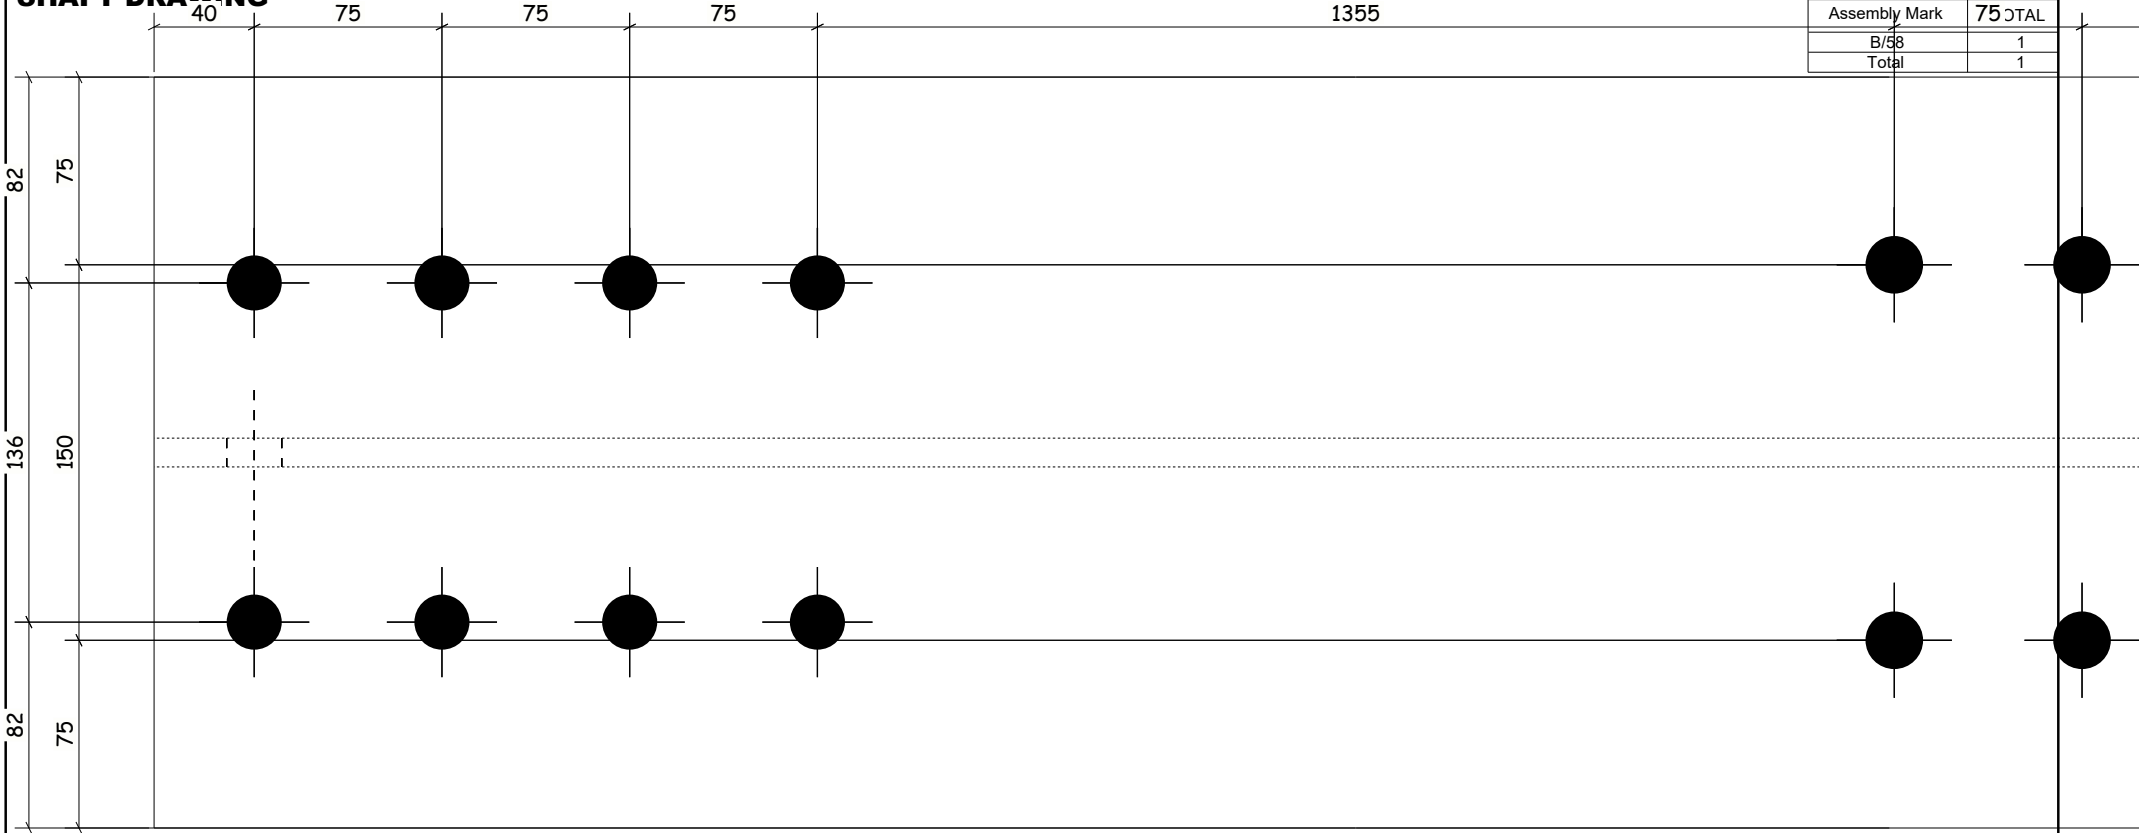

1 No BEAM

REQUIRED AS DRAWN MARKED b/874

LOT	0	QTY	1
PHASE	1	QTY	1

Rev	Date	Details					
b/874	HEA450	S235JR	1	2484.2	5.00	320.0	
Mark	Profile	Grade	QTY	Length	Area	Weight	

Fabricación: HcB Ingeniería

Project: CTIB 2026

General Notes:

ALL HOLES 22 Dia UNO

FINISH: 0

Steel Grade: S235JR

Drawn:

Checked:

Scale: N.T.S.

HcB CTIB

Job No. / Dwg No. / Rev

1 / b/874 /