


SHAFT DRAWING

ALLOCATION TO ASSEMBLIES	
Assembly Mark	TOTAL
B/1065	1
B/1121	1
C/2	1
Total	3

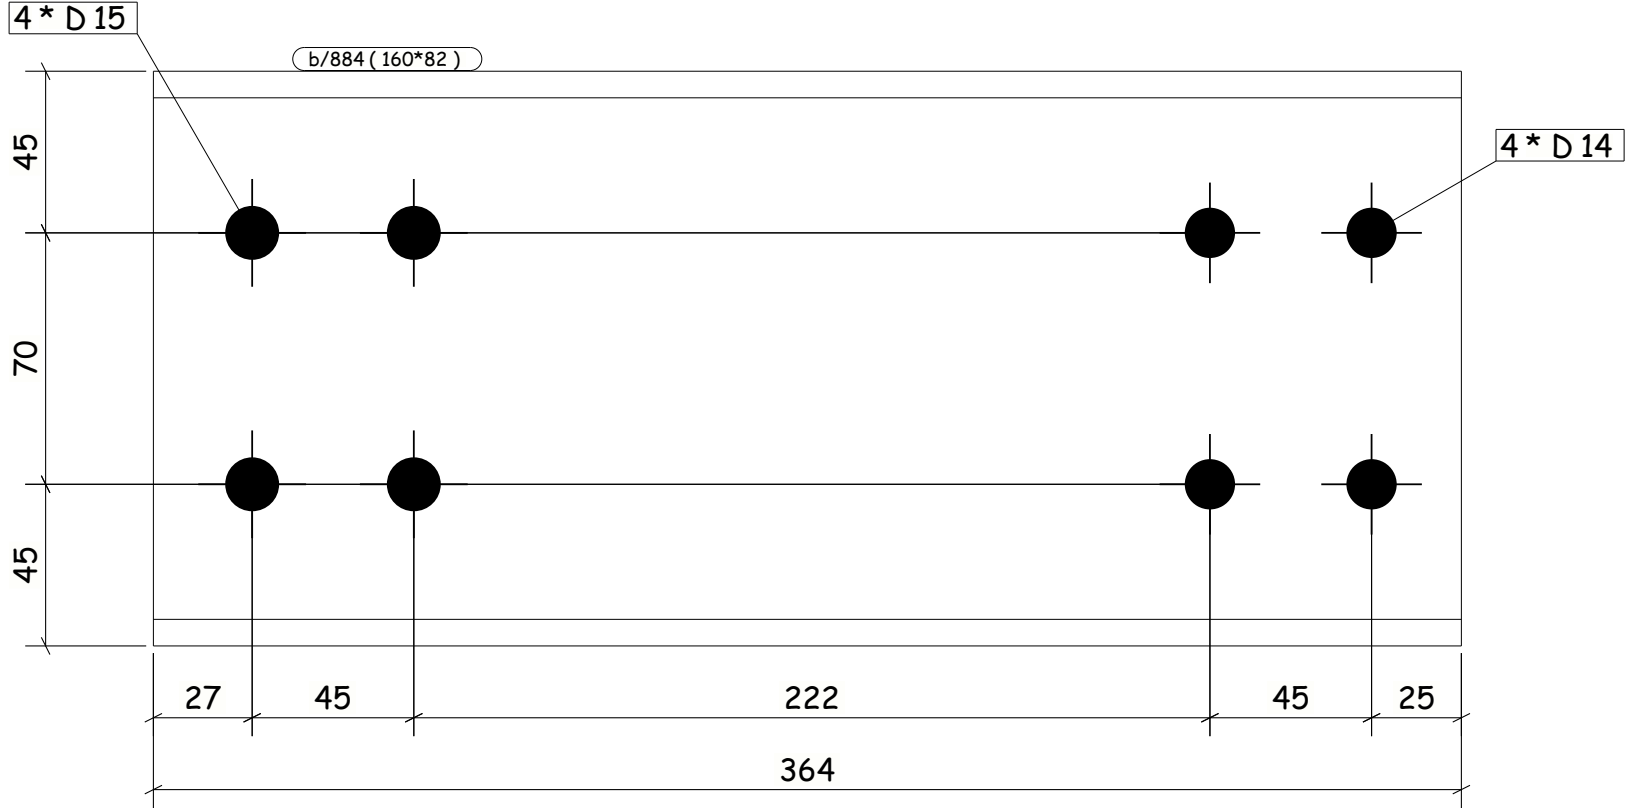

3 No BEAM REQUIRED AS DRAWN MARKED b/884

LOT	0	QTY	3
PHASE	1	QTY	3

Rev	By	Date	Details				
b/884	IPE160		S235JR	3	364.1	0.23	5.5
Mark	Profile		Grade	QTY	Length	Area	Weight

Fabricación: HcB Ingeniería	
Project: CTIB 2026	
General Notes:	Drawn:
ALL HOLES 22 Dia UNO	Checked:
FINISH: 0	Scale: N.T.S.
Steel Grade: S235JR	



Job No. /	Dwg No. /	Rev	A4
1 /	b/884 /		